



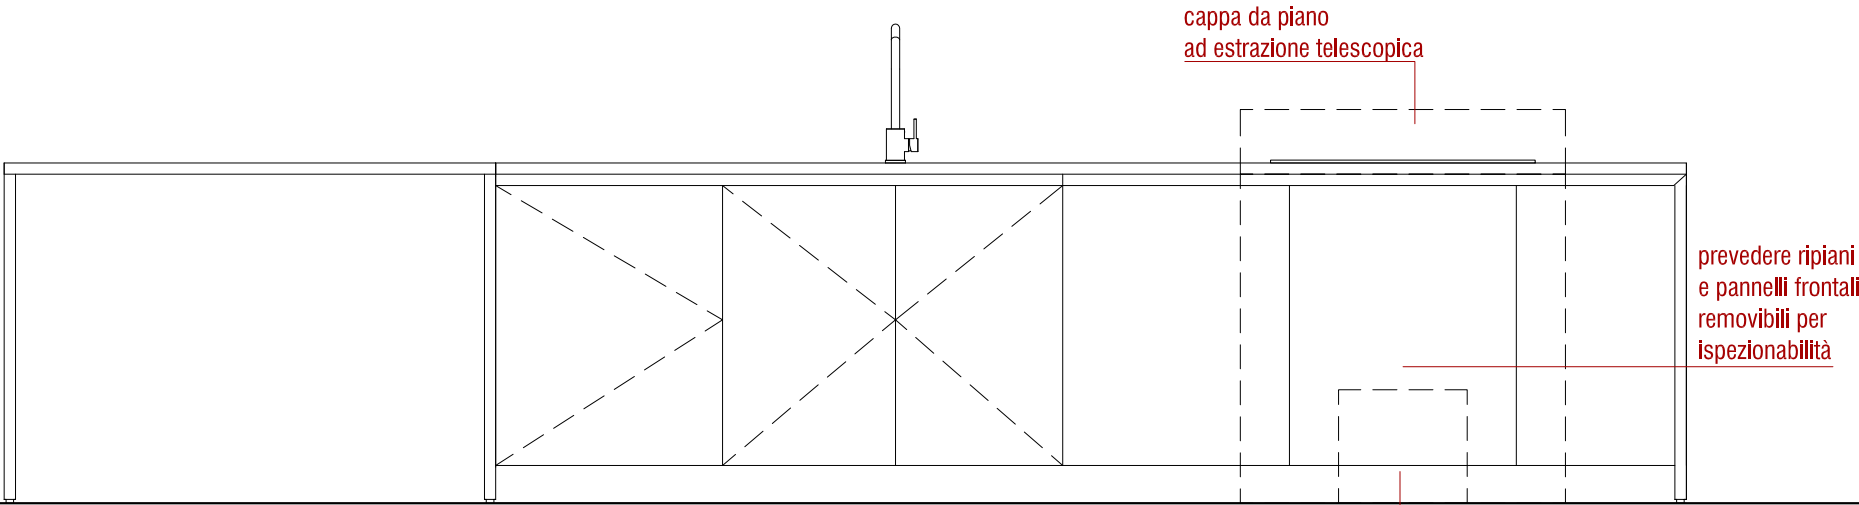


PROSPETTO LATO 1

ingombro indicativo
cappa da piano motore compreso

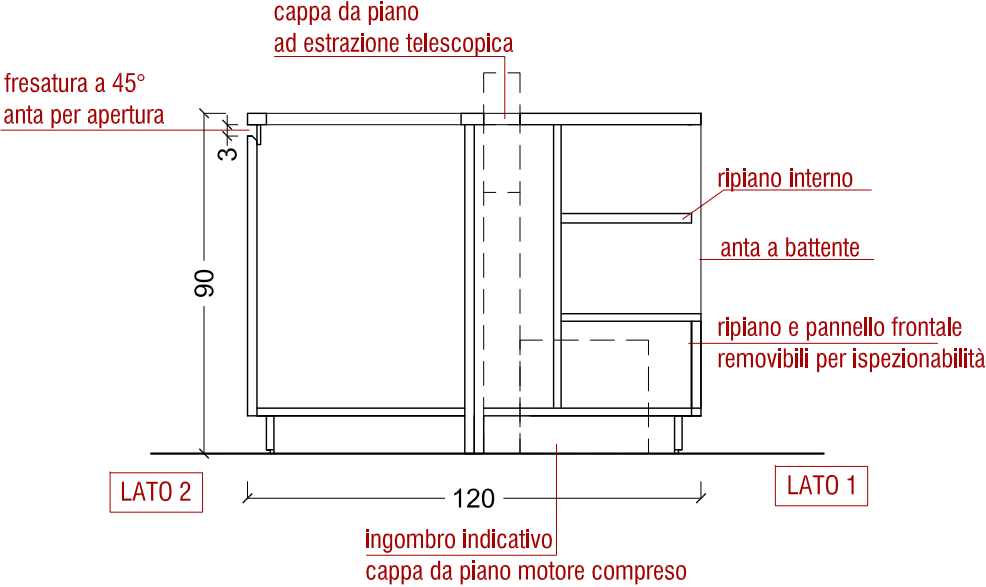

DETTAGLIO CUCINA CON CAPPDA PIANO
AD ESTRAZIONE TELESCOPICA

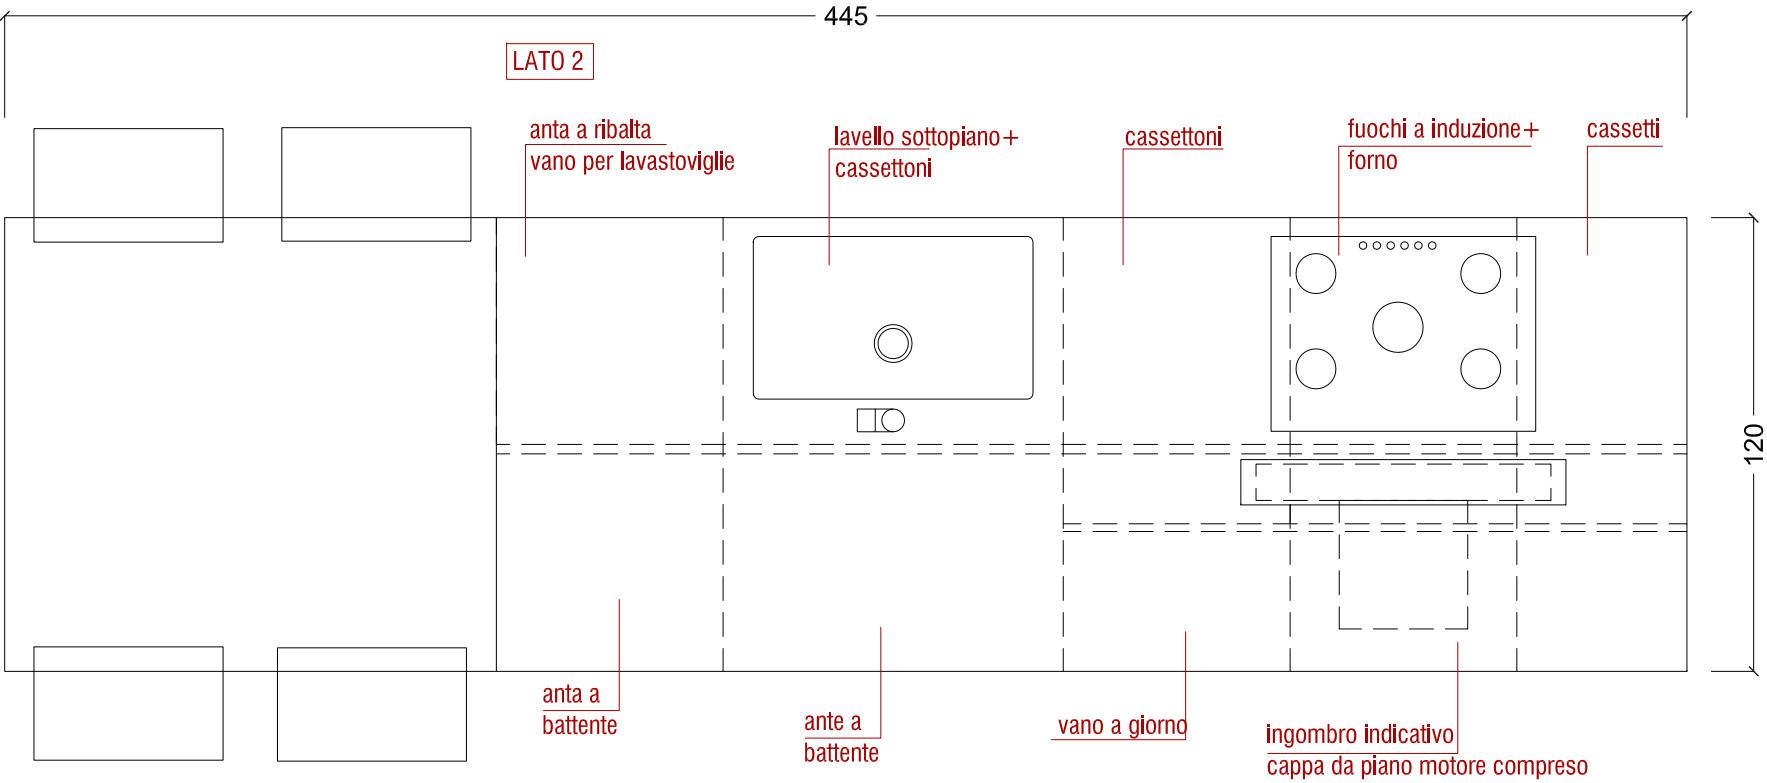

PIANTA

NOTA:
prevedere fori interni per la regolazione dei
ripiani in altezza