





1 Interior Render

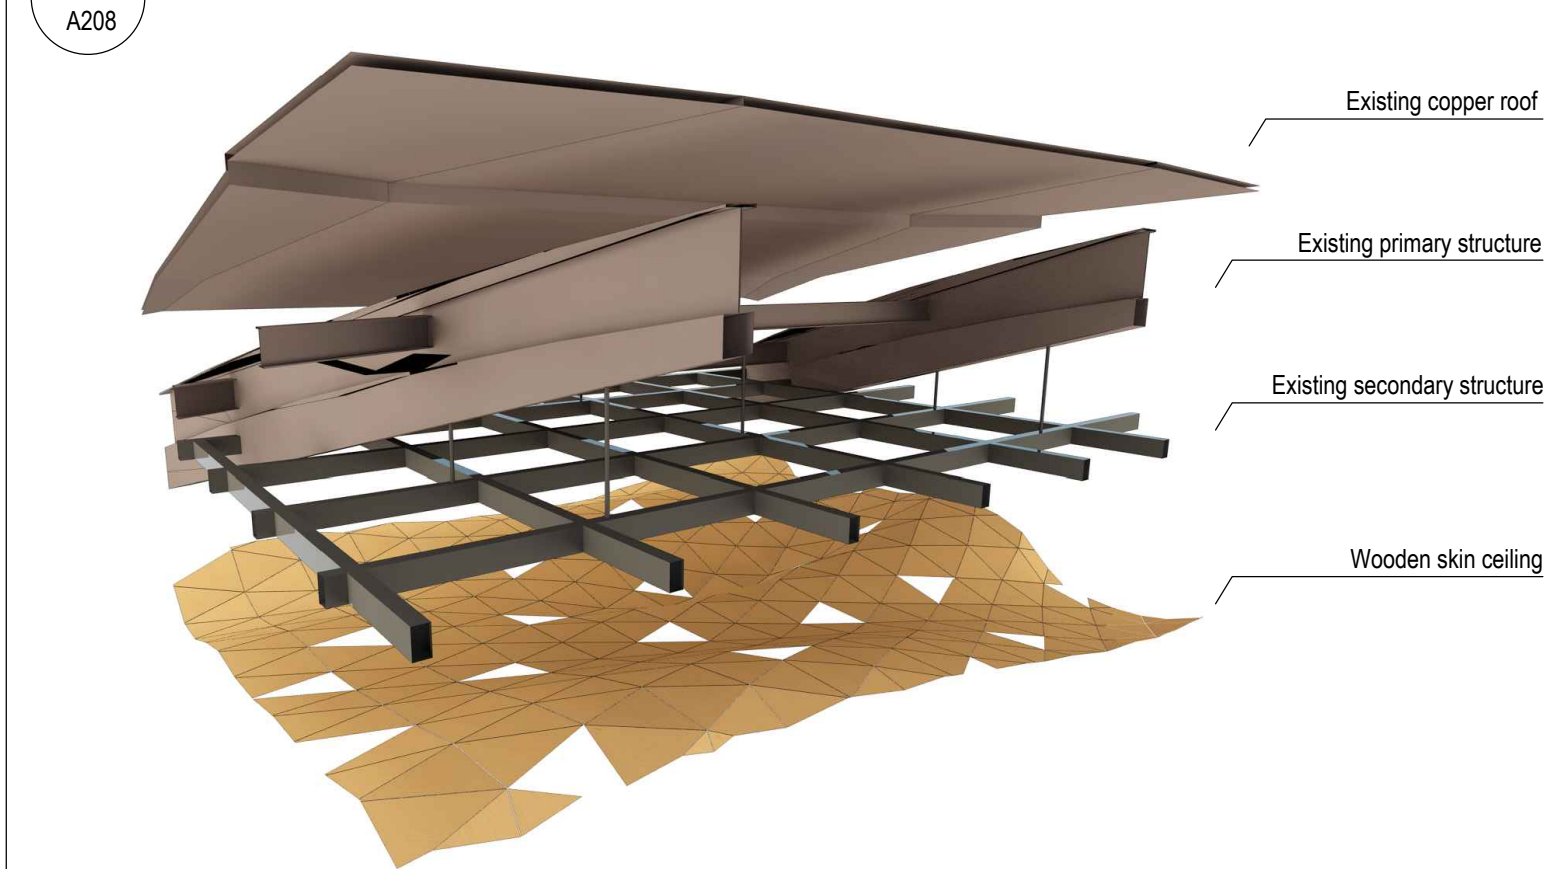


2 Roof Scheme

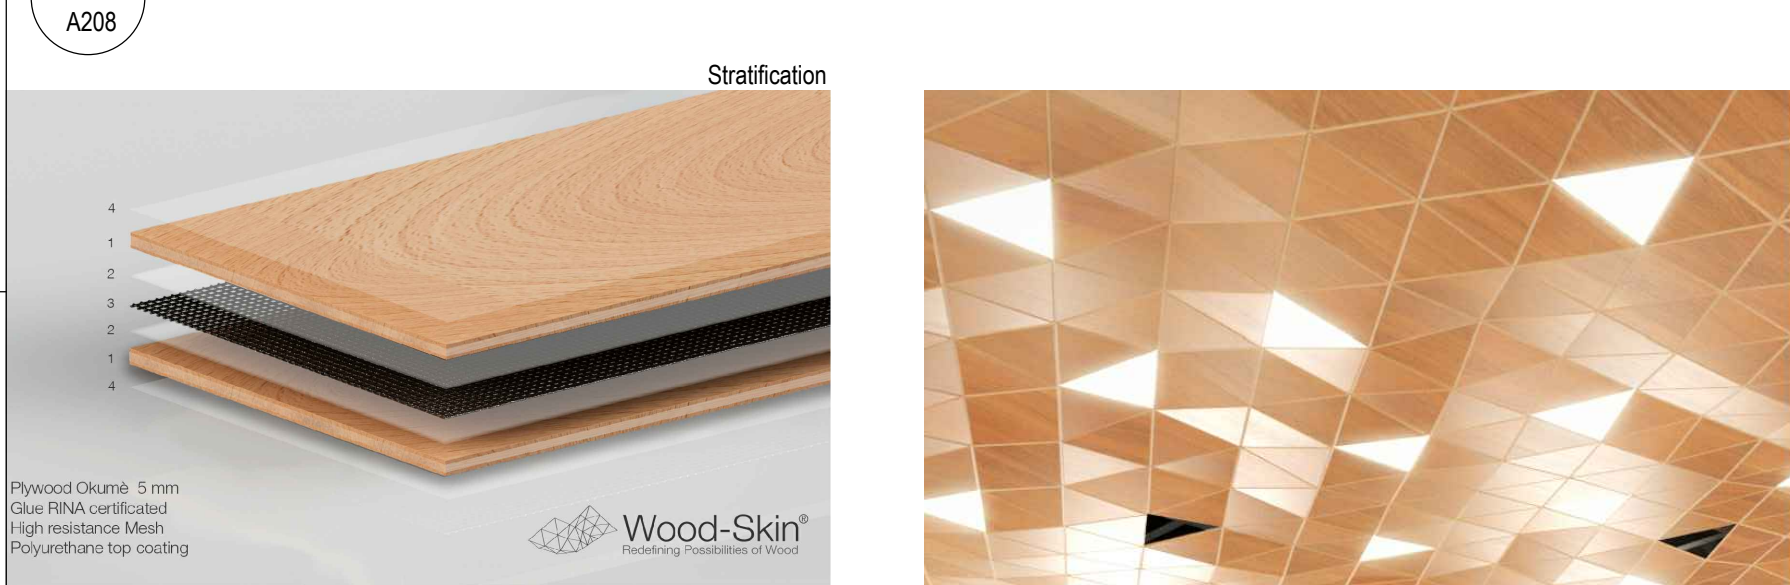


3 Woodskin characteristics


4 Woodskin Reference Image

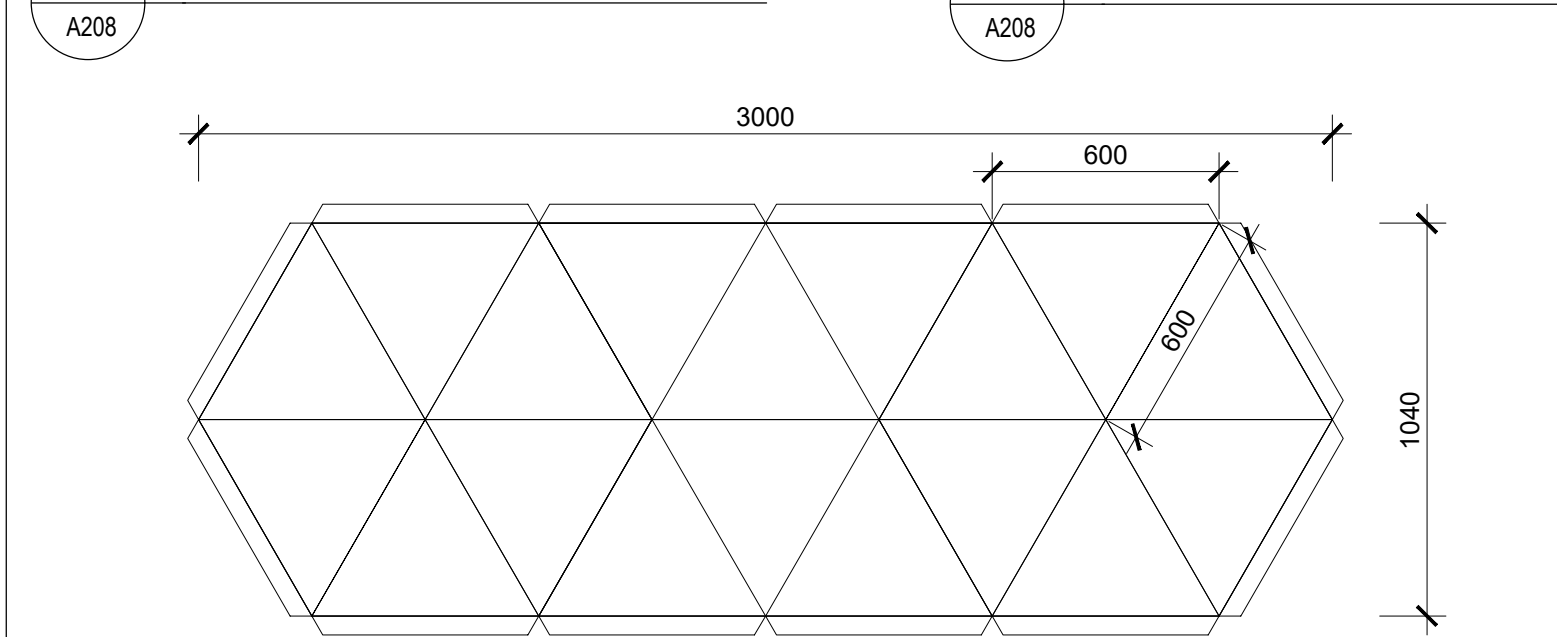


8 Single ceiling module - Plan

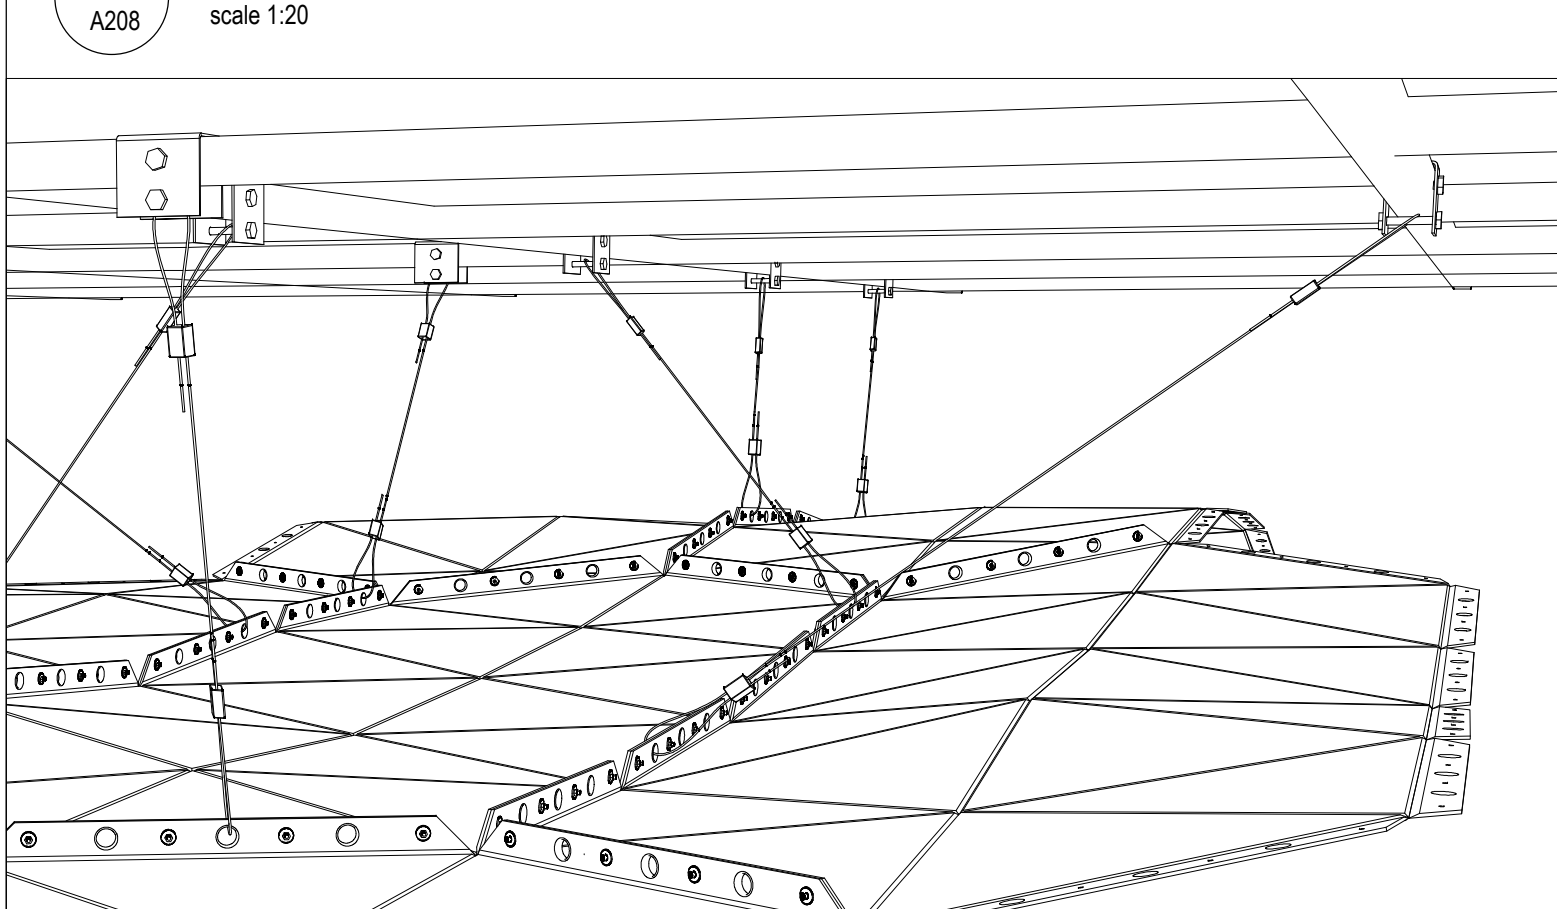


9 Ceiling Elements - 3d view

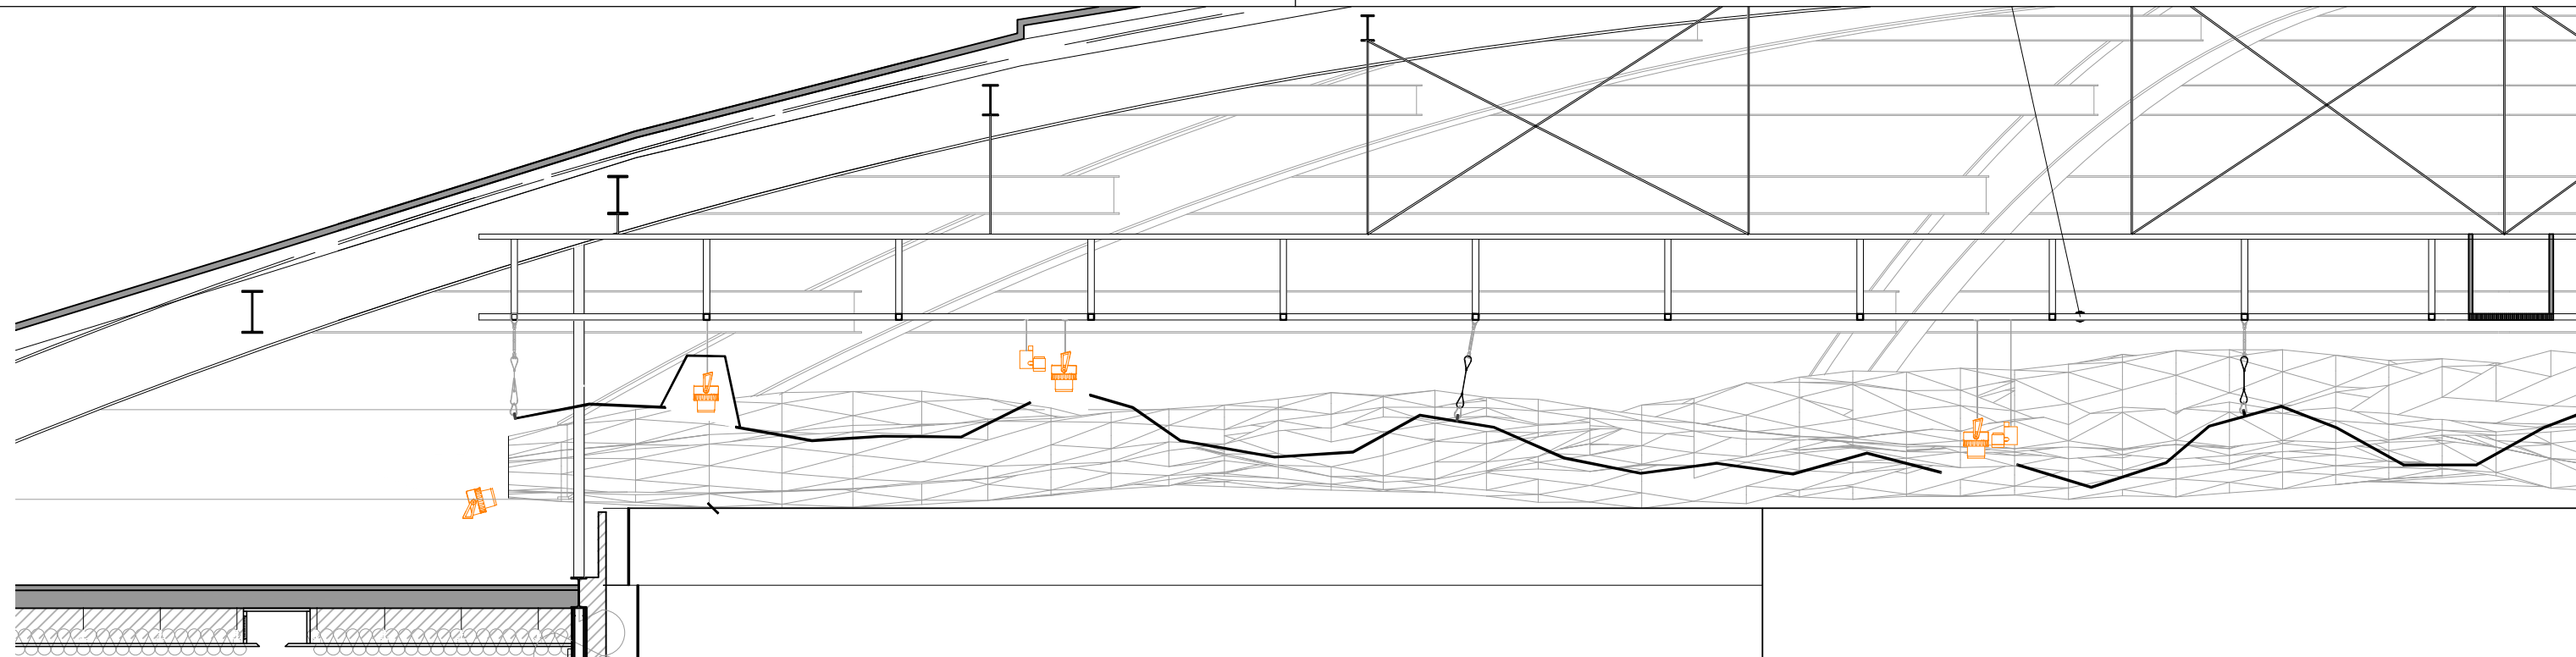


5 Section AA detail

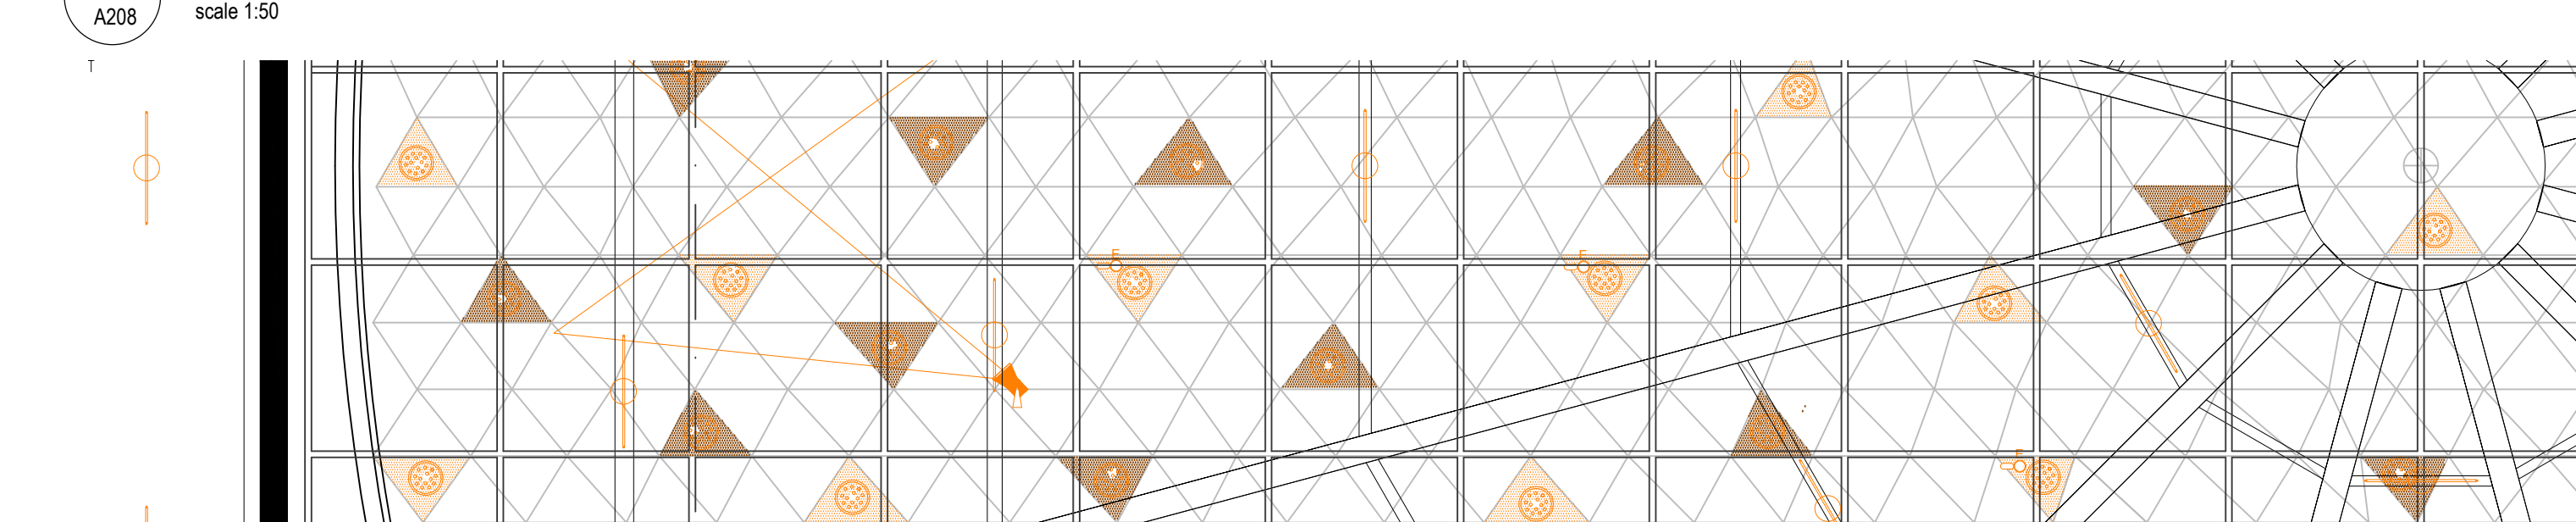


6 Roof Plan Detail

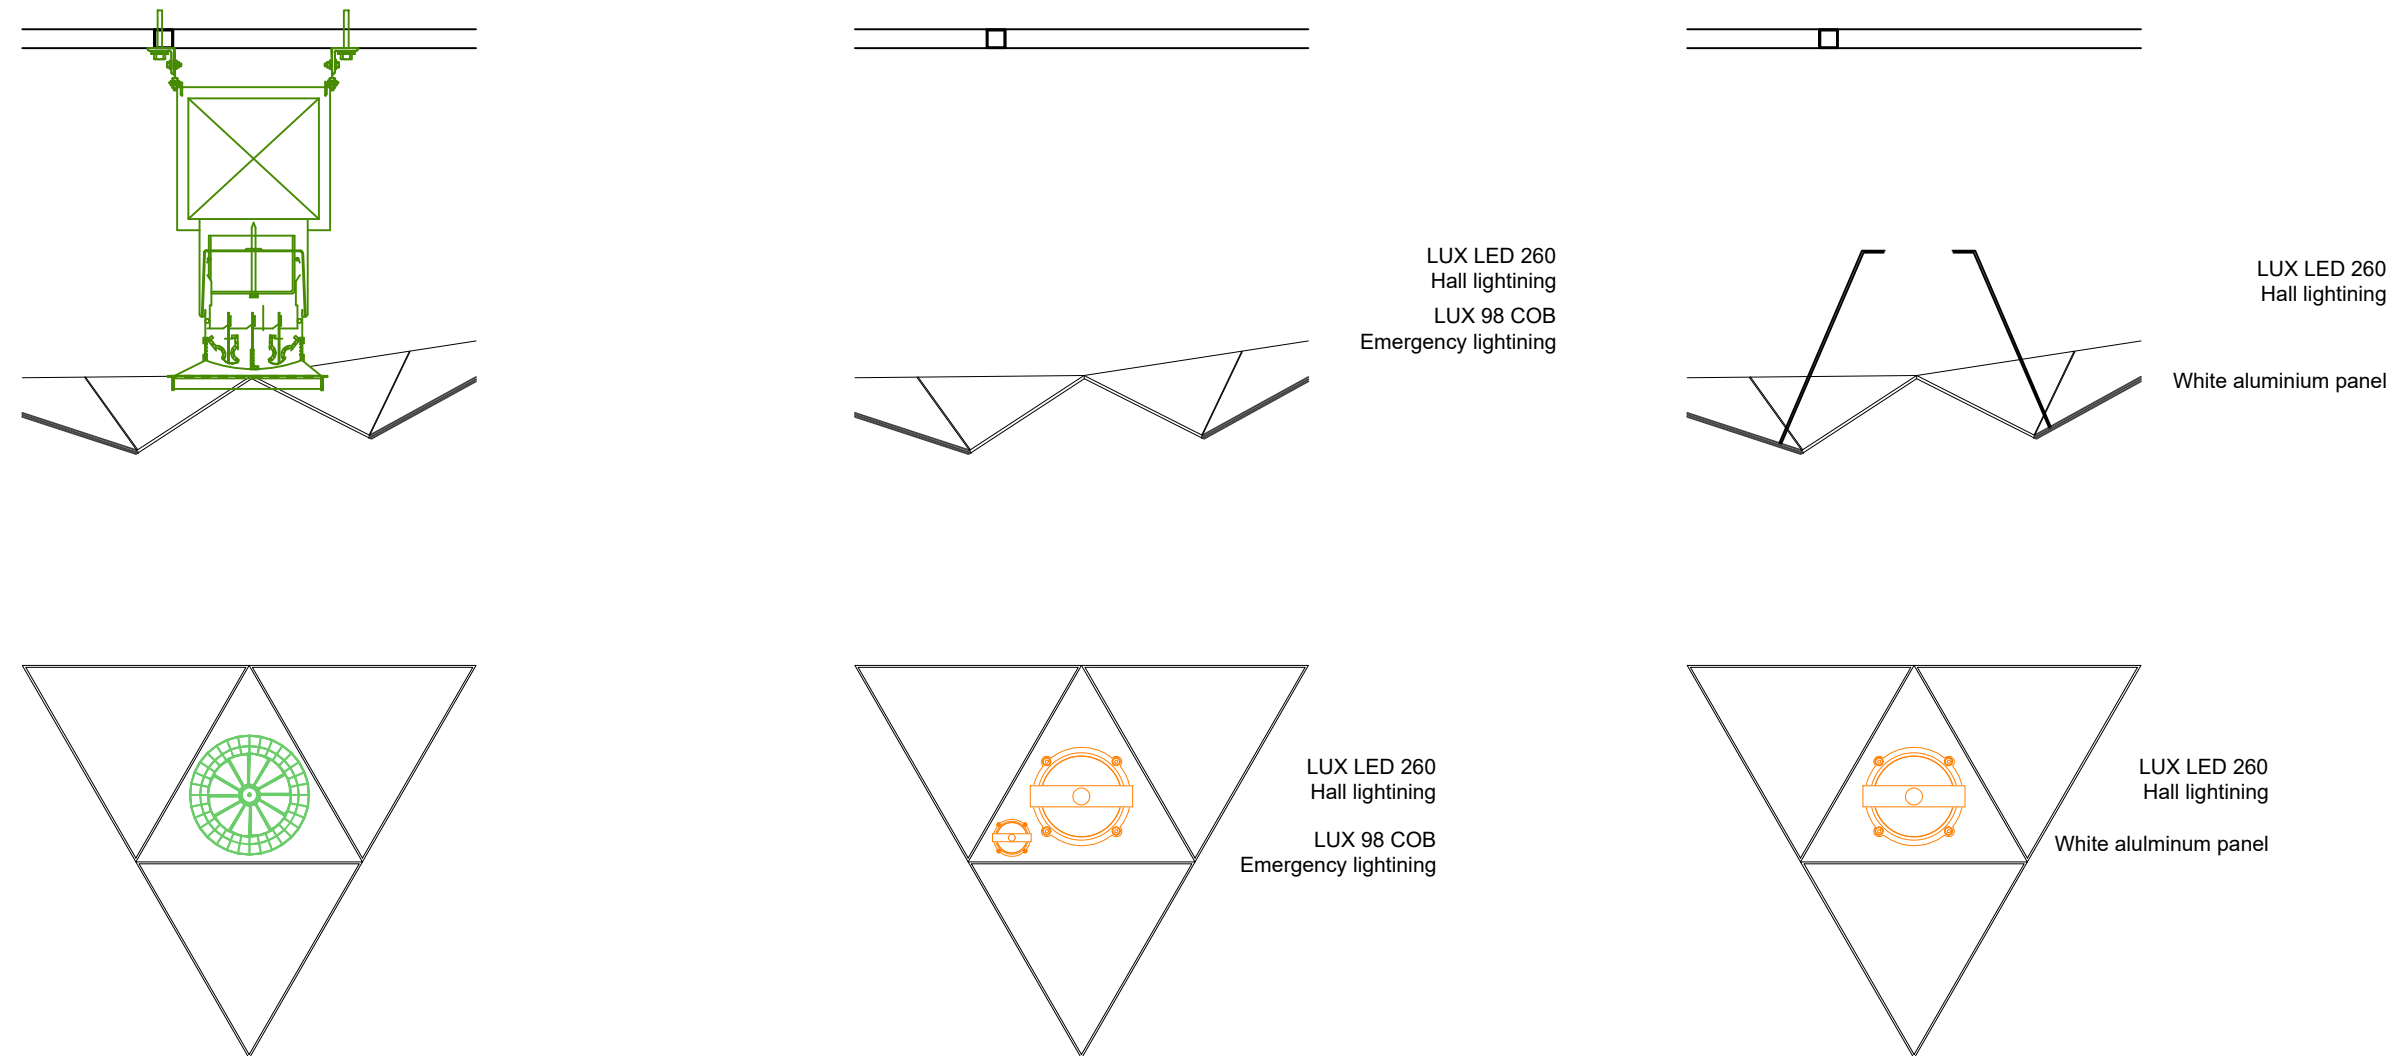

7 Ceiling Elements - Section

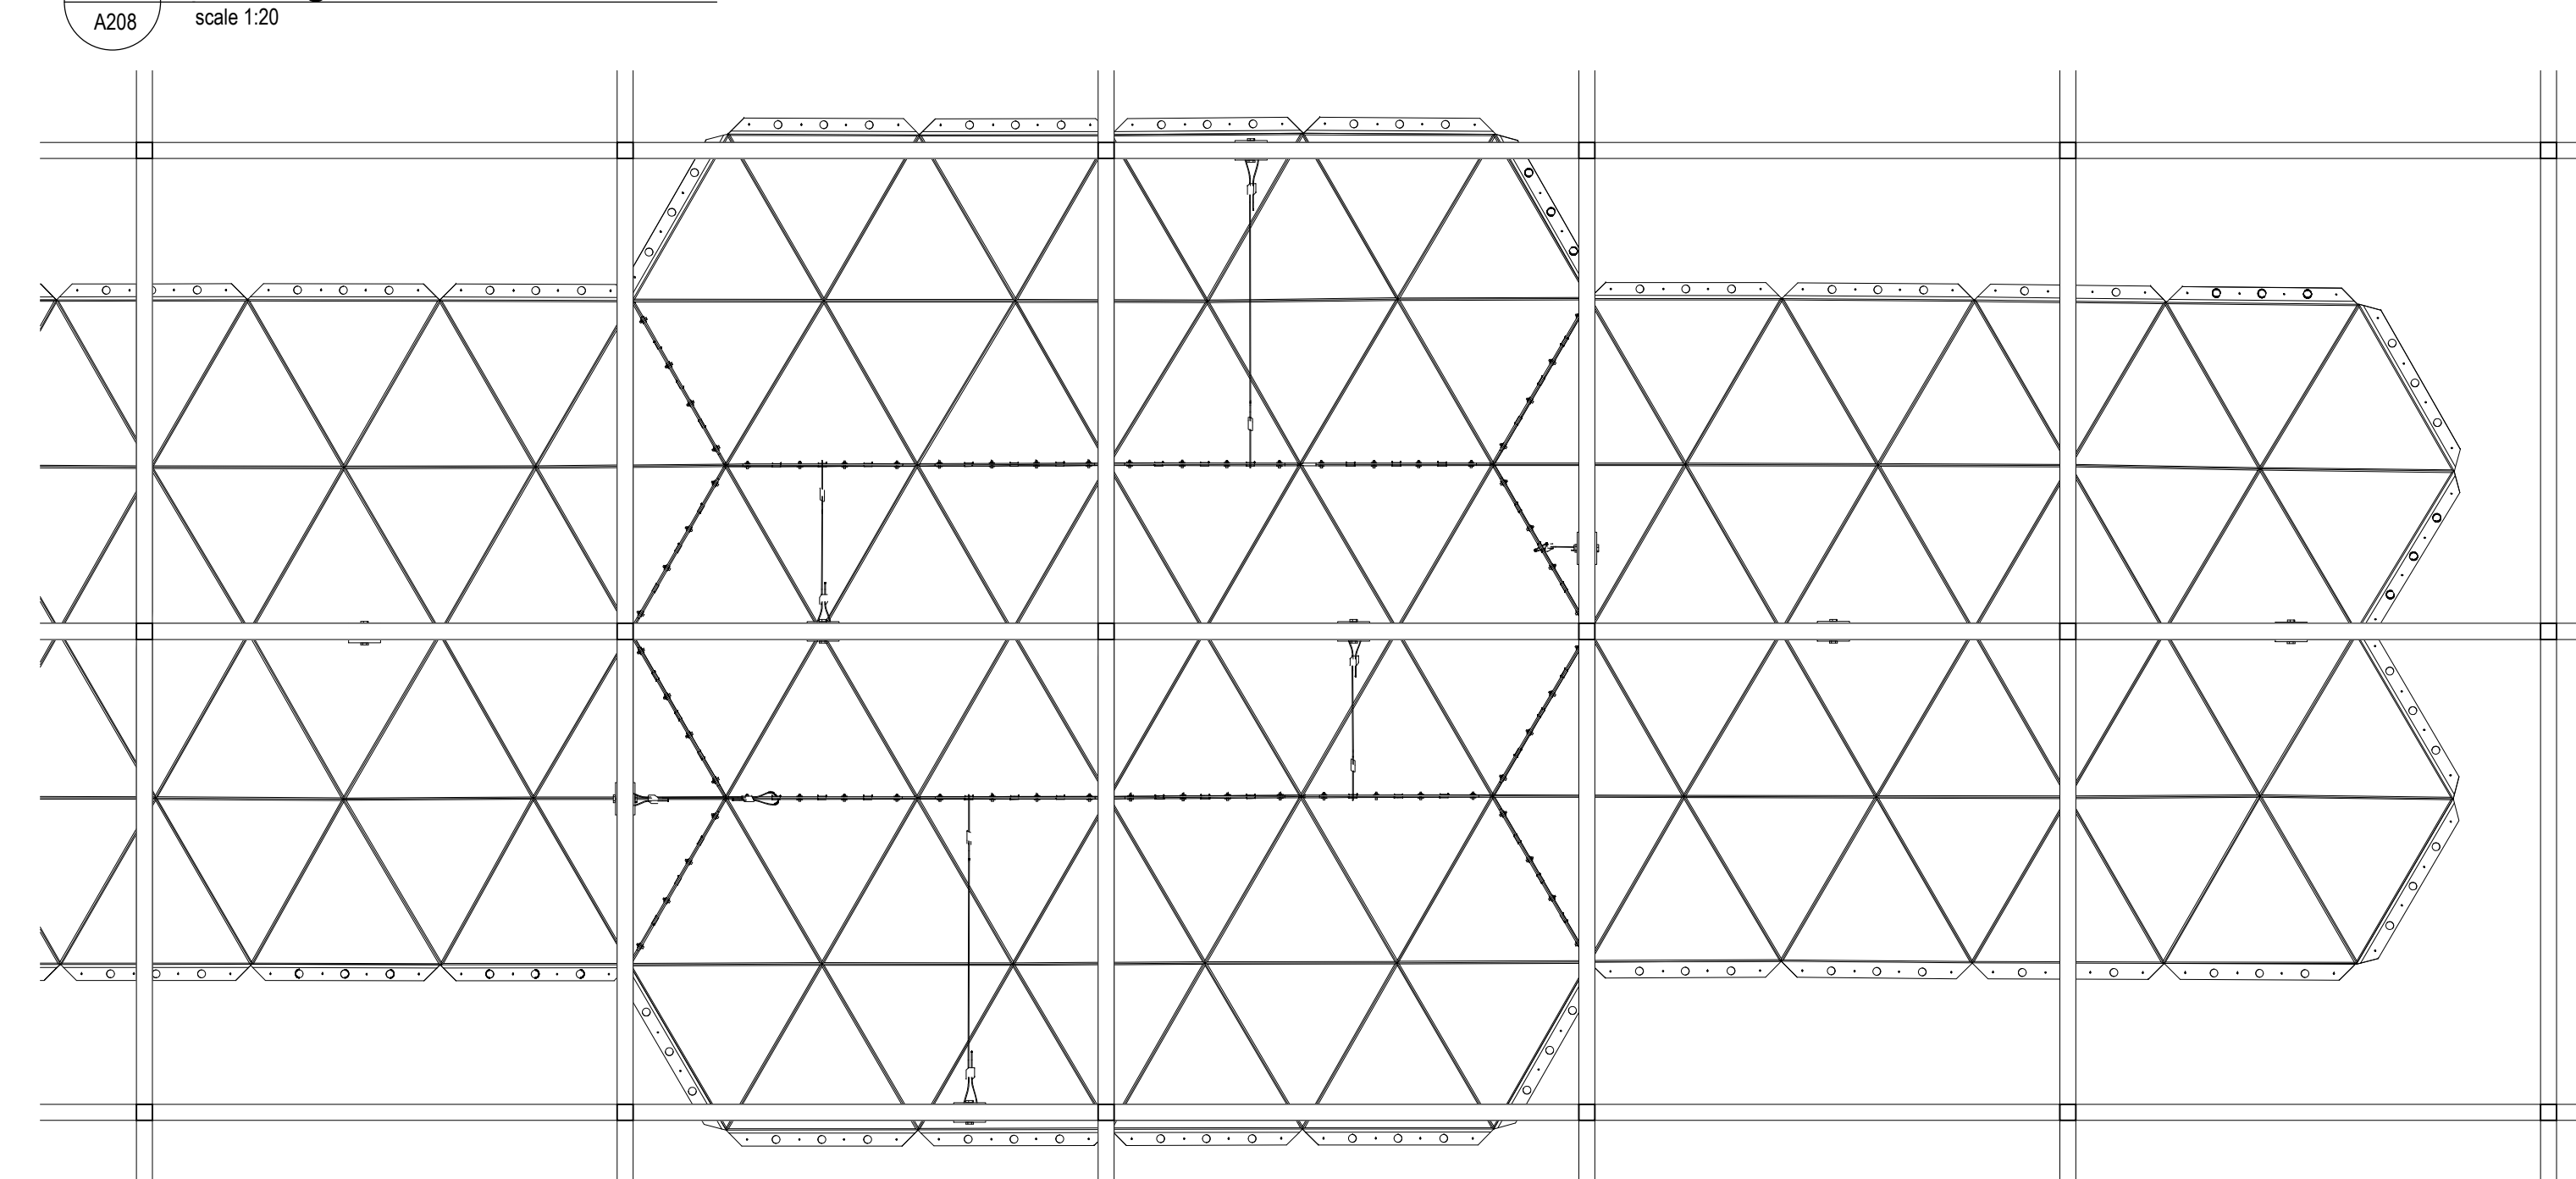

10 Ceiling Elements - Assembling

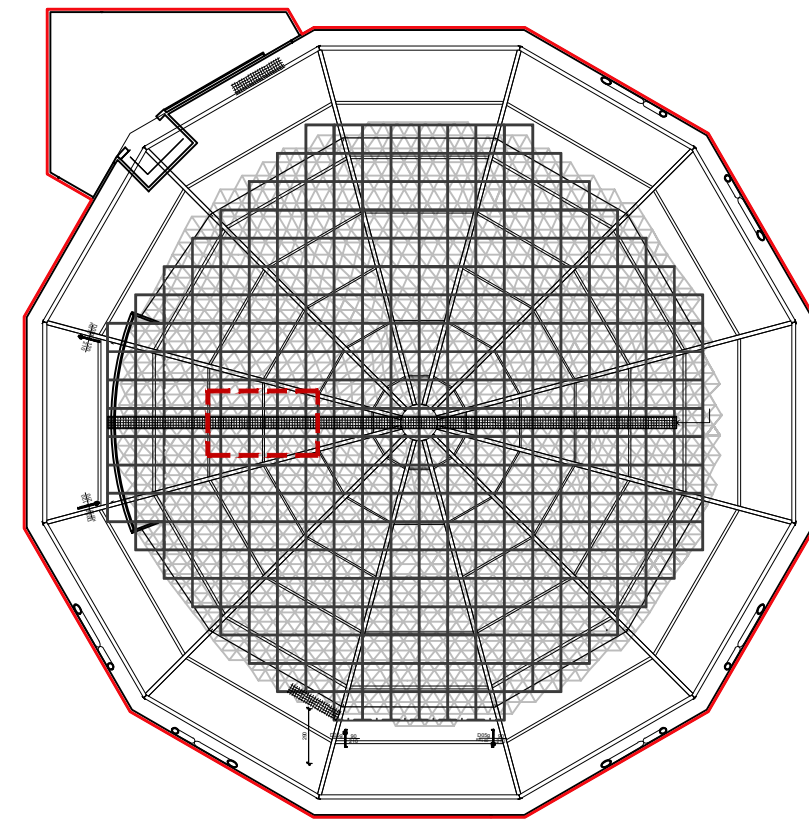

KEYPLAN LOWER LEVEL

LEGEND

PROJECT AREA			
LEGEND: WALL AND FLOORING LIGHTS			
Flexible light strip LED Array High Performances 29W 3402 lm 3000K CRI 80	data-sheet LT 01	Desk lamp - SNAKE LED LED 1 x 1,0m	data-sheet LT 14
Surface light - REGLETTE LED LED 1000lm/m	data-sheet LT 06	Desk lamp LED 21W/m CRI 90	data-sheet LT 17
Wall lamp Top LED 1,2W 105 lm 3000K CRI 90	data-sheet LT 09	Note: Motion sensor in all bathrooms Note: For a better specification please refer to the related engineering drawings	

LEGEND: CEILING LIGHTS			
Lights must be checked to guarantee high quality broadcasting			
Flexible light strip LED Array High Performances 29W 3402 lm 3000K CRI 80	data-sheet LT 01	Ceiling lamp - Fixed Trim Dimmable Power LED 10W 910 lm 3000K CRI 90	data-sheet LT 12
Recessed light - DIMMABLE LED Array High Performances 29W 3402 lm 3000K CRI 80	data-sheet LT 02	Emergency ceiling lamp VERSO LED VSD	data-sheet LT 13
Recessed light Ø80 LED Array DC 500 mA 9,2W 810 lm 3000K CRI 90	data-sheet LT 03	Projector Sagomare, LED, 450W, CW zoom 08°-19°, 5600K, controllo DMX	data-sheet LT 15
Recessed light Top LED 34,1W/m 3915 lm/m 3000K CRI	data-sheet LT 04	Emergency ceiling lamp	data-sheet LT 16
Projector 1 x 48 TOP LED 3000K 2110lm total CRI80 - 2x10W	data-sheet LT 05	Projector Sagomare, LED, 450W, CW zoom 08°, 3000K, controllo DMX	data-sheet LT 18
Surface light - REGLETTE LED LED 1000lm/m	data-sheet LT 06	KEEP EXISTING LIGHTING	
CEILING OPENING FOR LUX LED - closed niches - no.100 (see detail layout no. 207)		CEILING OPENING FOR LUX LED - open niches to be used also as void for air return - no. 100 (see detail layout no. 207)	
Note: Motion sensor in all bathrooms Note: For a better specification please refer to the related engineering drawings			

LEGEND: THERMIC AND AIR SYSTEM			
AIR DIFFUSER (dome)	HORIZONTAL GRID AIR RETURN	VERTICAL GRID AIR RETURN	
CEILING OPENING FOR AIR DIFFUSER no. 48	HORIZONTAL GRID AIR SUPPLY	VERTICAL GRID AIR SUPPLY	
NATURAL VENTILATION GRID	GRILLES FOR EXPELLING EXHAUSTED AIR	FLOORING AIR SUPPLY (office)	
SPLIT SYSTEM AIR CONDITIONER (internal and external unit)	EXTERNAL AIR CONDENSER	Note: For a better specification please refer to the related engineering drawings	

NOTE:
FOR FURTHER DETAIL ABOUT WOODSKIN REFERE TO THE TECHNICAL ATTACHED TO THE DATASHEET

GENERAL NOTES:
A. DO NOT SCALE THE DRAWINGS. ANY DISCREPANCIES FOUND SHOULD BE REPORTED TO THE RESPONSIBLE ARCHITECT OR ENGINEER IMMEDIATELY.
B. ALL MEASUREMENT MUST BE VERIFIED AND CONFIRMED AT CONSTRUCTION SITE.
C. ALL WORKS ARE TO BE CARRIED OUT TO LOCAL CODES OF CONSTRUCTIONS.
D. ALL MATERIAL FINISHES AND WORKMANSHIP SHOULD BE OF HIGH STANDARD QUALITY OF WORKS.
E. IN CASE OF NON-CONFORMITY ALL INFORMATION REGARDING THE ARCHITECTURE HAS TO BE TAKEN OUT OF THE ARCHITECTURAL DRAWINGS AND ALL THE MECHANICAL AND ELECTRICAL INSTRUCTIONS OUT OF MEP DRAWINGS.
F. THIS DRAWINGS SHOULD BE READ IN CONJUNCTION WITH THE OTHER RELEVANT ARCHITECTURAL, STRUCTURAL, MECHANICAL AND ELECTRICAL DRAWINGS AND ALL RELEVANT SECTIONS OF THE SPECIFICATIONS.
G. EXACT LOCATION, SIZES AND DETAILS OF ELECTRO-MECHANICAL WALL OPENINGS SHALL BE COORDINATED WITH ELECTRO-MECHANICAL ENGINEERS.
H. DIMENSION AND LOCATION OF SERVICES SHALL BE COORDINATED WITH RESPECTIVE ARCHITECTURAL AND SERVICES DRAWINGS PRIOR TO COMMENCEMENT OF ANY WORK. ANY DISCREPANCY FOUND SHOULD BE BROUGHT TO THE NOTICE OF THE CONCERNED ENGINEER.
I. IT IS THE RESPONSIBILITY OF THE CONTRACTOR OR BUILDERS TO ASCERTAIN AND CONFIRM THAT ALL DIMENSIONS SHOWN IN THESE DRAWINGS SHALL COMPLY WITH THE SITE DIMENSIONS AND LEVELS PRIOR TO PREPARING DRAWINGS AND EXECUTING THE WORKS.
L. ALL MATERIALS MUST BE VERIFIED AND CONFIRMED BY SITE ENGINEER ON SHOP DRAWINGS AND SAMPLES BY CONTRACTOR.
M. REFER TO SCHEDULE OF FINISHES FOR FLOORS, WALLS AND CEILINGS.
N. ALL TEXTURES AND COLORS SHOULD BE REFERRED TO SCHEDULE OF FINISHES AND HAVE APPROVAL OF SITE ENGINEER.

LEGEND:
O.O.S.W. = OUT OF SCOPE OF WORK
F.F.L. = FLOOR FINISHING LEVEL

Architect:
Peia Associati s.r.l.
Arch. Giampiero Peia

Engineering:
AI Engineering s.r.l.

Client:
QATAR MINISTRY OF FOREIGN AFFAIRS
Permanent Mission of the State of Qatar to the United Nations Office in Geneva

Project:
RENOVATION AND FURNISHING OF CONFERENCE ROOM XIX AT THE UNOG GENEVA- SWITZERLAND

Project Phase:
DETAIL PHASE

Drawing Subject:
Detail - Dome Wood Skin

Designed:
Peia Associati

Draft:
PB

Checked:
GP

Review:
01

Date:
13/04/2018

Scale:
1:20/1:50/A1 Sheet

ID Dwg:
GE_DET_WS

Sheet No.:
A208

GE_DET_WS_Reboot.dwg

COPYRIGHT LAW RULES THE USE AND COPYING OF THIS DOCUMENT