




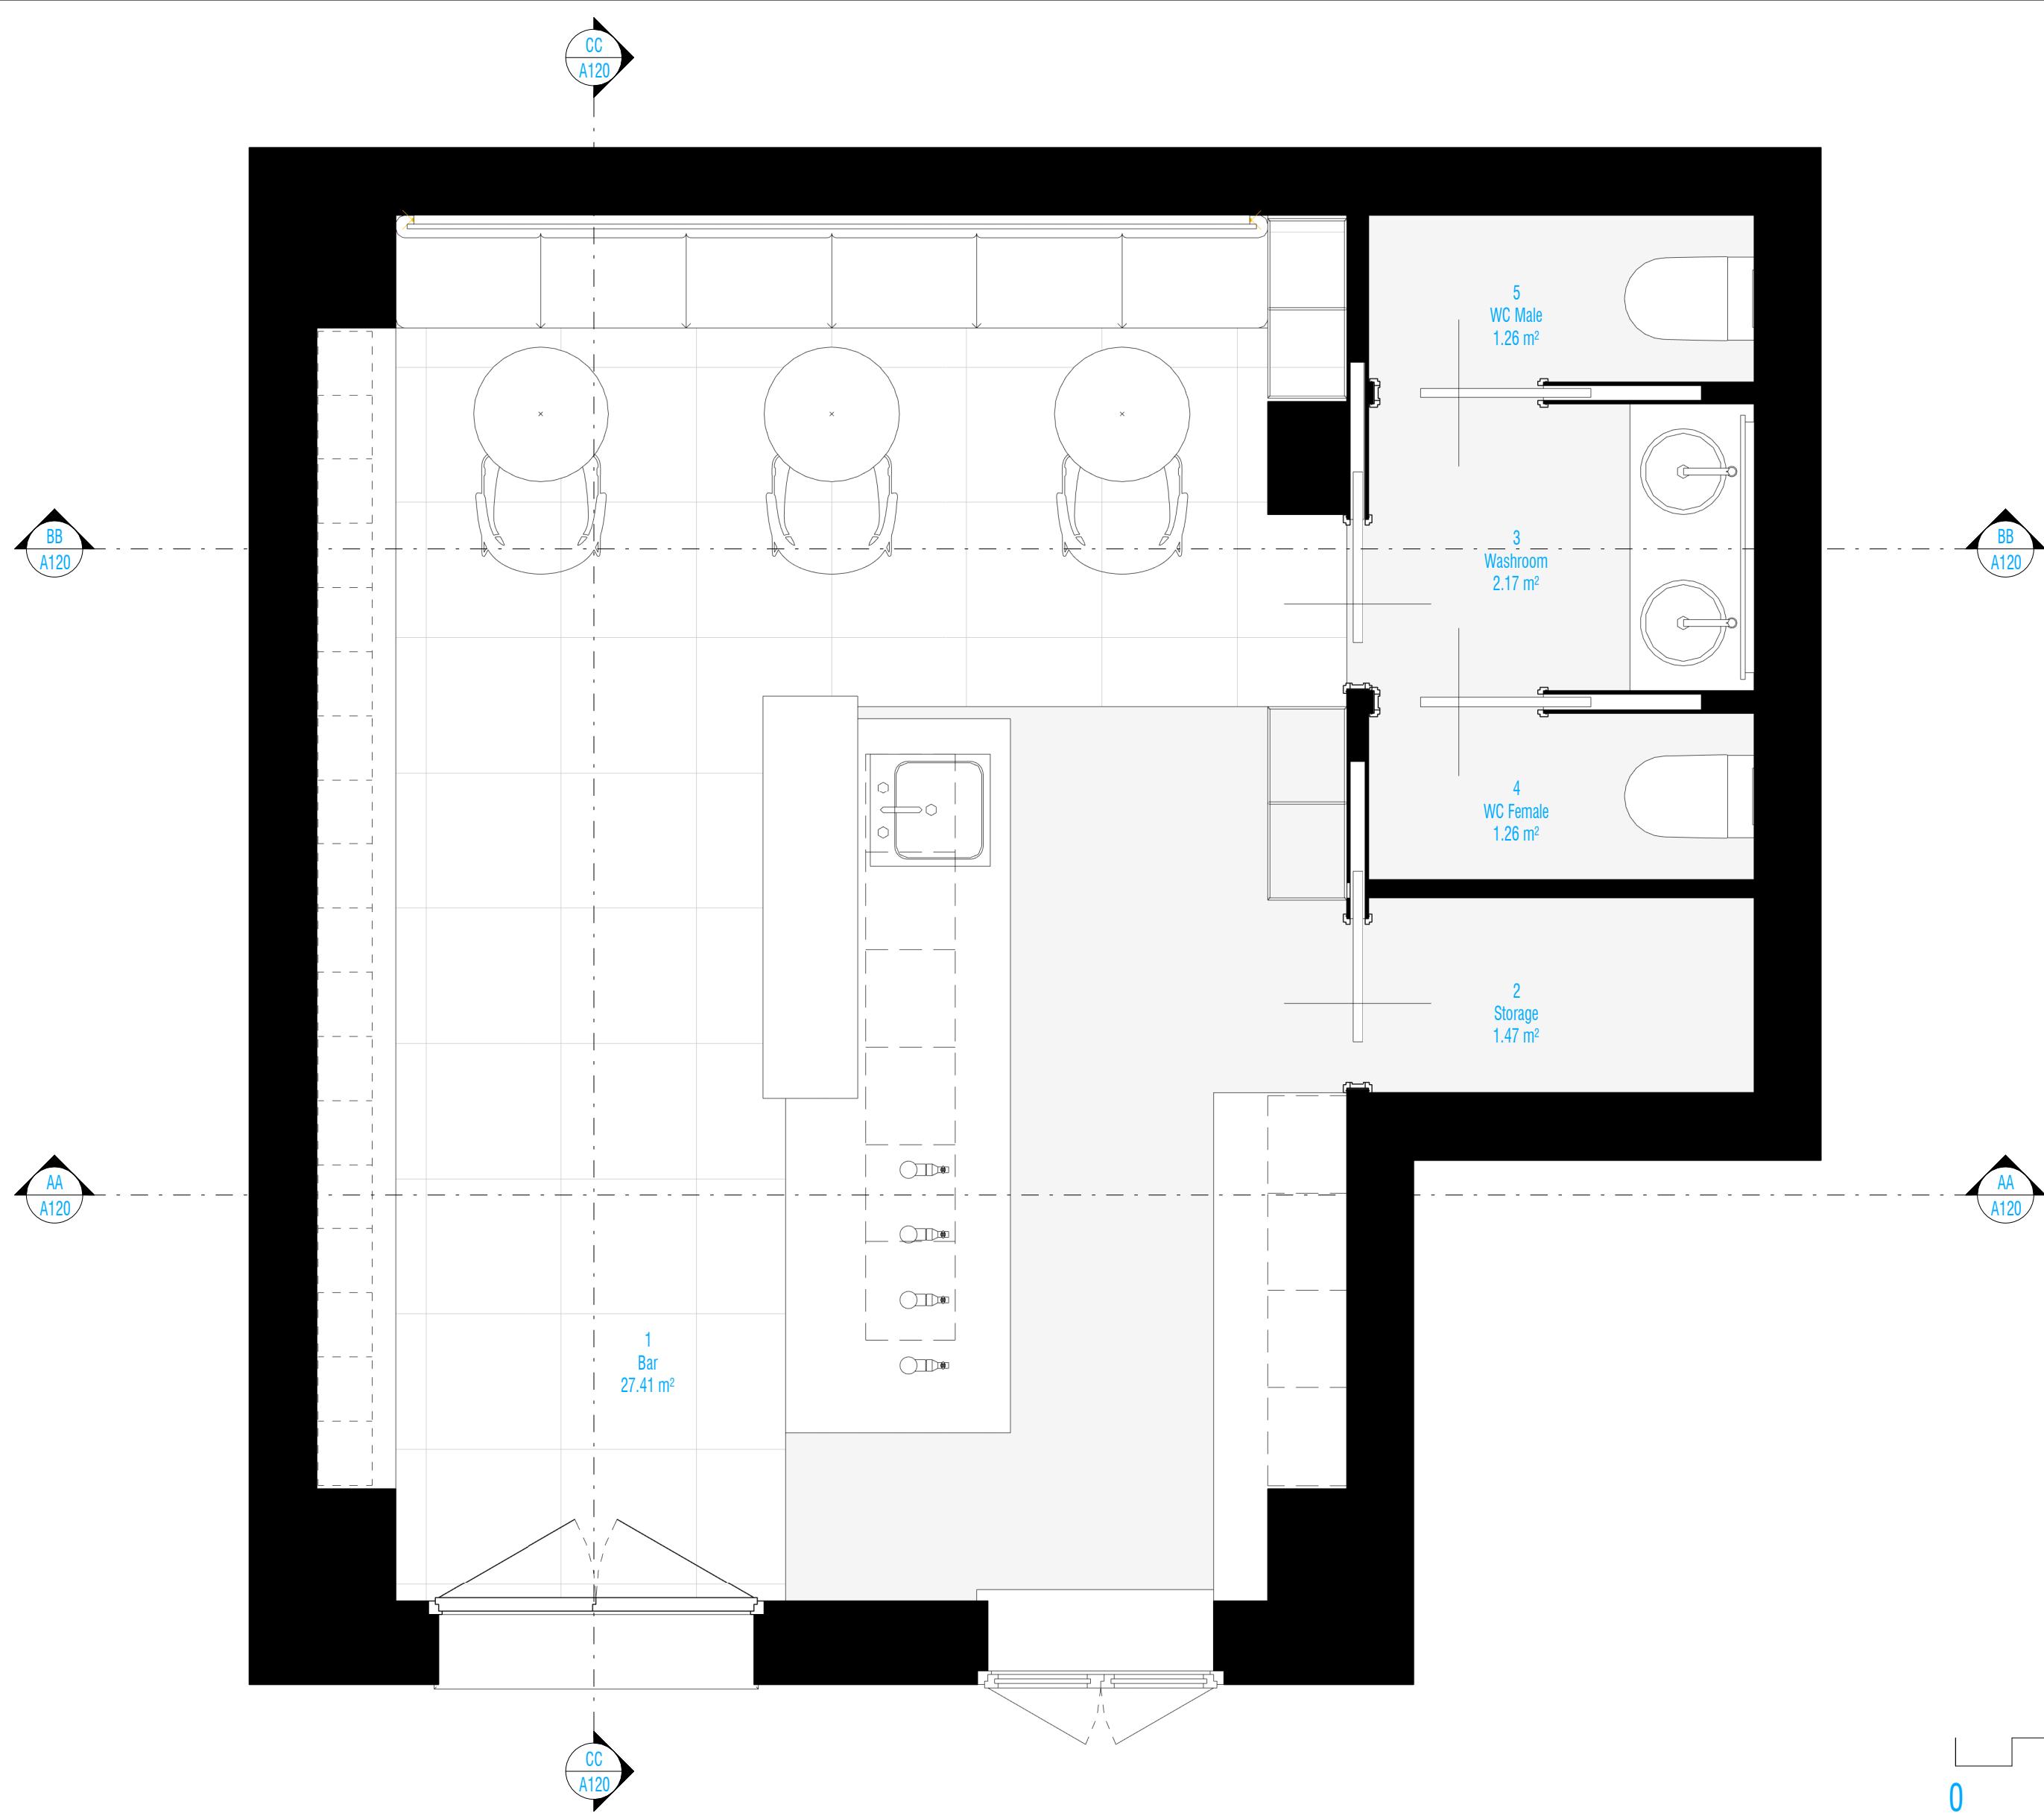

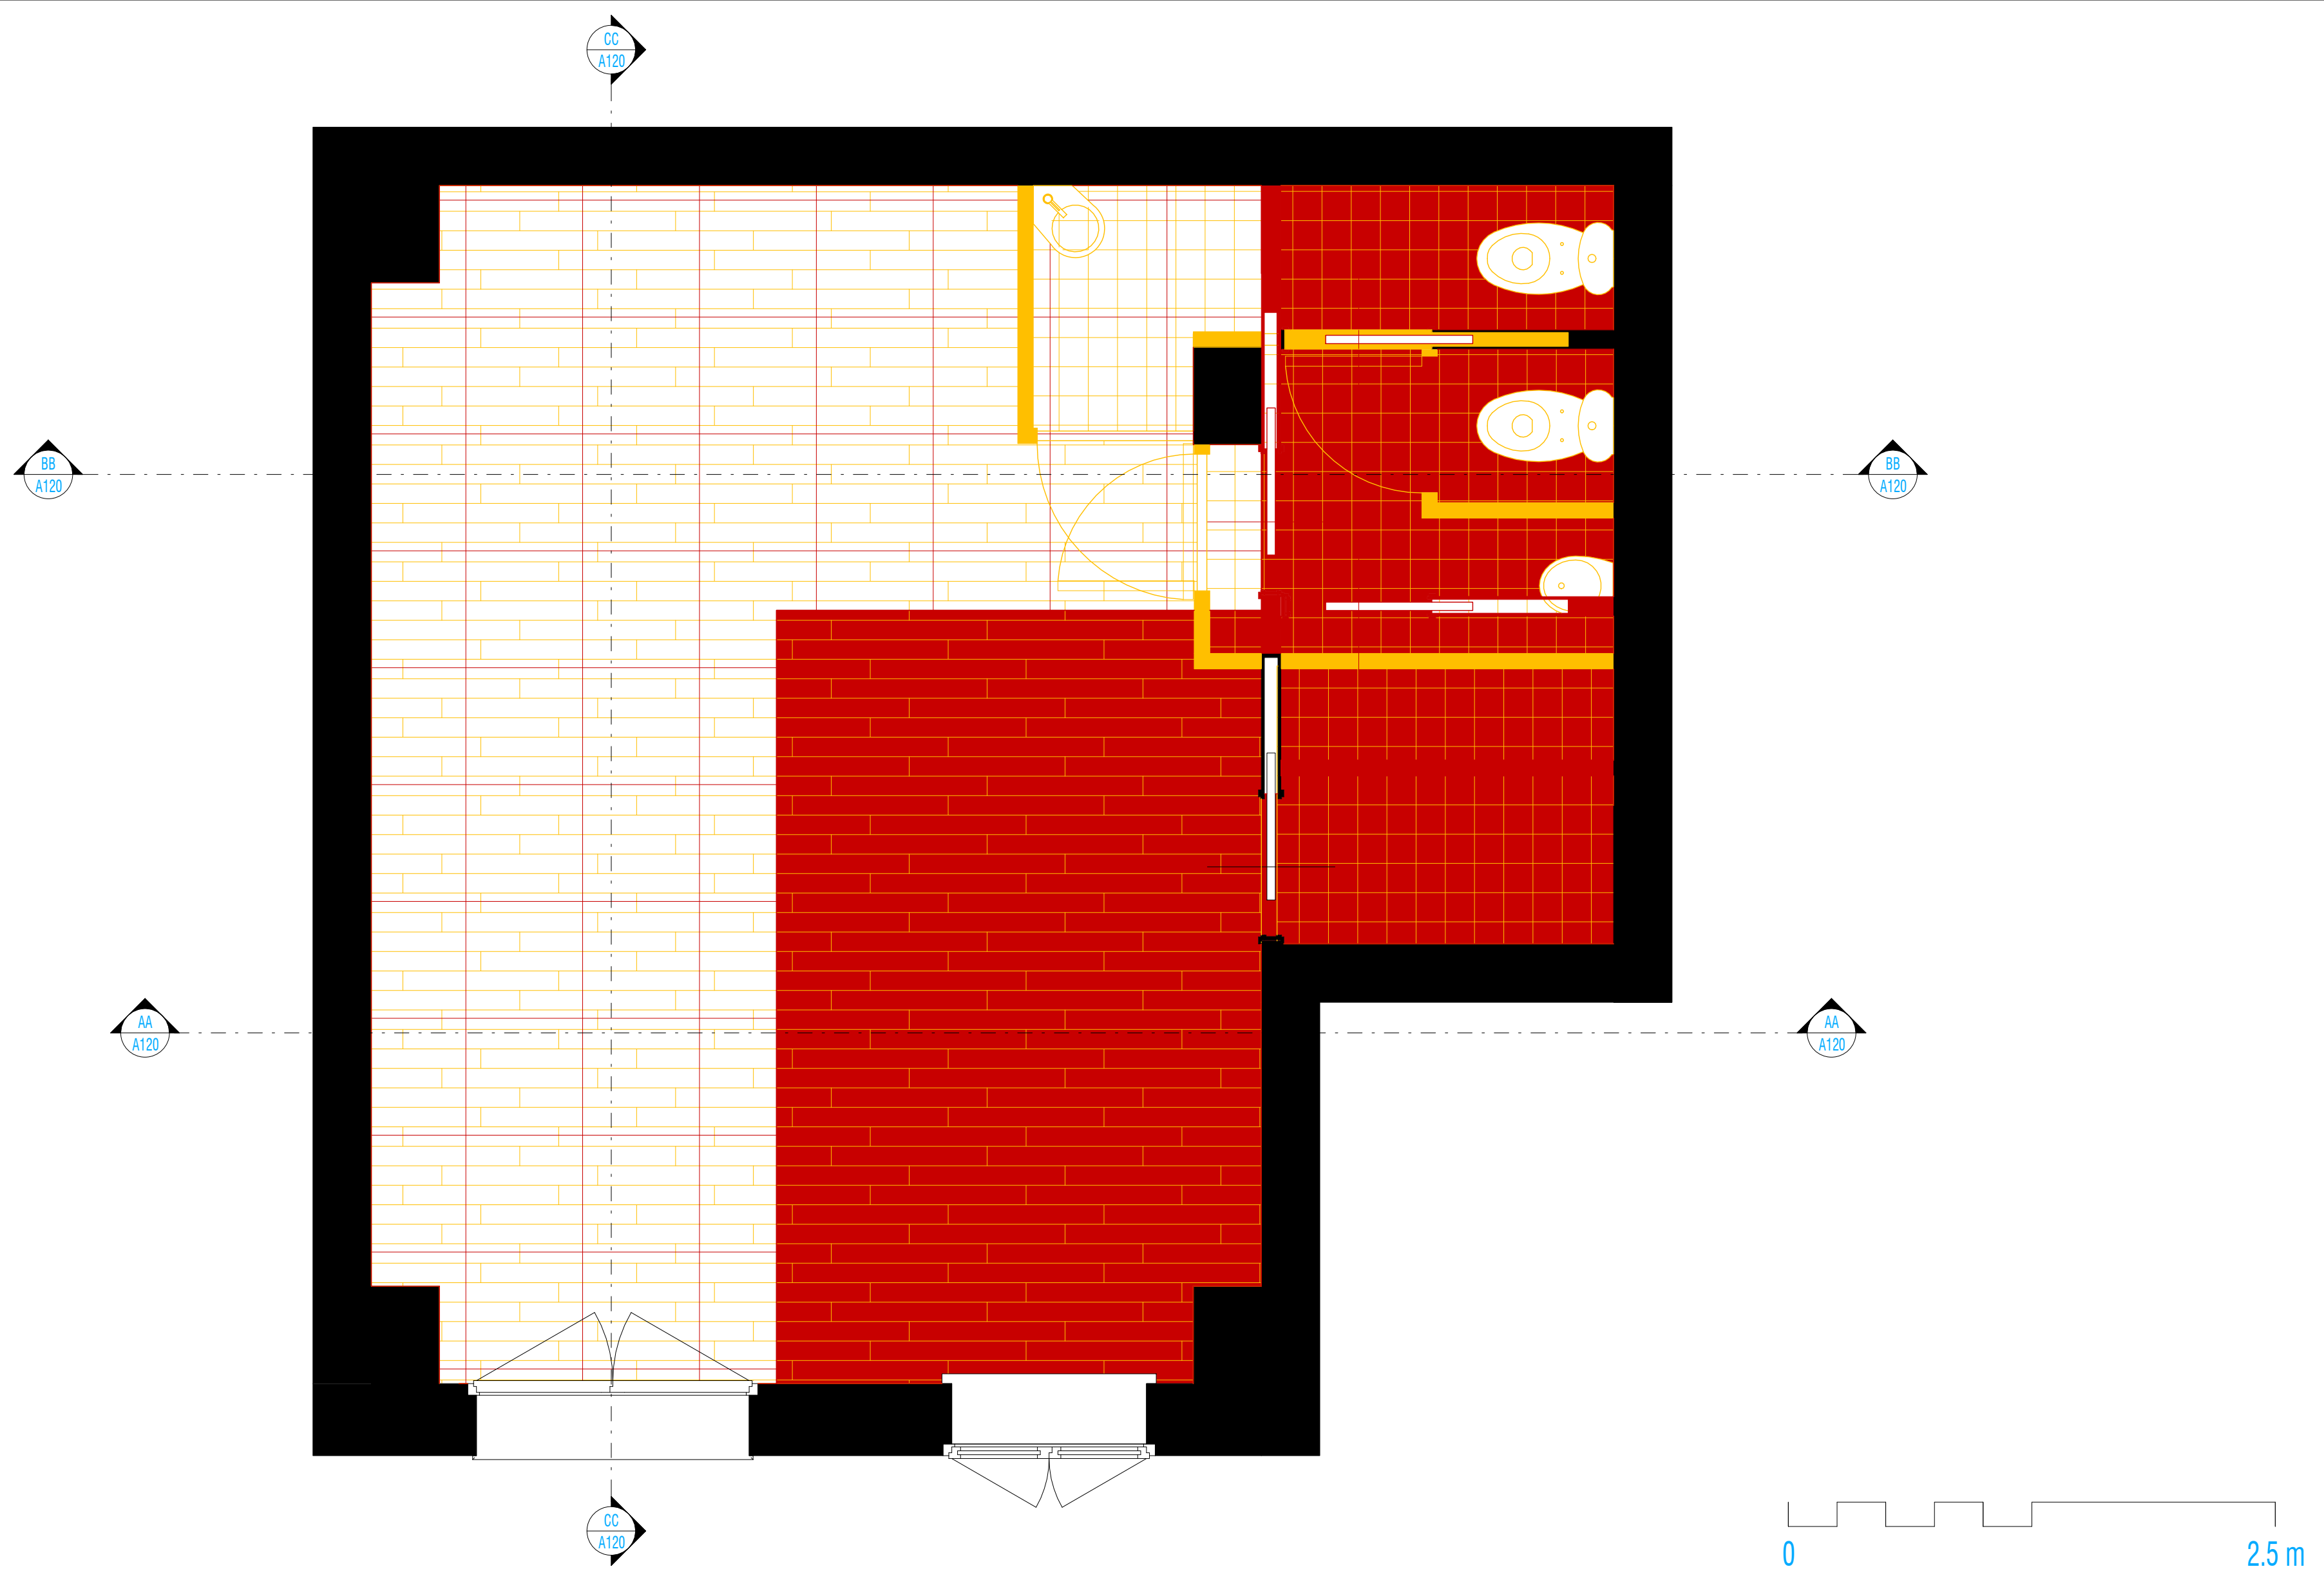

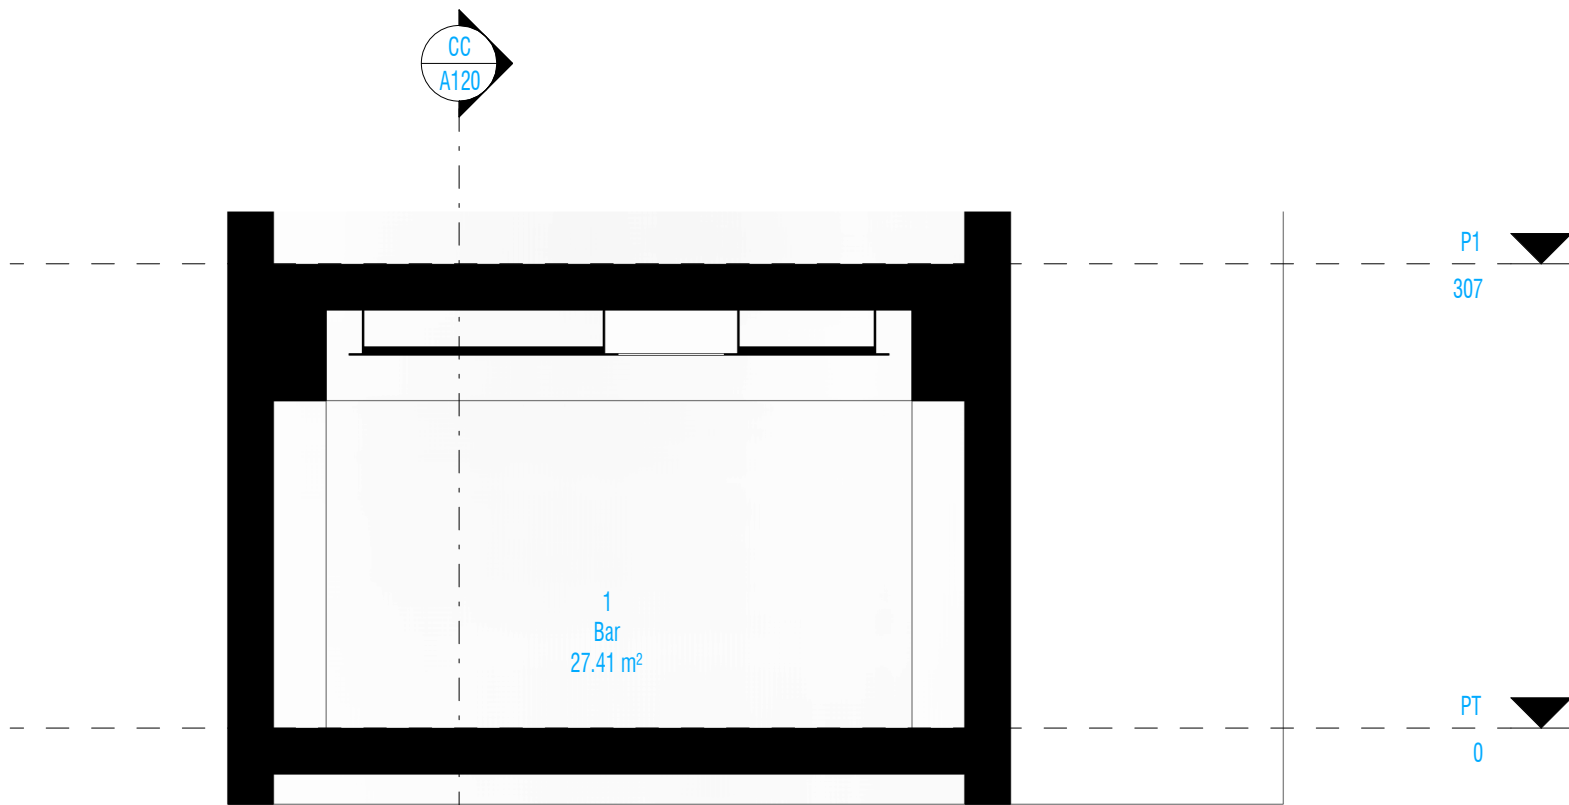







Section AA

1 : 50

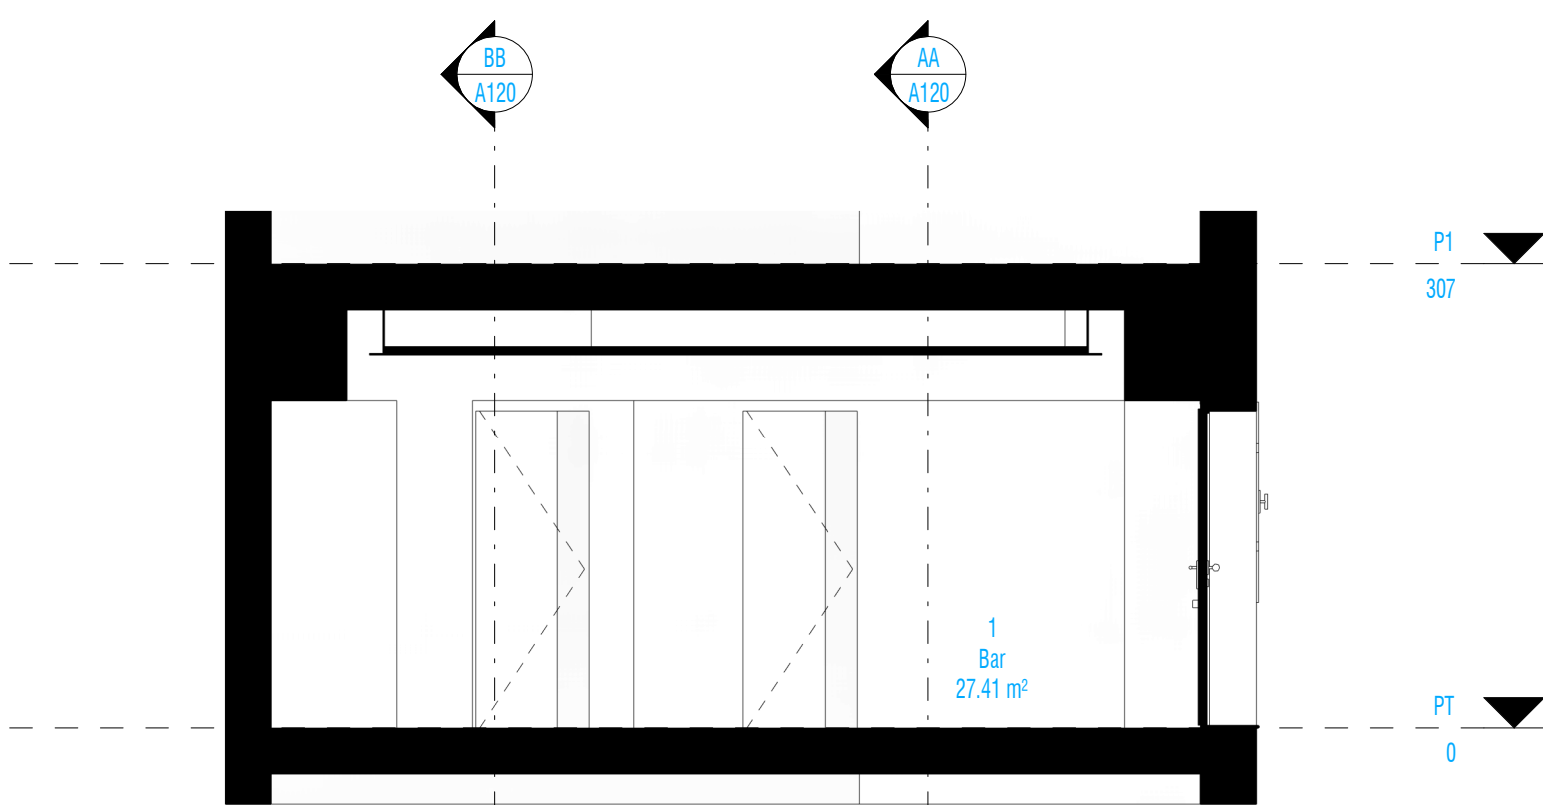


Section CC

1 : 50

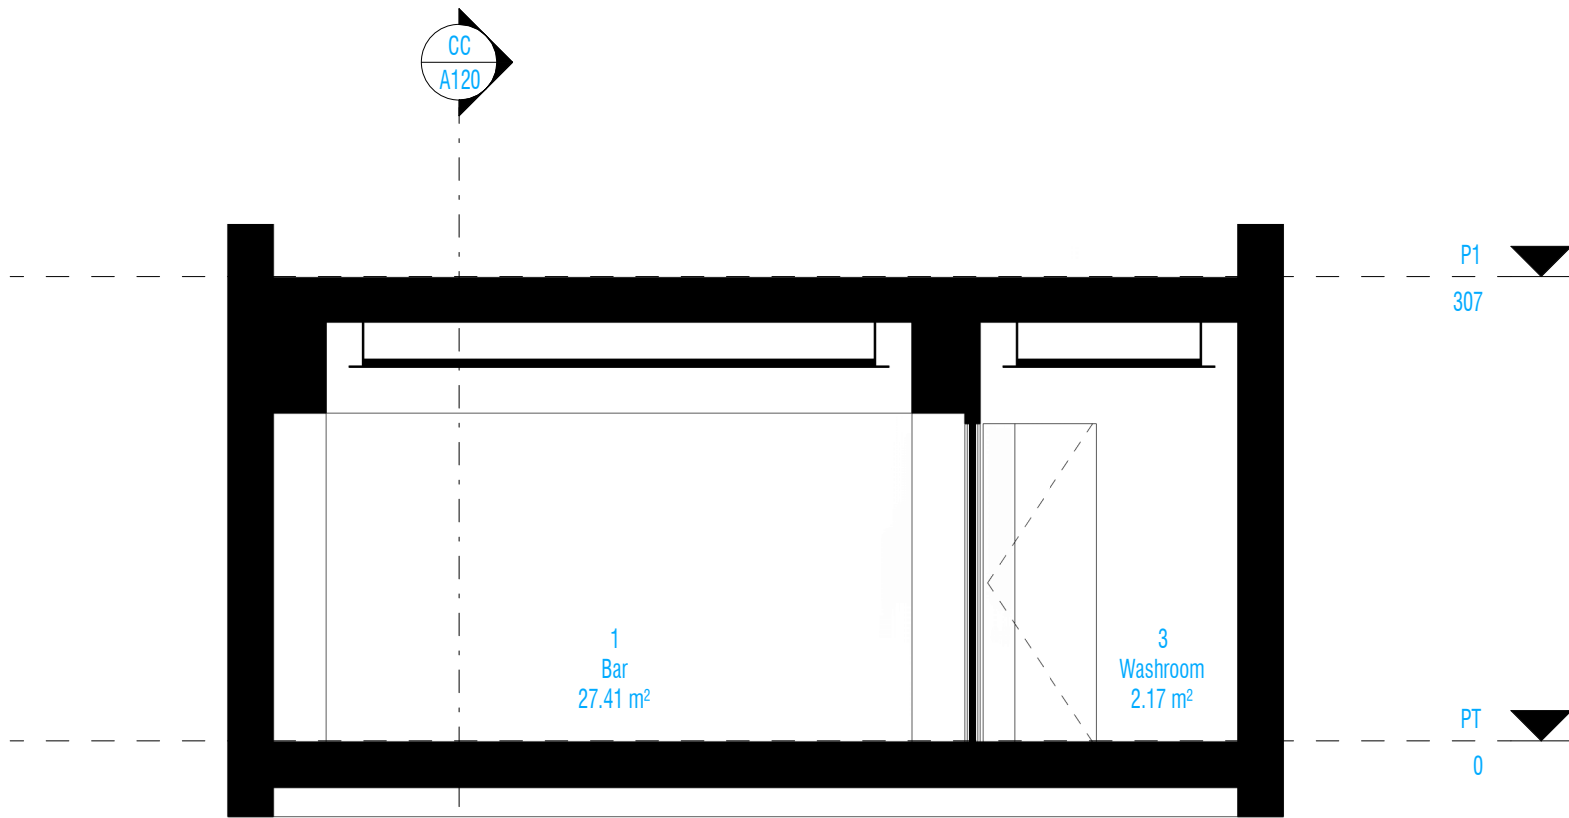



Section BB


1 : 50

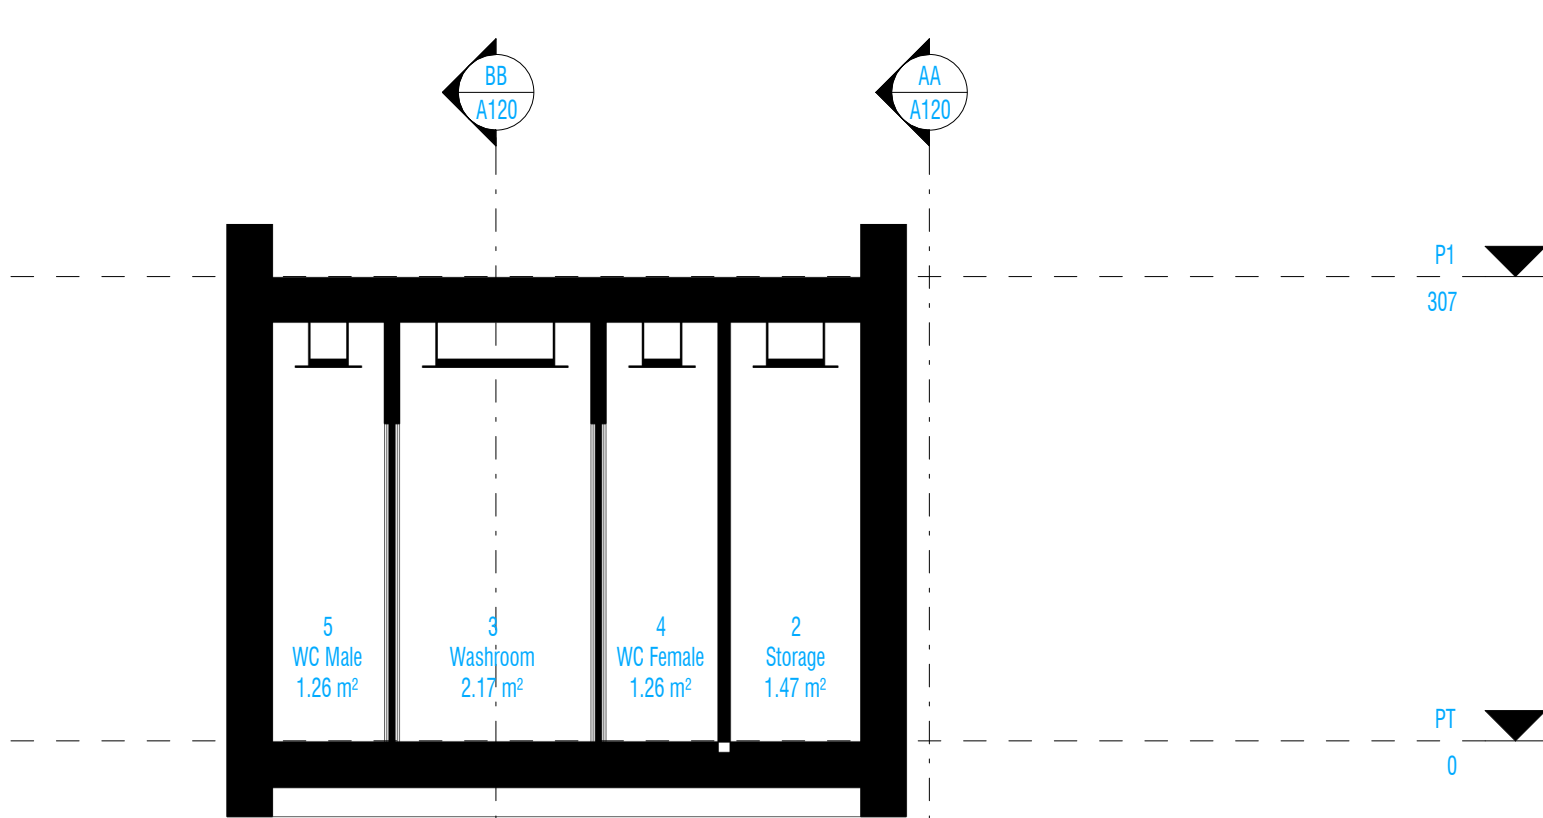

Section DD


1 : 50

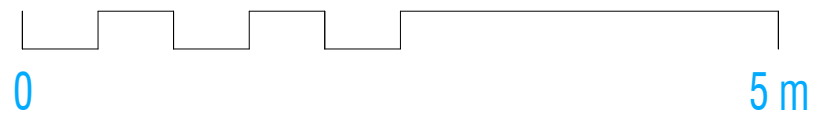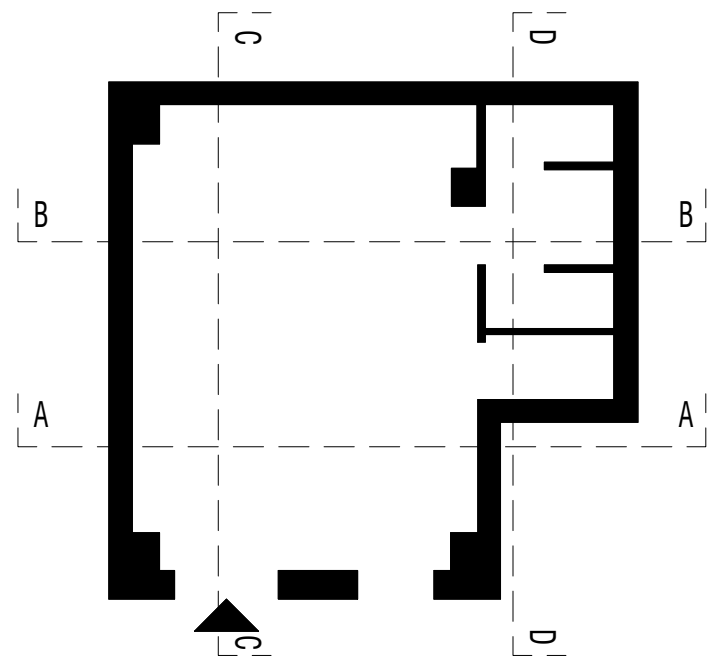

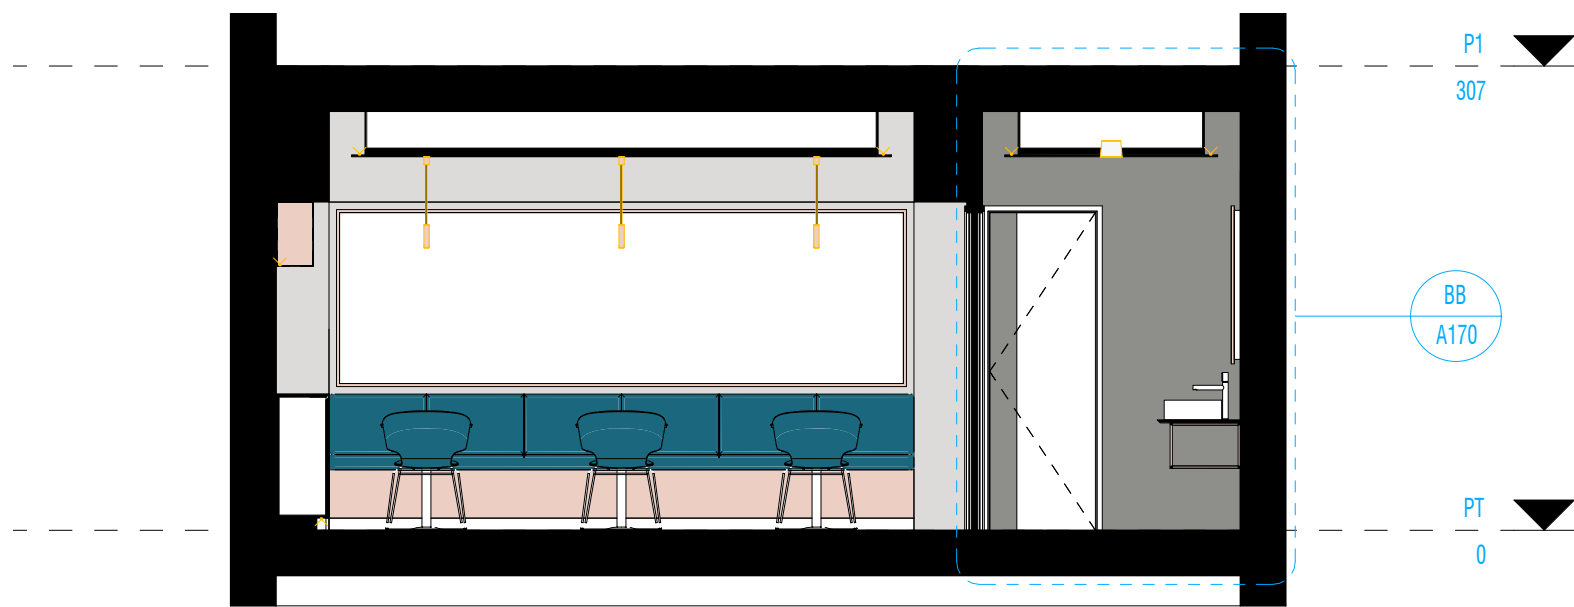


North Interior Elevation

1 : 50

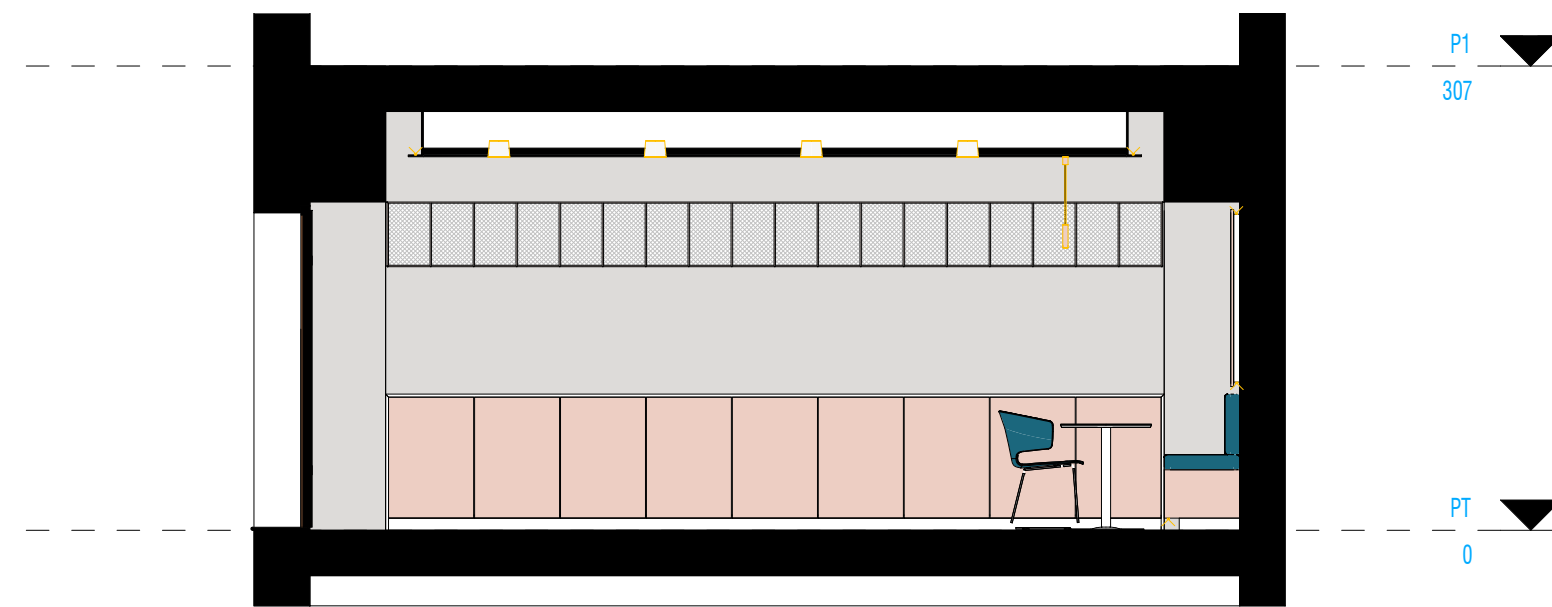


West Interior Elevation

1 : 50

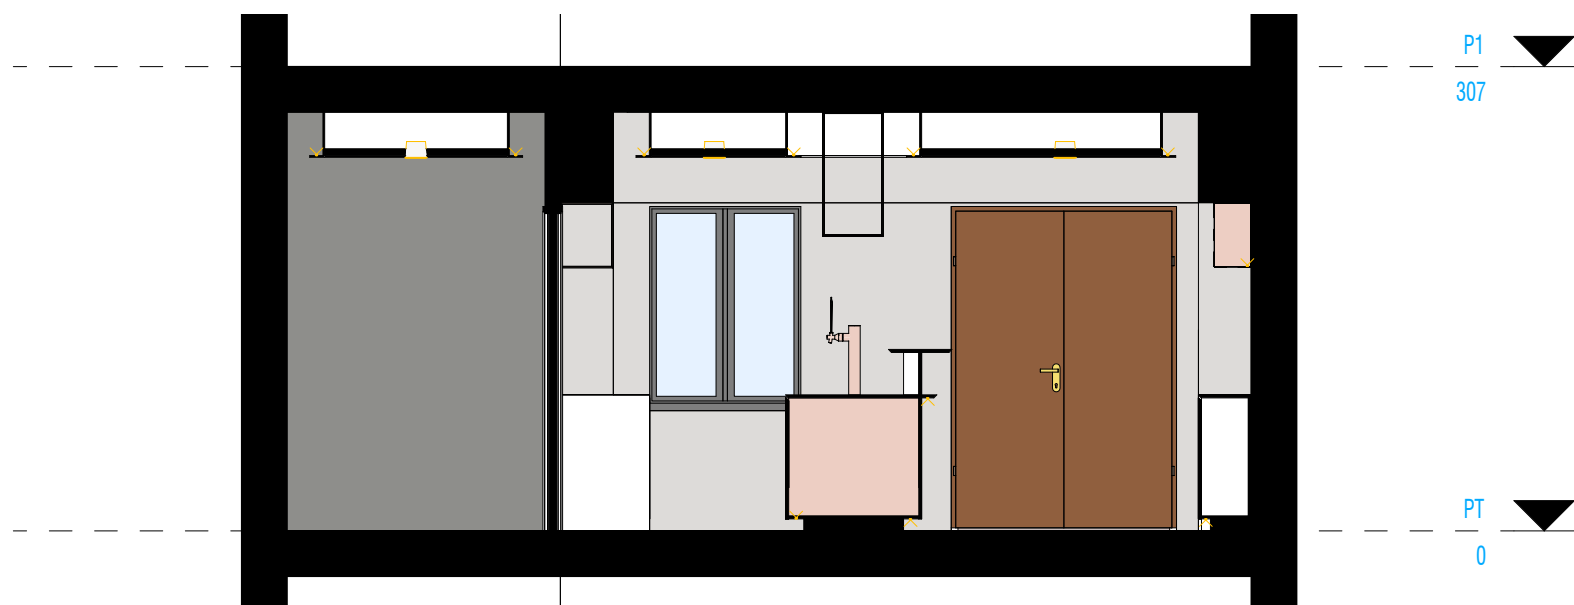



ARC_SDP_Int_Sud





1 : 50

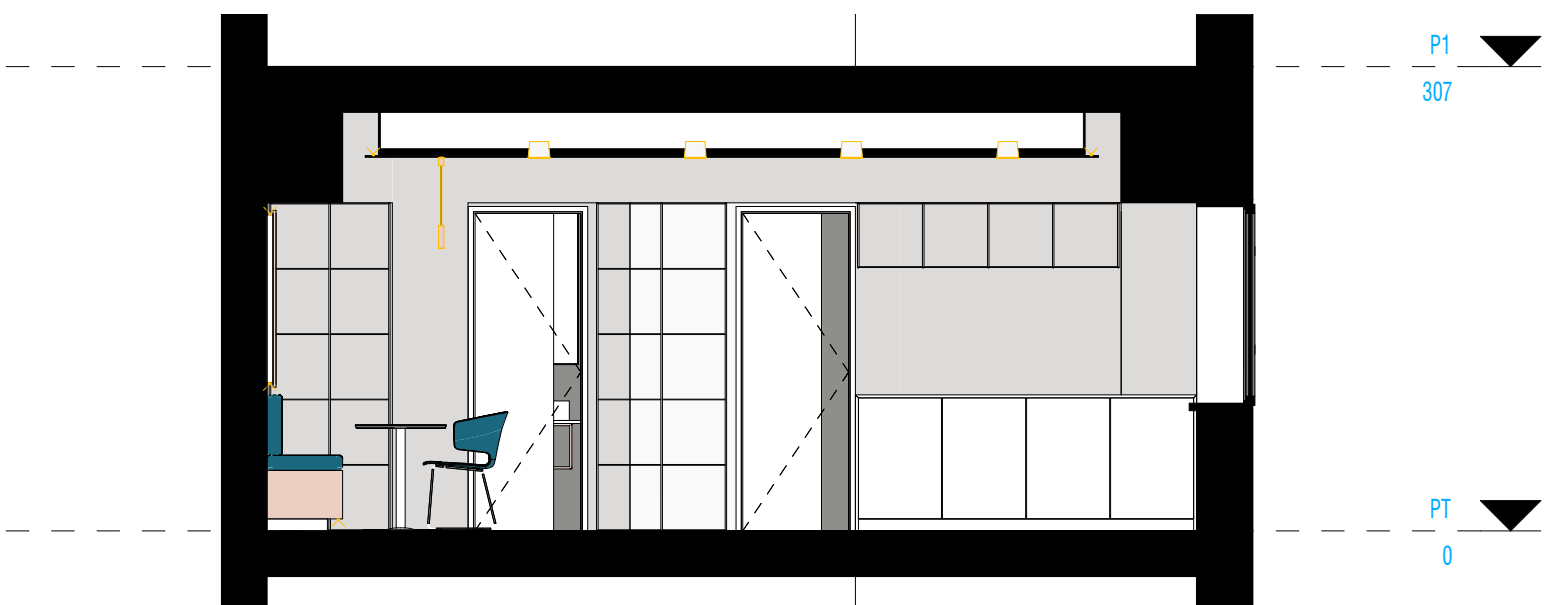


East Interior Elevation

1 : 50

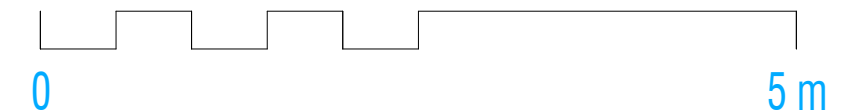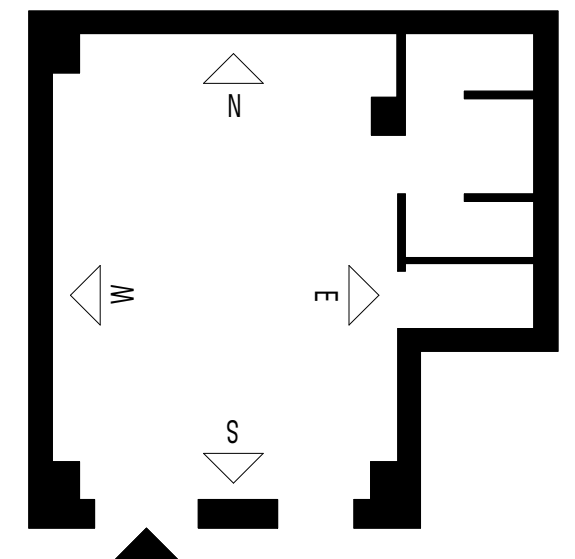

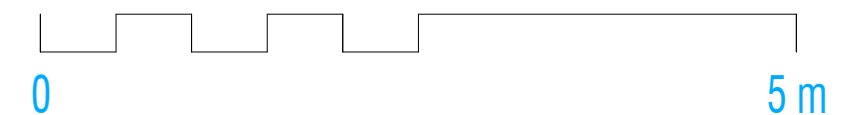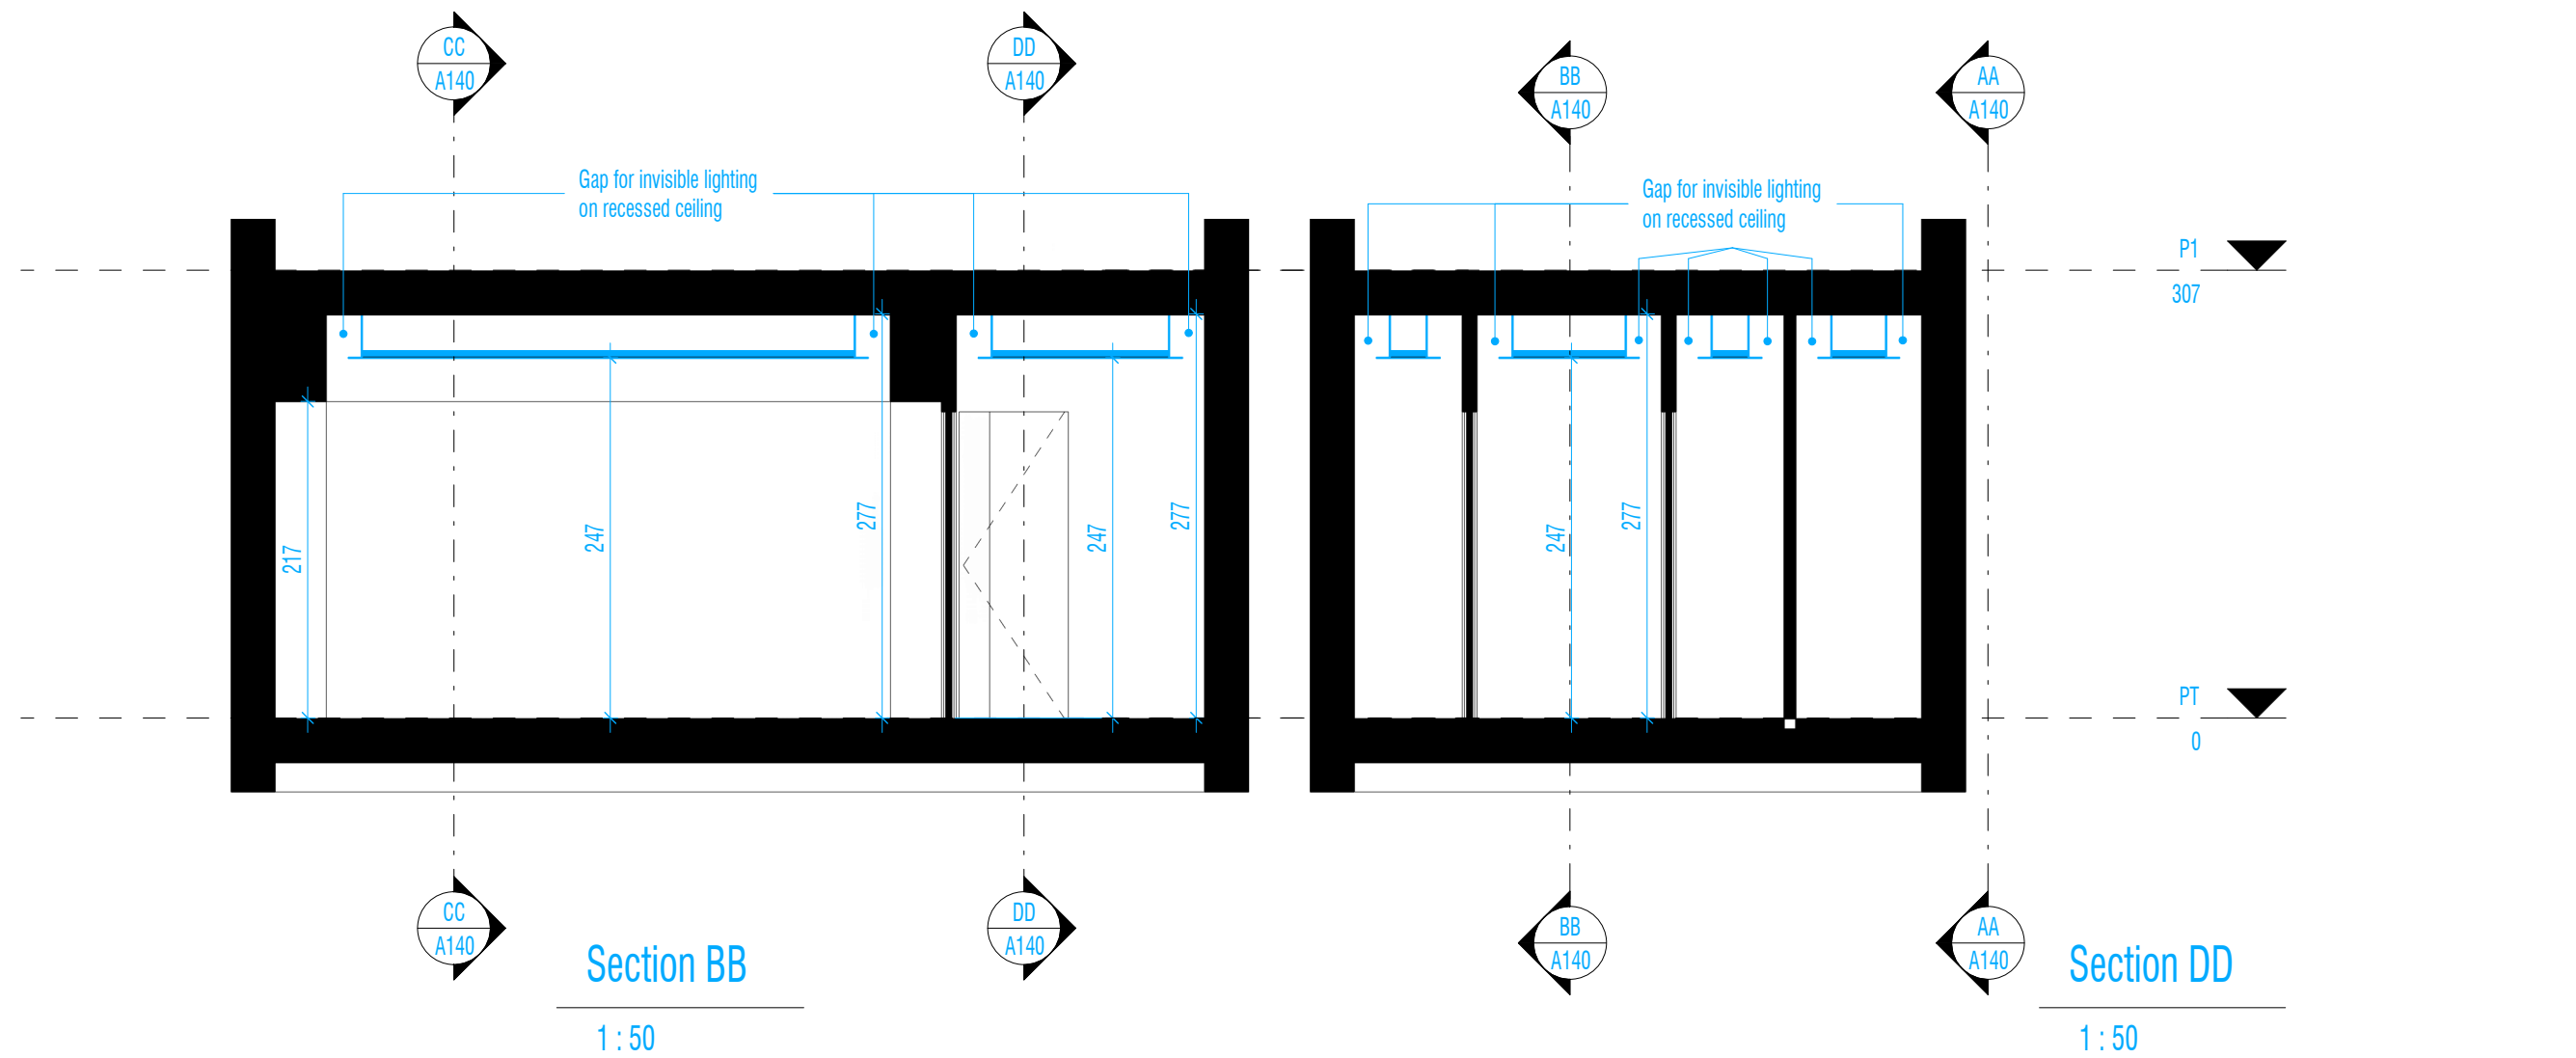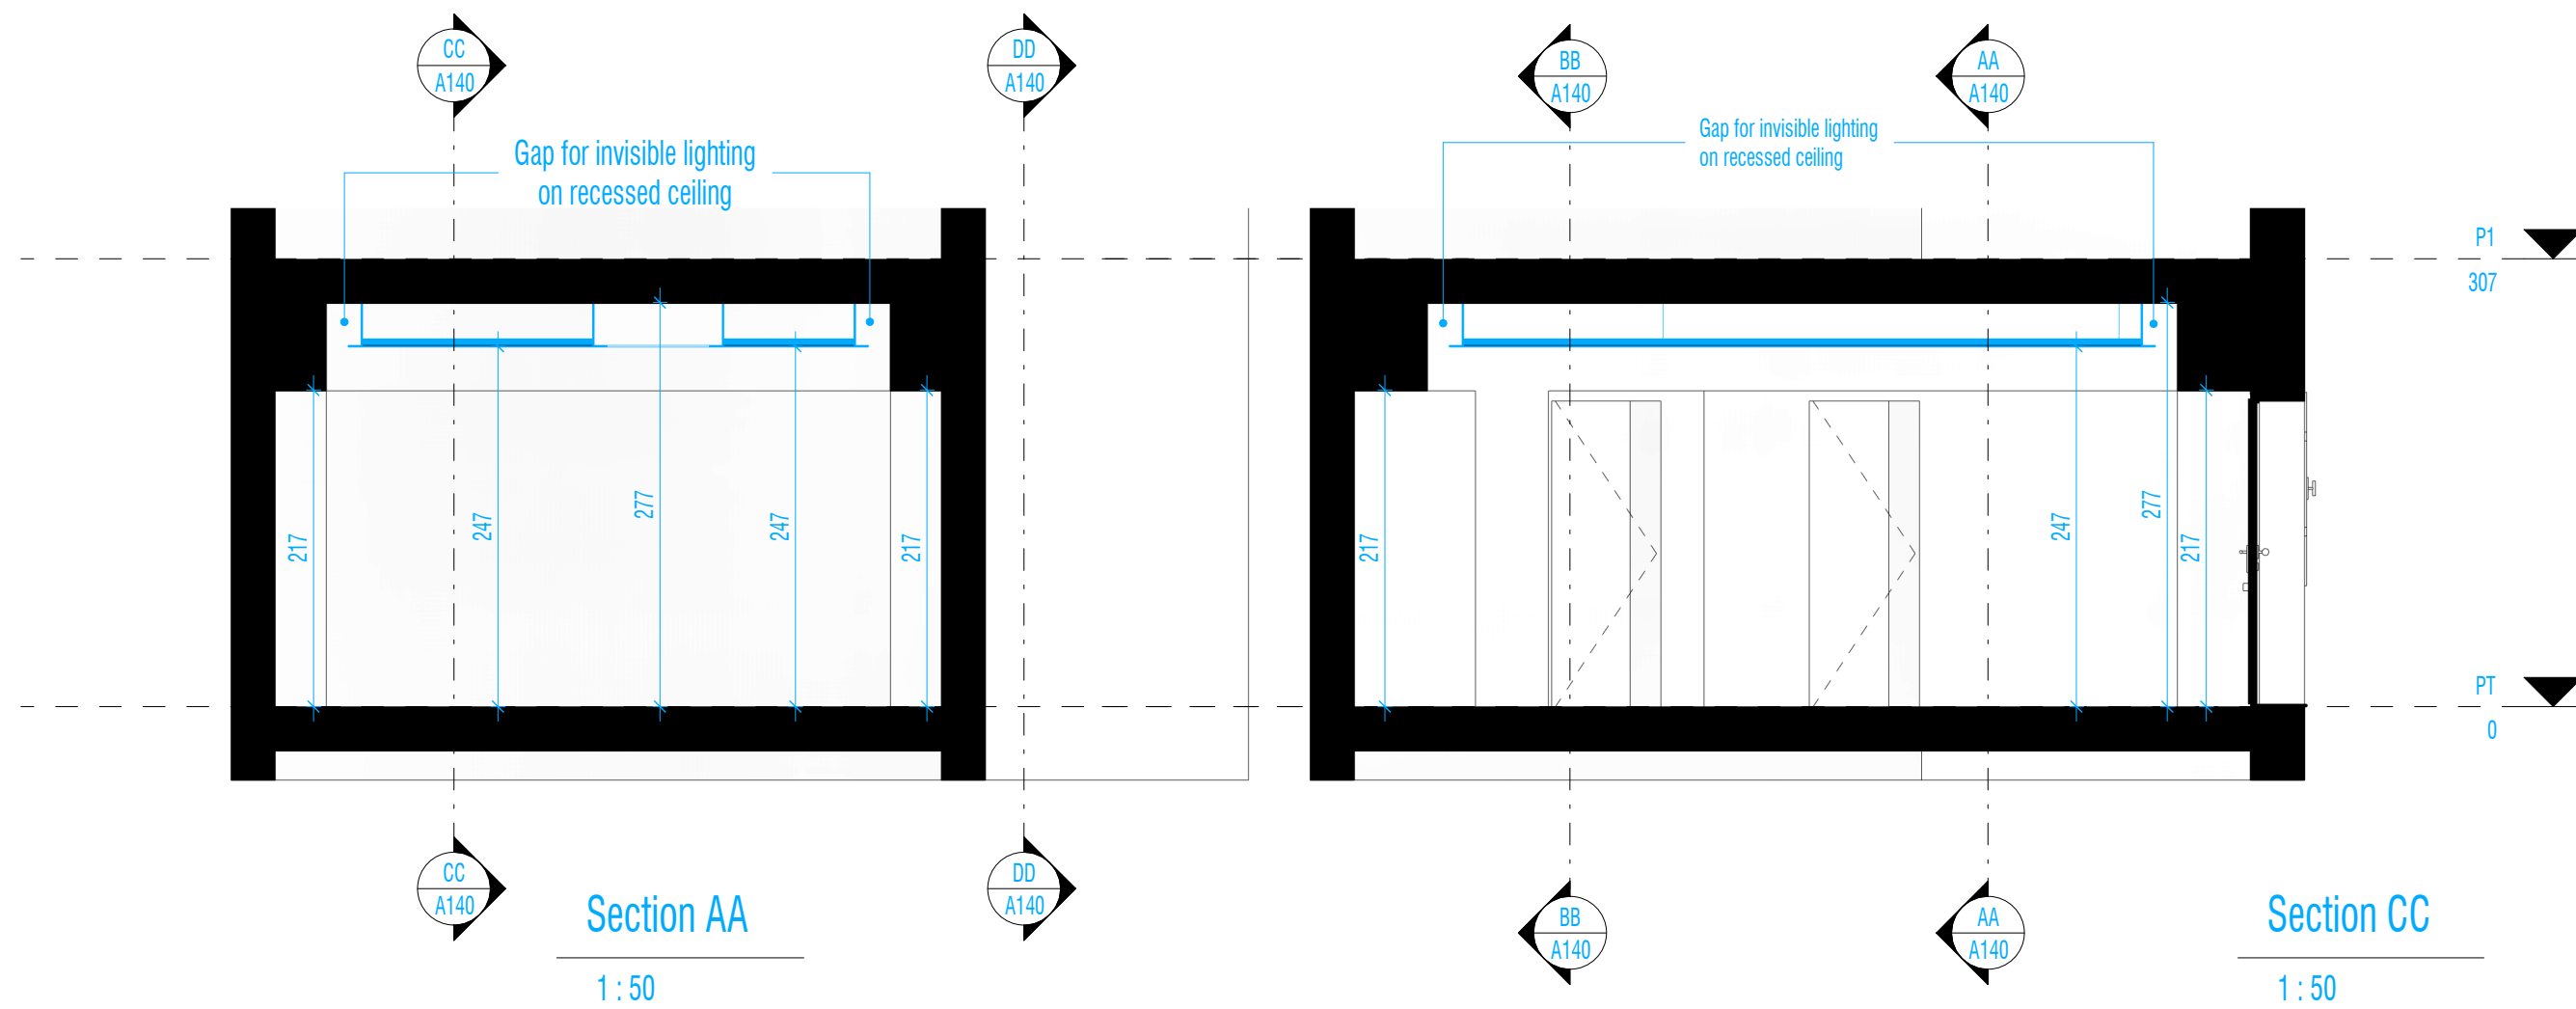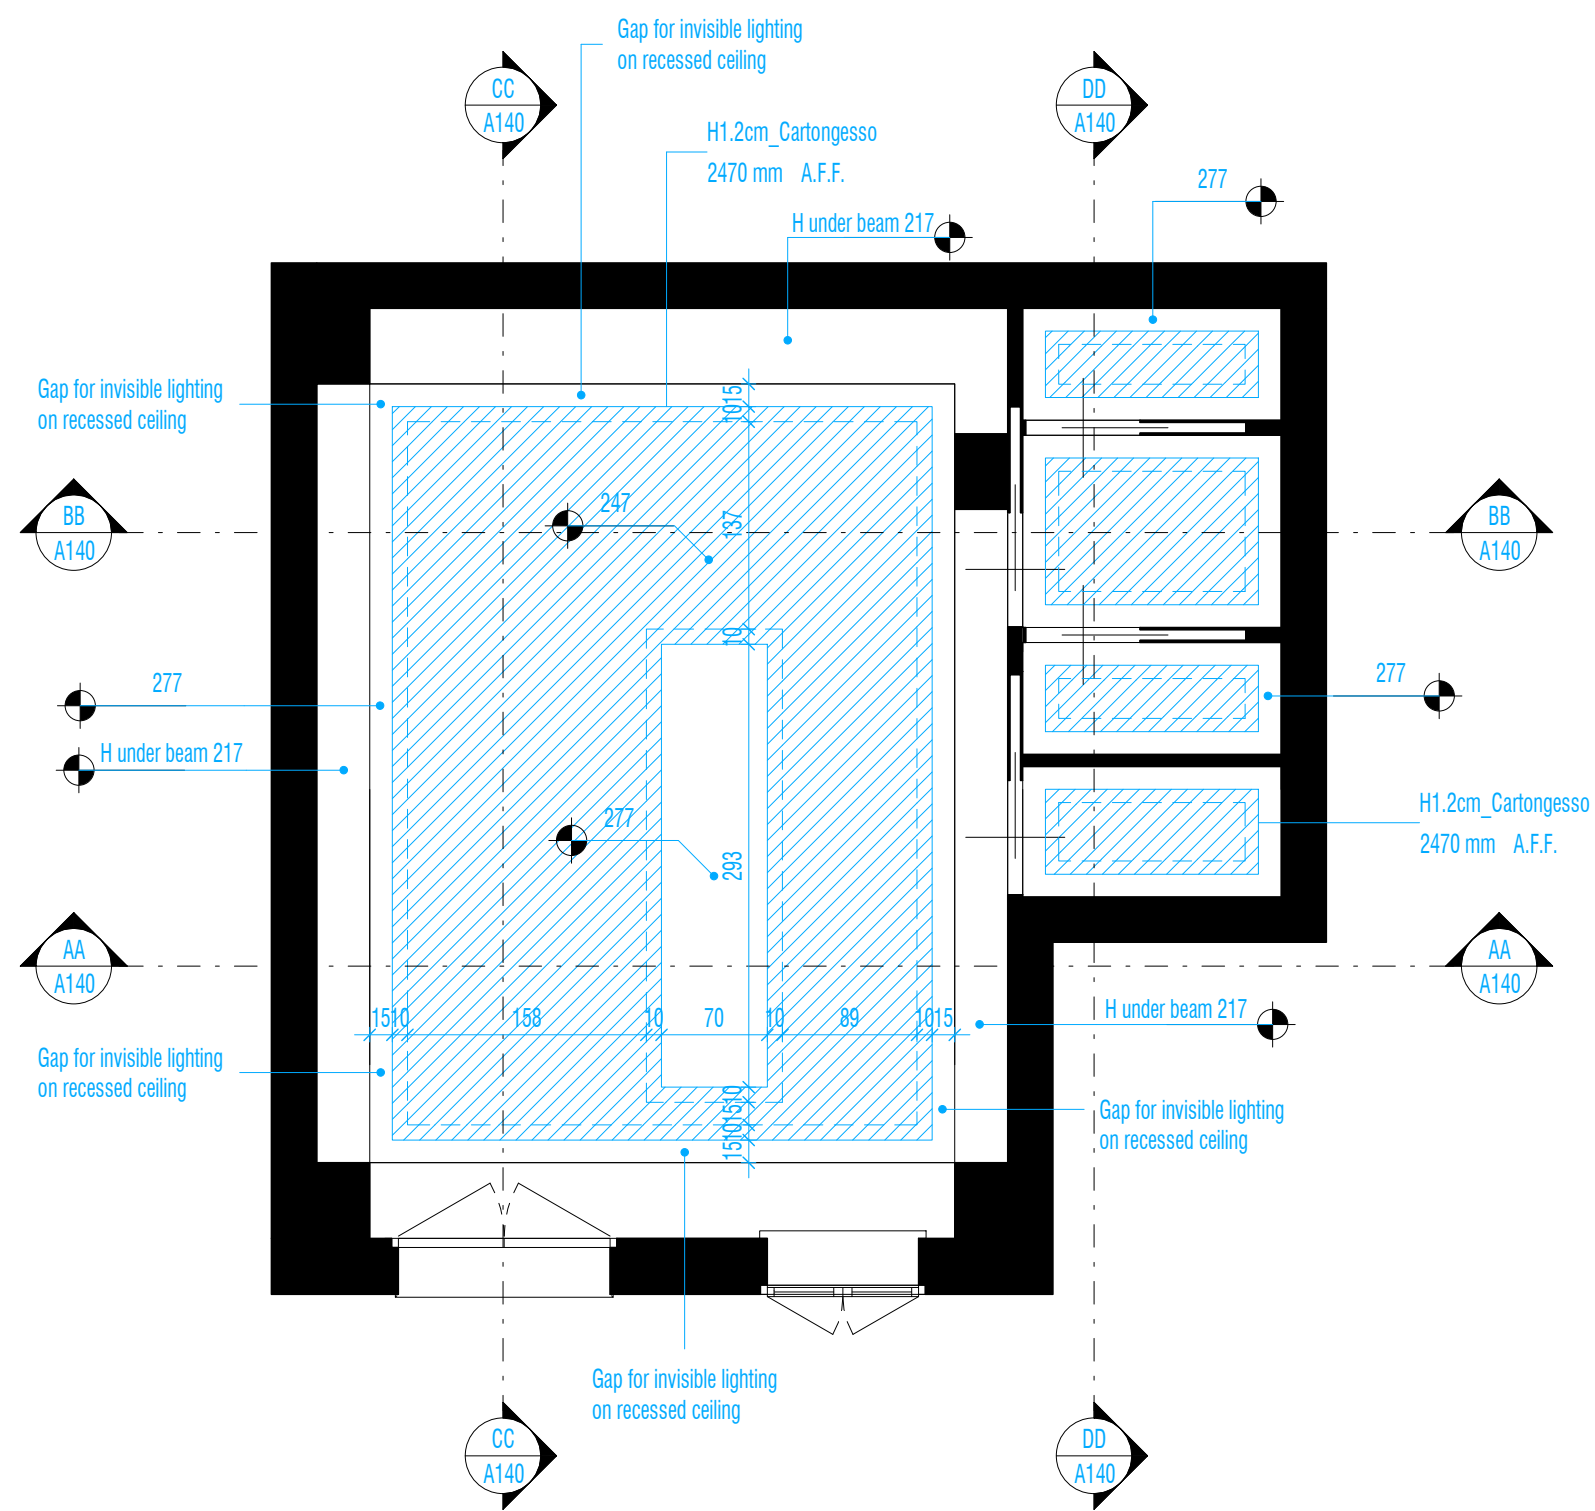


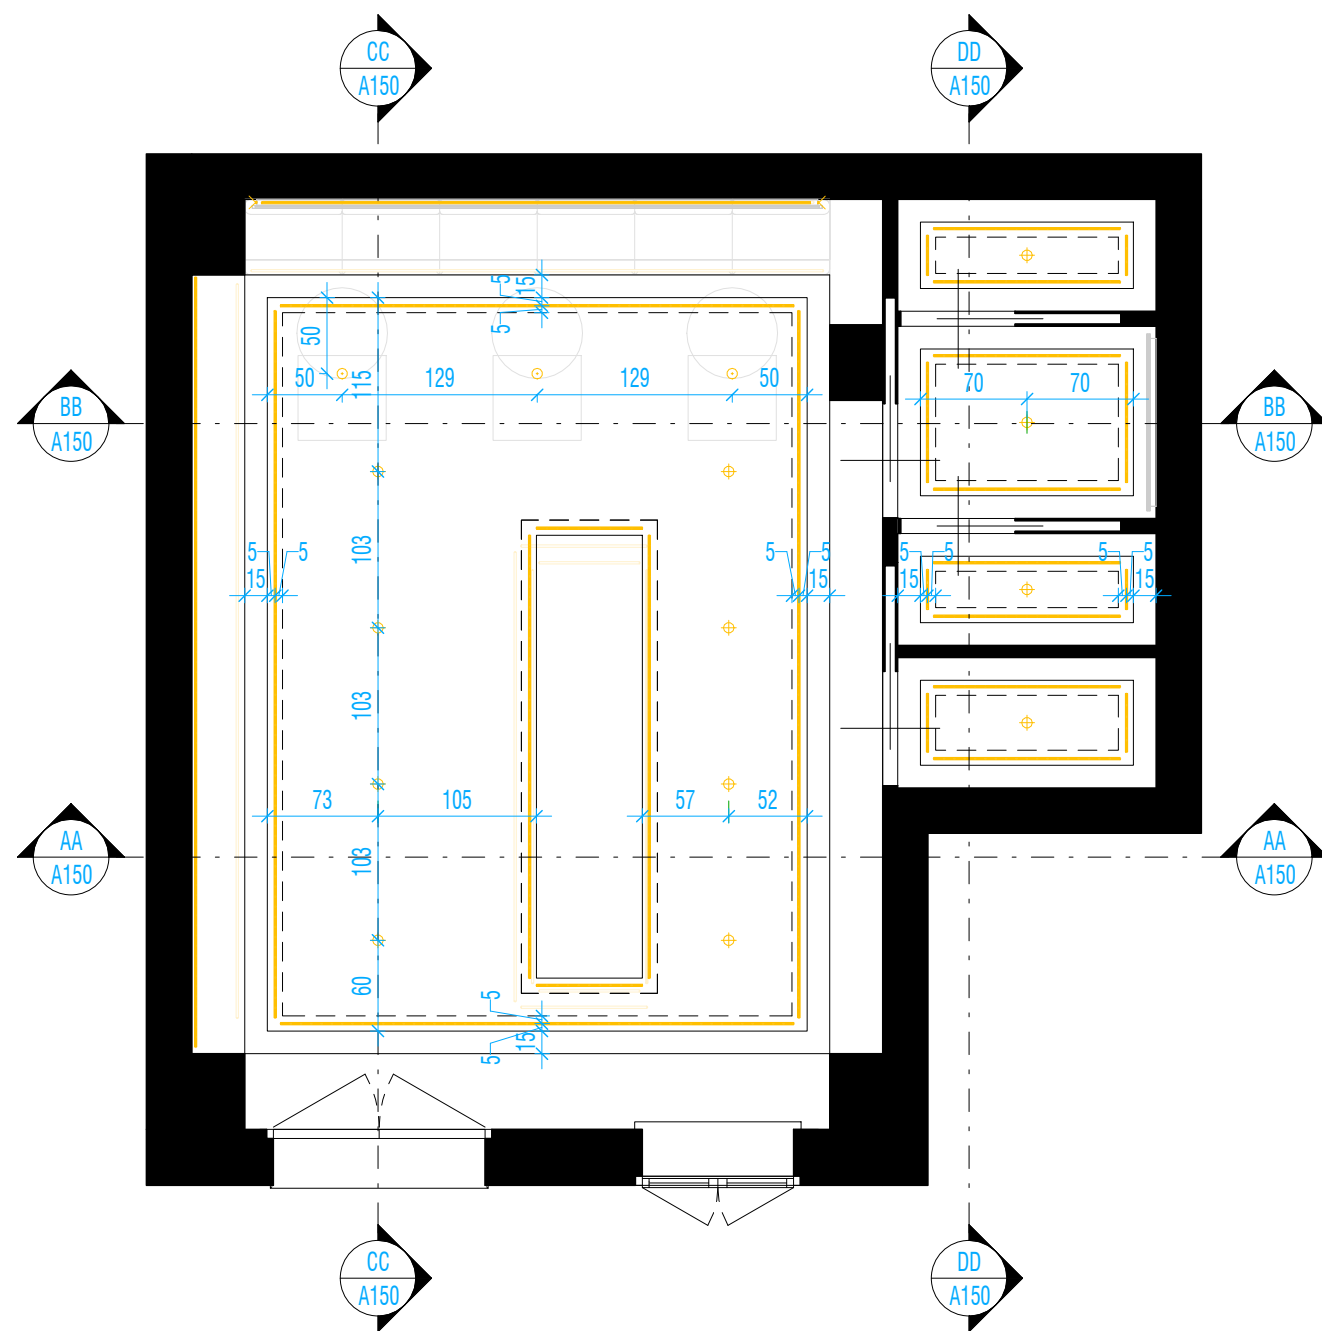

Lighting Fixtures Legend

-   L1_Fixed luminaire on false ceilings
-   L2_LED Strip
-   L3_Pendant luminaire on false ceilings





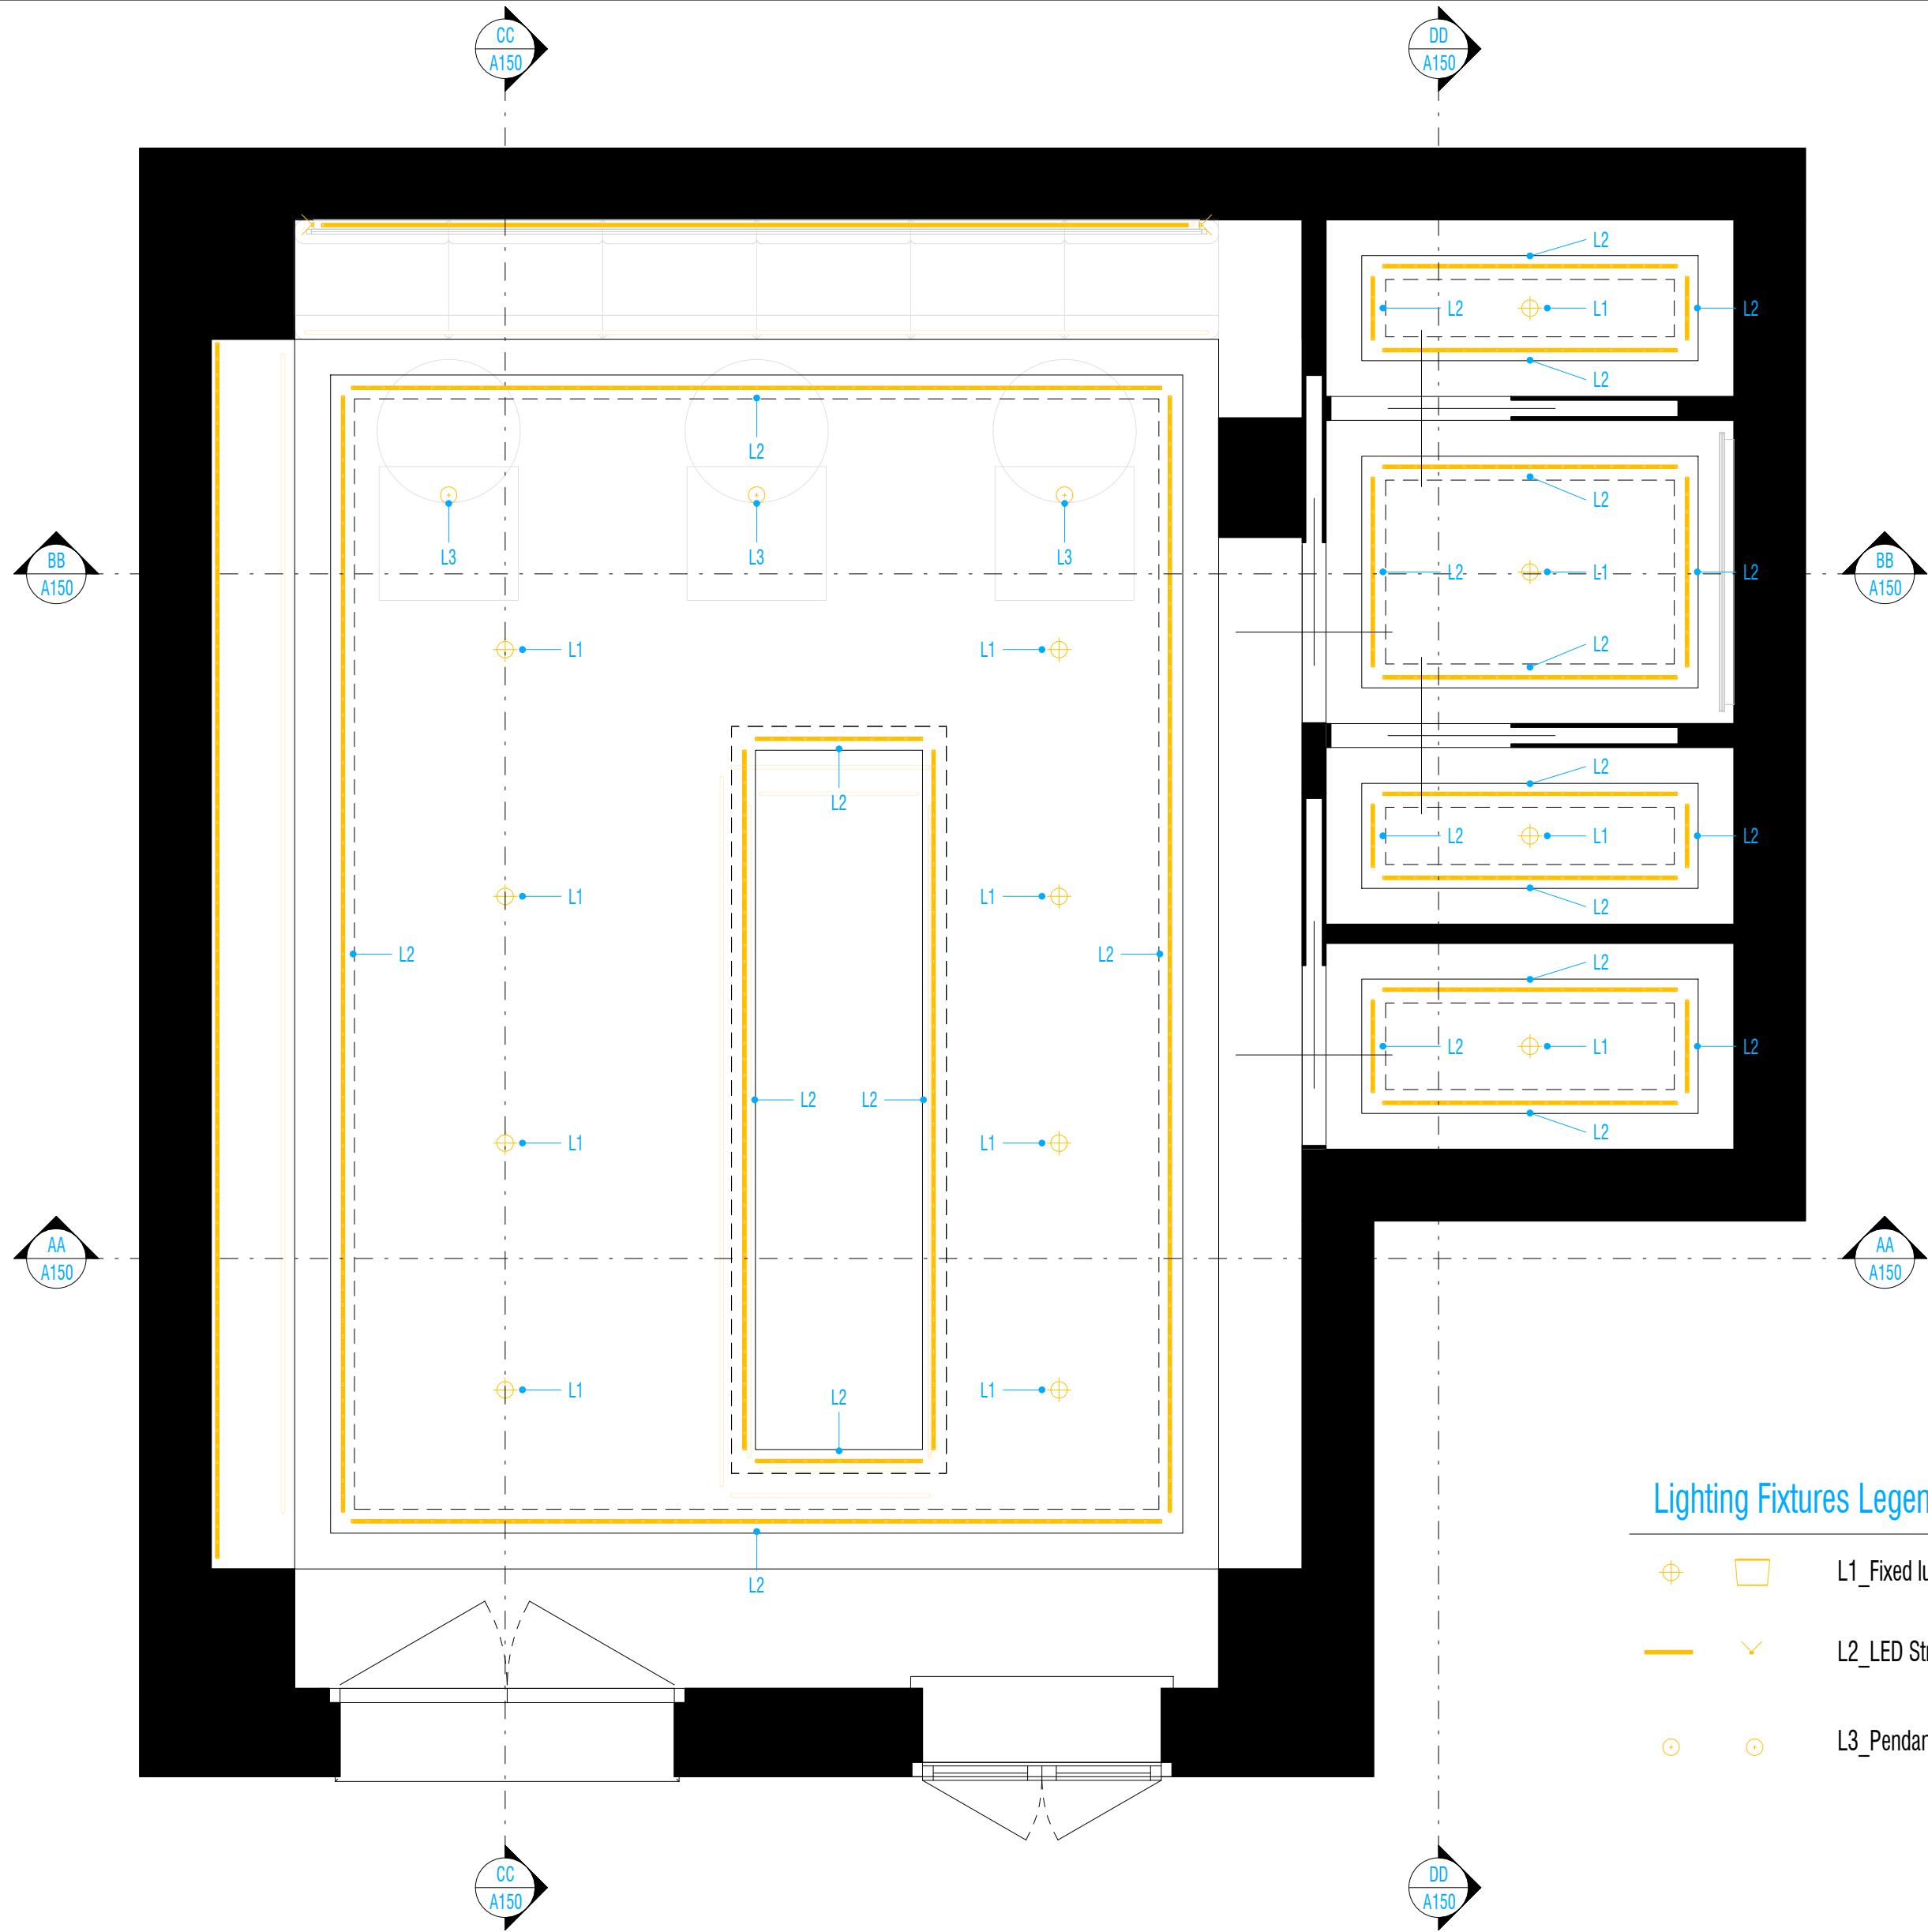

Lighting Fixtures Legend






-   L1_Fixed luminaire on false ceilings
-   L2_LED Strip
-   L3_Pendant luminaire on false ceilings

Lighting Fixtures Schedule									
Code	Image	Quantity	Manufacturer	Model	Description	Unit cost	Partial cost	Link	
L1		12	iGuzzini spa -Recanati-Italy	P587	Fixed circular recessed luminaire. Flush mount installation on false ceilings.	€140.40	€1,684.80	http://www.iguzzini.com/p587/	
L2		38	iGuzzini spa -Recanati-Italy	M827	Linear lighting product – with white monochrome LEDs – made on a white flexible strip	€90.00	€3,420.00	http://www.iguzzini.com/m827/	
L3		3	Reggiani Spa Illuminazione	Yori pendant Ø35mm	Pendant LED light mounted on false ceiling, adjustable height. Brushed copper finish.	€180.00	€540.00	http://www.reggiani.net/pendants-and-floor-lamps/family/yori-pendant-o35mm	
Total cost Lighting Fixtures: 53							€5,644.80		



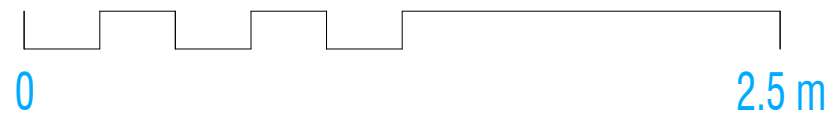
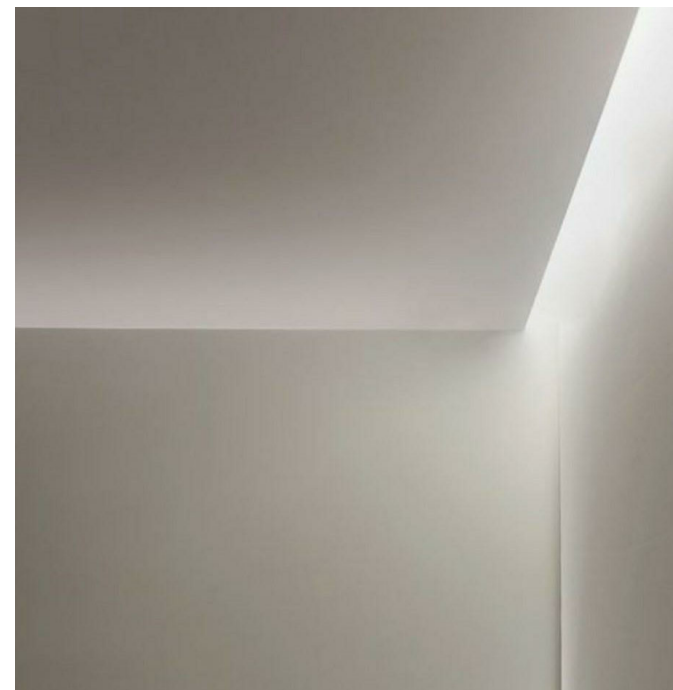





Furniture Schedule

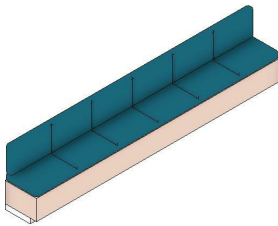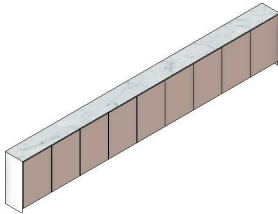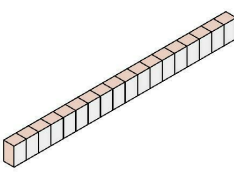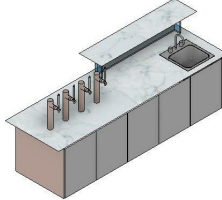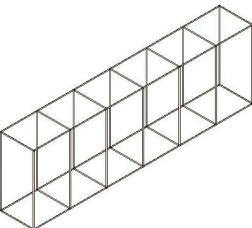
Code	Image	Quantity	Manufacturer	Model	Description	Unit Cost	Partial Cost	URL
F1		3	Midj	Infinity Ø 60	Table with round base in black lacquered steel. Crystalceramic top, glossy black greek marble.	€350.00	€1,050.00	https://www.albaplusth.com/it/prodotti/tavoli-di-design/riace/tondo
F2		3	Alias	Taormina 504	Armchair with structure in chromed steel. Seat and back in solid plastic material padded with cfc free expanded polyurethane foam, removable cover in fabric.	€590.00	€1,770.00	https://alias.design/en-us/products/taormina/taormina-chair-504
F3		1	Local Artisan	Custom	Custom sofa. Wooden structure with copper finish, seat and back pillows with removable cover in fabric.	€1,200.00	€1,200.00	
F4		1	Local Artisan	Custom Wall Unit	Custom wall unit with 9 cabinets, wood structure and top in Croatian Kirmenjak Light Blue. Wooden doors with copper paint finish.	€2,250.00	€2,250.00	
F5		1	Local Artisan	Custom Wall-hanged Unit	Custom wall-hanged unit, 18 modules L513 X H43 X D35cm. Door panels with white powder coated mesh. Alluminium structure powder coated with copper colour.	€2,160.00	€2,160.00	
F6		1	Local Artisan	Custom Bar Console	Custom Bar Console, Croatian Kirmenjak Light Blue countertop copper finishes on sides and back.	€5,000.00	€5,000.00	
F7		1	Local Artisan	Custom Ceiling-hanged Unit	Custom ceiling-hanged unit, 6 modules L260 X H82 X D40cm. Alluminium frame structure powder coated with copper colour. Transparent glass shelves.	€540.00	€540.00	


Furniture Schedule

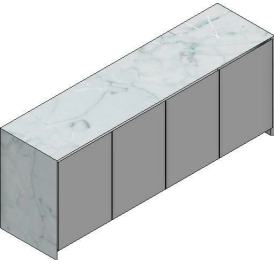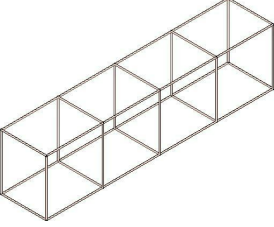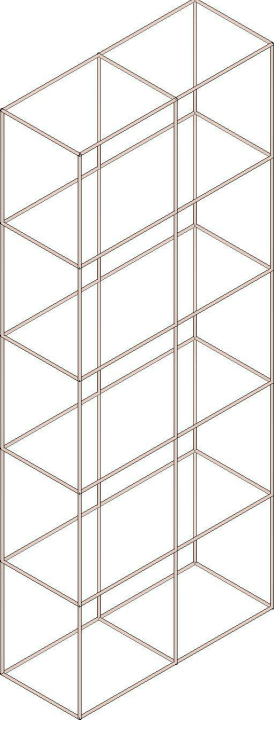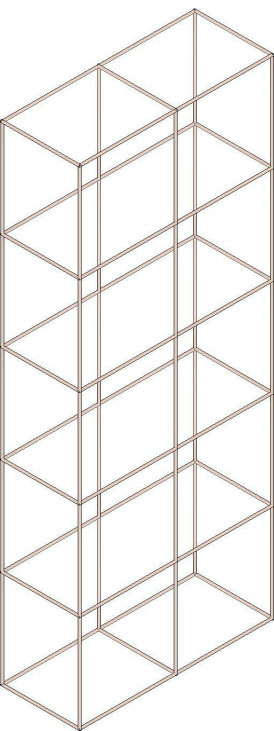Code	Image	Quantity	Manufacturer	Model	Description	Unit Cost	Partial Cost	URL
F8		1	Local Artisan	Custom Wall Unit	Custom wall unit with work plane and 4 cabinets, wood structure, Croatian Kirmenjak Light Blue and sides. Wooden doors with copper paint finish.	€1,000.00	€1,000.00	
F9		1	Local Artisan	Custom Wall-hanged Unit	Custom wall-hanged unit, 4 modules L173 X H43 X D35cm. Alluminium frame structure powder coated with copper colour. Transparent glass shelves.	€360.00	€360.00	
F10		1	Local Artisan	Custom Wall Unit	Custom wall unit, 10 modules L86 X H217 X D35cm. Alluminium frame structure powder coated with copper colour. Transparent glass shelves.	€900.00	€900.00	
F11		1	Local Artisan	Custom Wall Unit	Custom wall unit, 10 modules L80 X H217 X D35cm. Alluminium frame structure powder coated with copper colour. Transparent glass shelves.	€900.00	€900.00	
F12		1	Local Artisan	Custom Mirror	Custom mirror L 377 X H 117cm. LED illuminated perimeter, aluminium frame 2cm copper finish	€1,050.00	€1,050.00	
Total furniture cost: 16							€18,180.00	

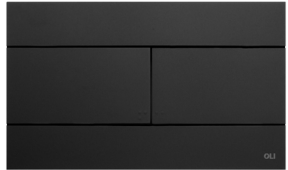

Bathroom Fixtures Schedule									
Code	Image	Quantity	Manufacturer	Model	Description	Unit Cost	Partial Cost	URL	
B1		1	Local Artisan	Custom Bathroom Wall Unit	Custom bathroom wall unit, L127 X H32 X D55cm. Alluminium frame structure, Ø1.5 cm circular solid section, powder coated with copper colour. Granite top.	€350.00	€350.00		
B2		2	Laufen	Bowl washbasin	Washbasin bowl, SaphirKeramik, EN 31, dimensions D380 mm H 130mm.	€350.00	€700.00	https://www.laufen.com/catalogue/product?productCode=811435	
B3		2	Hansgrohe	AXOR Uno Select 200	AXOR Uno Basin mixer Select 200 with waste set. Polished Red Gold finish.	€275.00	€550.00	https://www.axor-design.com/int/articledetail-axor-uno-basin-mixer-select-200-for-wash-bowls-with-waste-set-45013000	
B4		1	Local Artisan	Custom Mirror	Custom mirror L 117 X H 105cm. LED illuminated perimeter, aluminium frame 2cm copper finish	€365.50	€365.50		
B5		2	Duravit	252809	Toilet wall mounted 4,5 l, washdown model, EWL class 1. 370 X 570 mm, white alpin color. Design by Philippe Starck	€234.00	€468.00	https://www.duravit.co.uk/products/all_series/me_by_starck.com-en.html?product=2324615	
B6		2	OLI	Slim	Mechanic control plate for in-wall cisterns, 255 X 150 mm, 6,5mm thickness. Dual flush with Braille sinaletic, black Soft Touch finishing.	€112.45	€224.90	https://www.oli-world.com/en/categories/installation-systems/control-plate/slim/black-soft-touch-----/	
Total furniture cost: 10							€2,658.40		

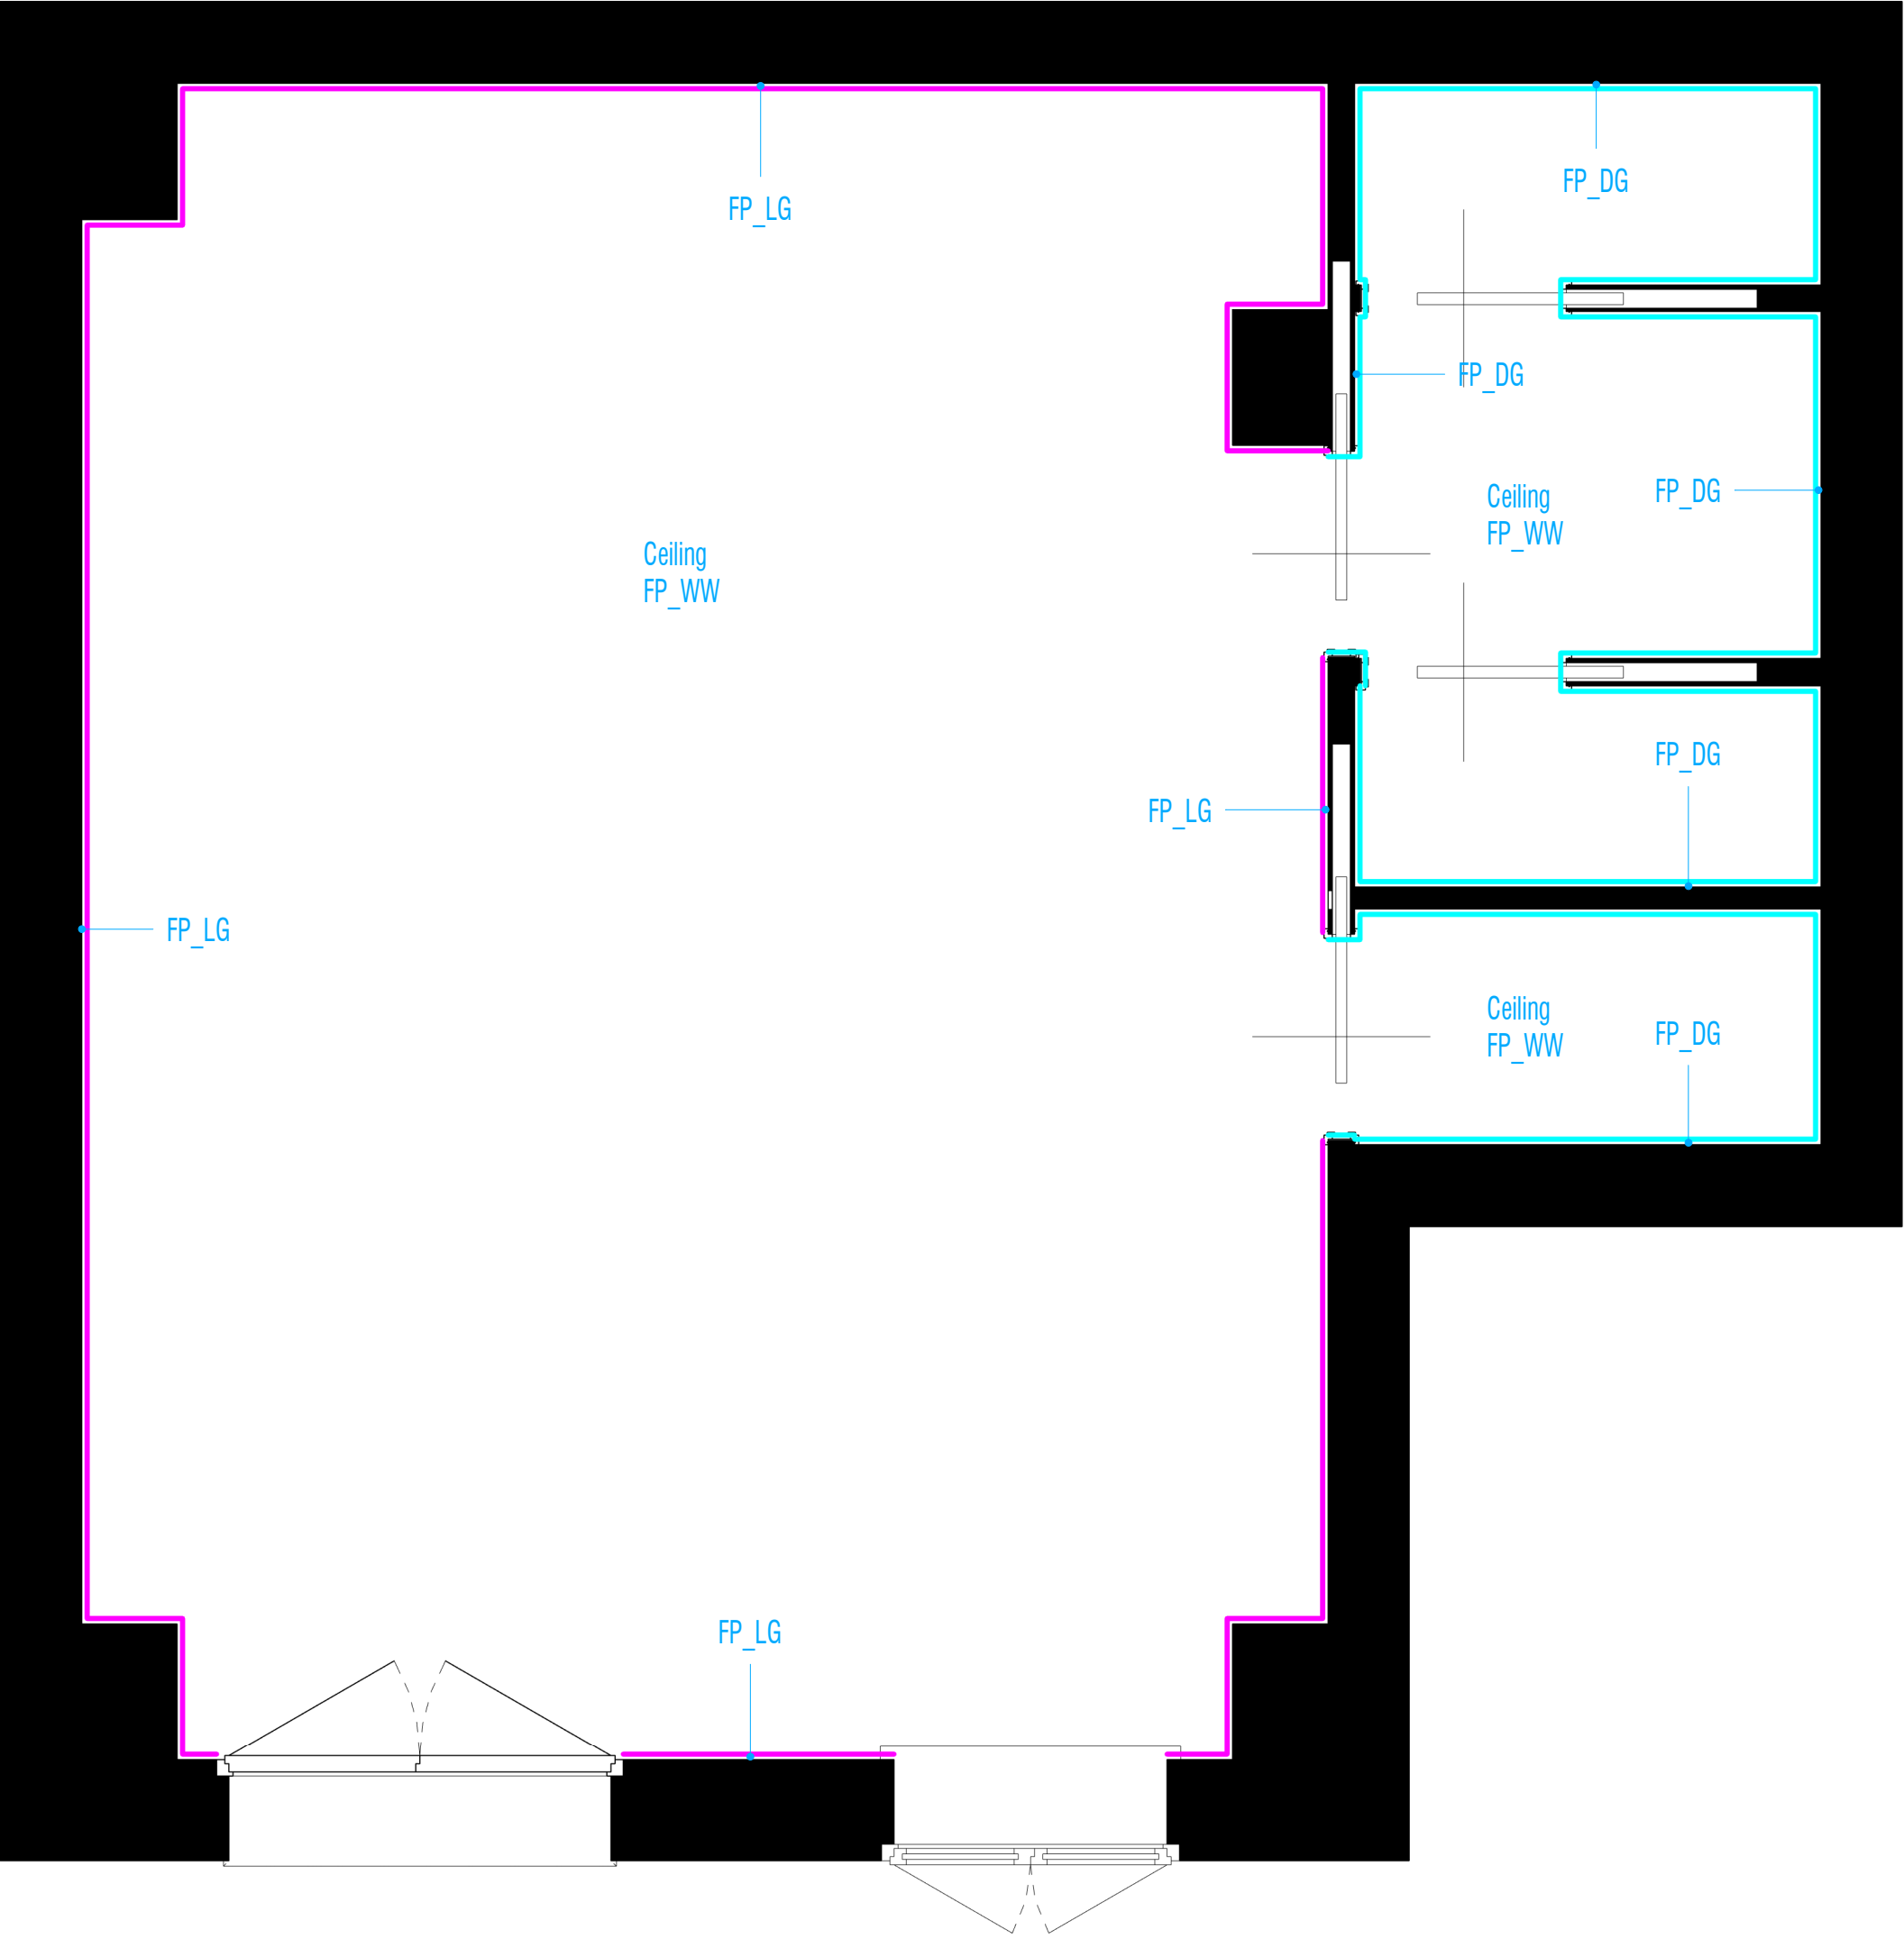


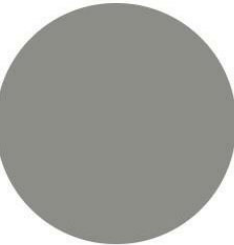Wall and Ceiling Finishes							
Code	Image	Area	Manufacturer	Name	URL	Cost	Partial Cost
<u>FP_DG</u>		41.53 m²	Farrow & Ball	Plummett No.272	https://www.farrow-ball.com/paint-colours/plummett	€12.75	€529.49
<u>FP_LG</u>		33.07 m²	Farrow & Ball	Blackened No.2011	https://www.farrow-ball.com/paint-colours/blackened	€12.75	€421.58
FP_WW		10.85 m²	Farrow & Ball	All White No.2005	https://www.farrow-ball.com/paint-colours/all-white	€12.75	€138.37
Total Wall and Ceiling Finish Cost		85.45 m²					€1,089.45



AR_WM

Furniture Finish -
White aluminium
mesh

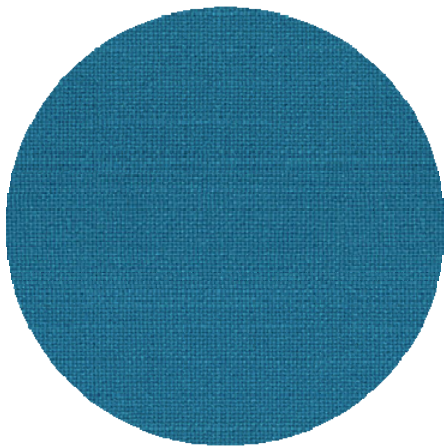


AR_SD

Fabric - Blue




FP_WW

Paint_Light grey

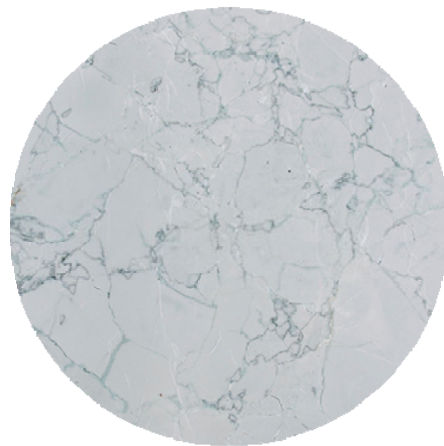

AR_KB

Furniture Finish -
Kirmenjak Light Blue -
Polished

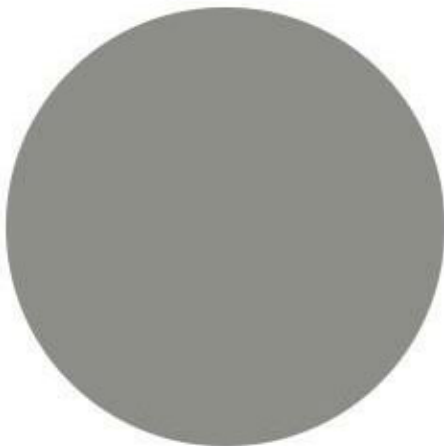

FP_DG

Paint_Dark grey



FL_KL

Floor Finish - Typical
croatian limestone




AR_CP

Furniture Finish -
Copper




FP_LG

Paint_Light grey

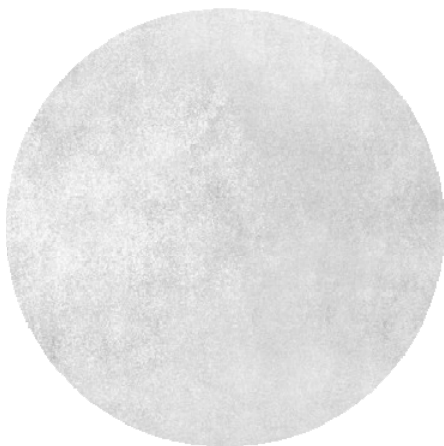


FL_NB

Floor Finish - Polished
concrete

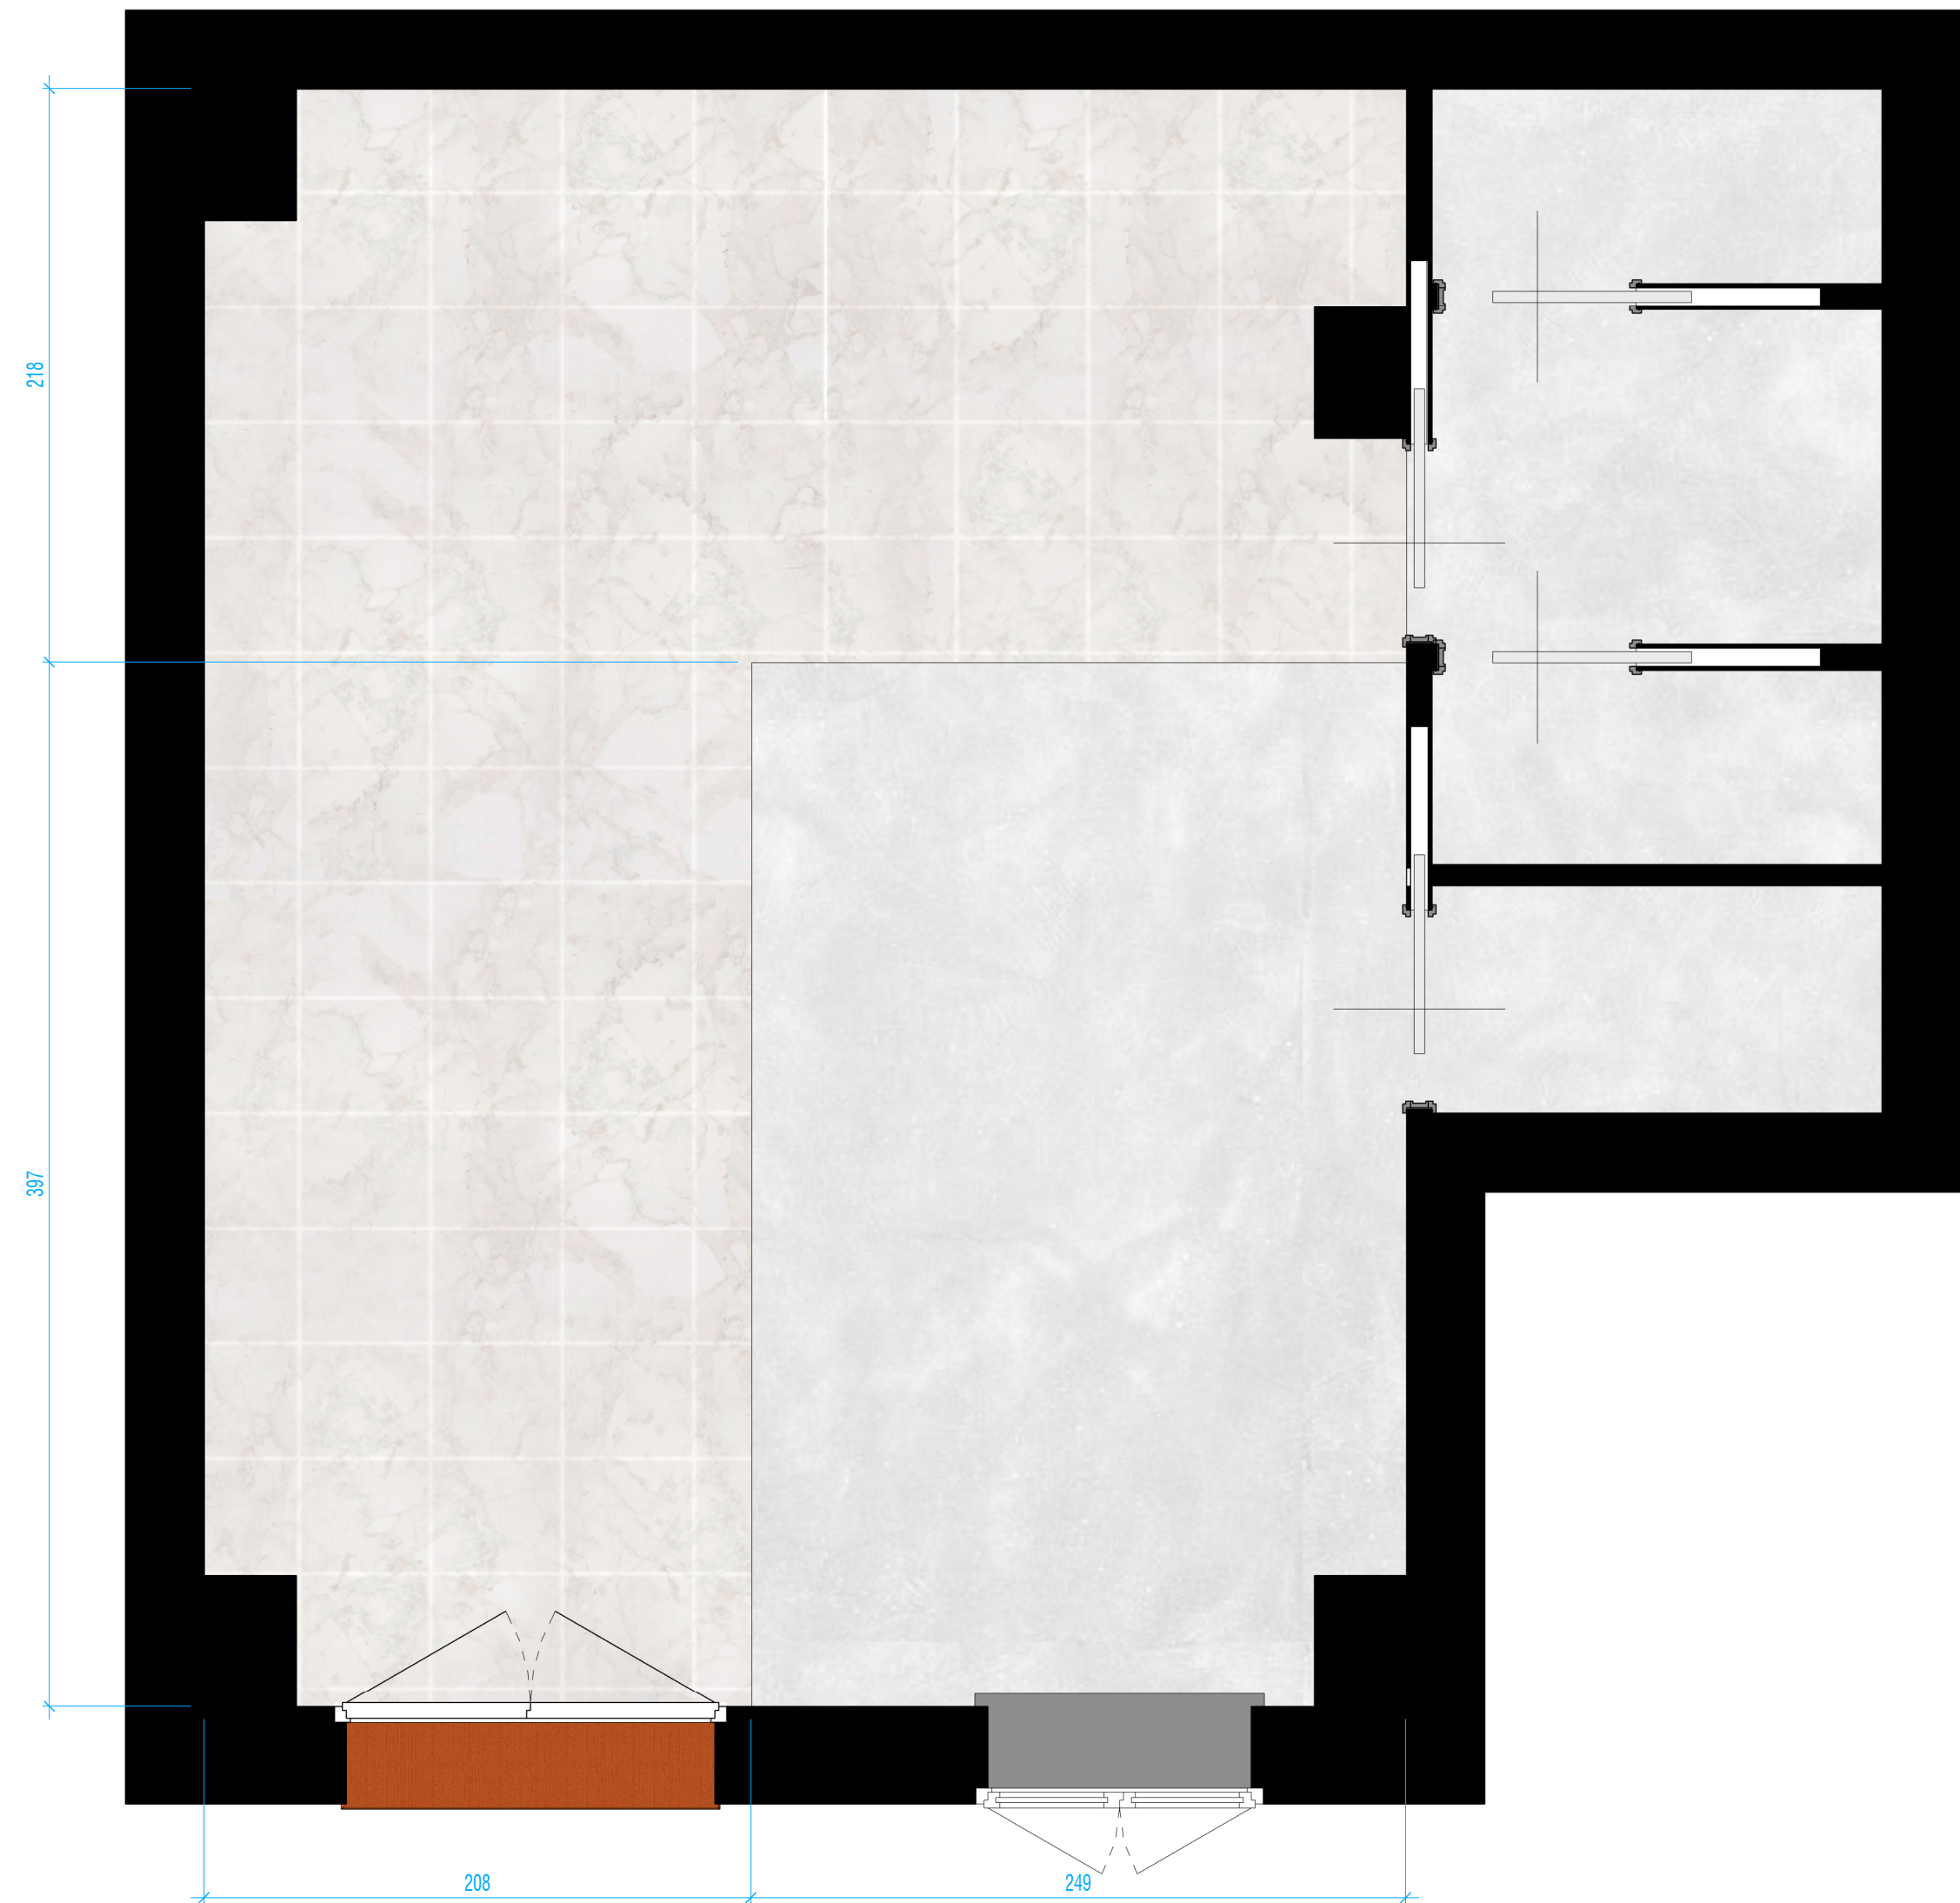


Floor Finishes								
Code	Image	Area	Manufacturer	Name	Description	Cost	Partial Cost	URL
FL_KL		17.70 m²	Kamen d.d. Pazin	Kirmenjask Light Polished	Floor Finish - Typical croatian limestone	€38.00	€672.47	https://www.kamen.hr/en/materijali/kirmenjask-svijetli-polirano/
FL_NB		16.22 m²	Mapei	Mapefloor Decor 700	Floor Finish - Polished concrete	€65.00	€1,054.04	https://www.mapei.com/it/en/products-and-solutions/products/detail/mapefloor-decor-700
Total Floor Finishes Cost		33.91 m²					€1,726.51	

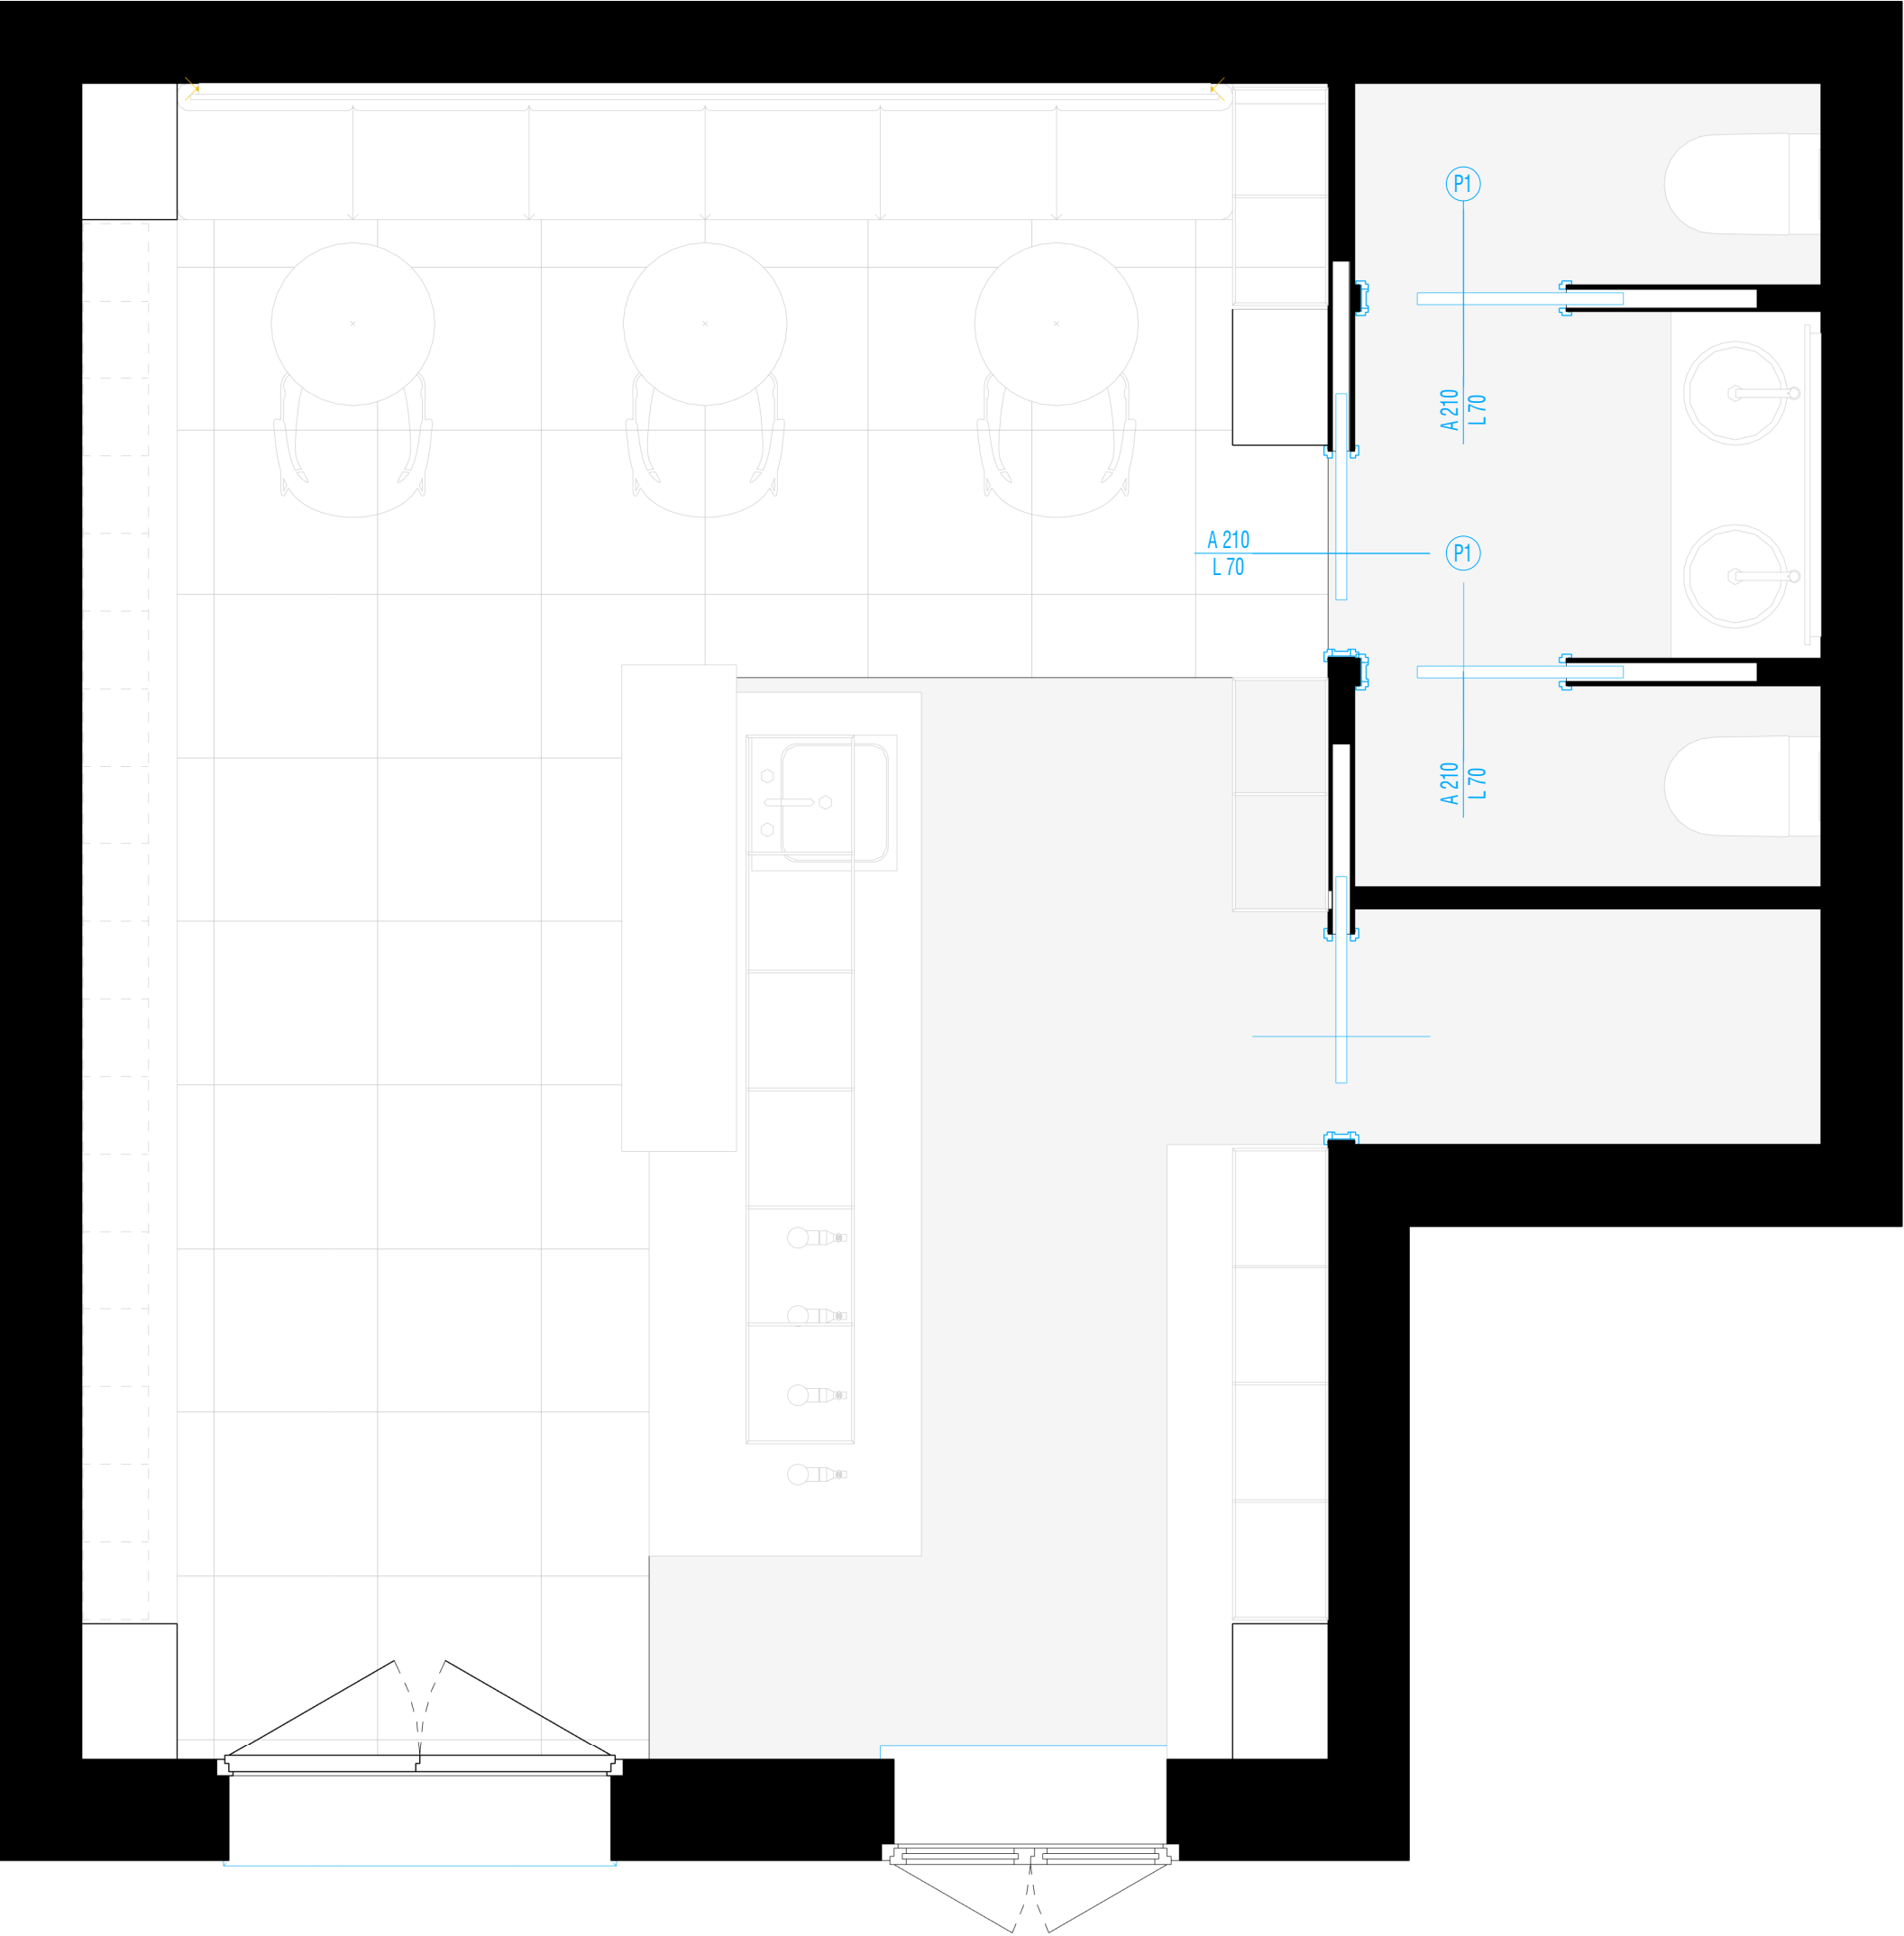

Door list											
Type	Image	Type	Mark	Count	Manufacturer	Model	Height	Width	Cost	Partial Cost	URL
		P1		3	Bertolotto	Varsavia	210	70	€232.00	€696.00	https://www.bertolotto.com/









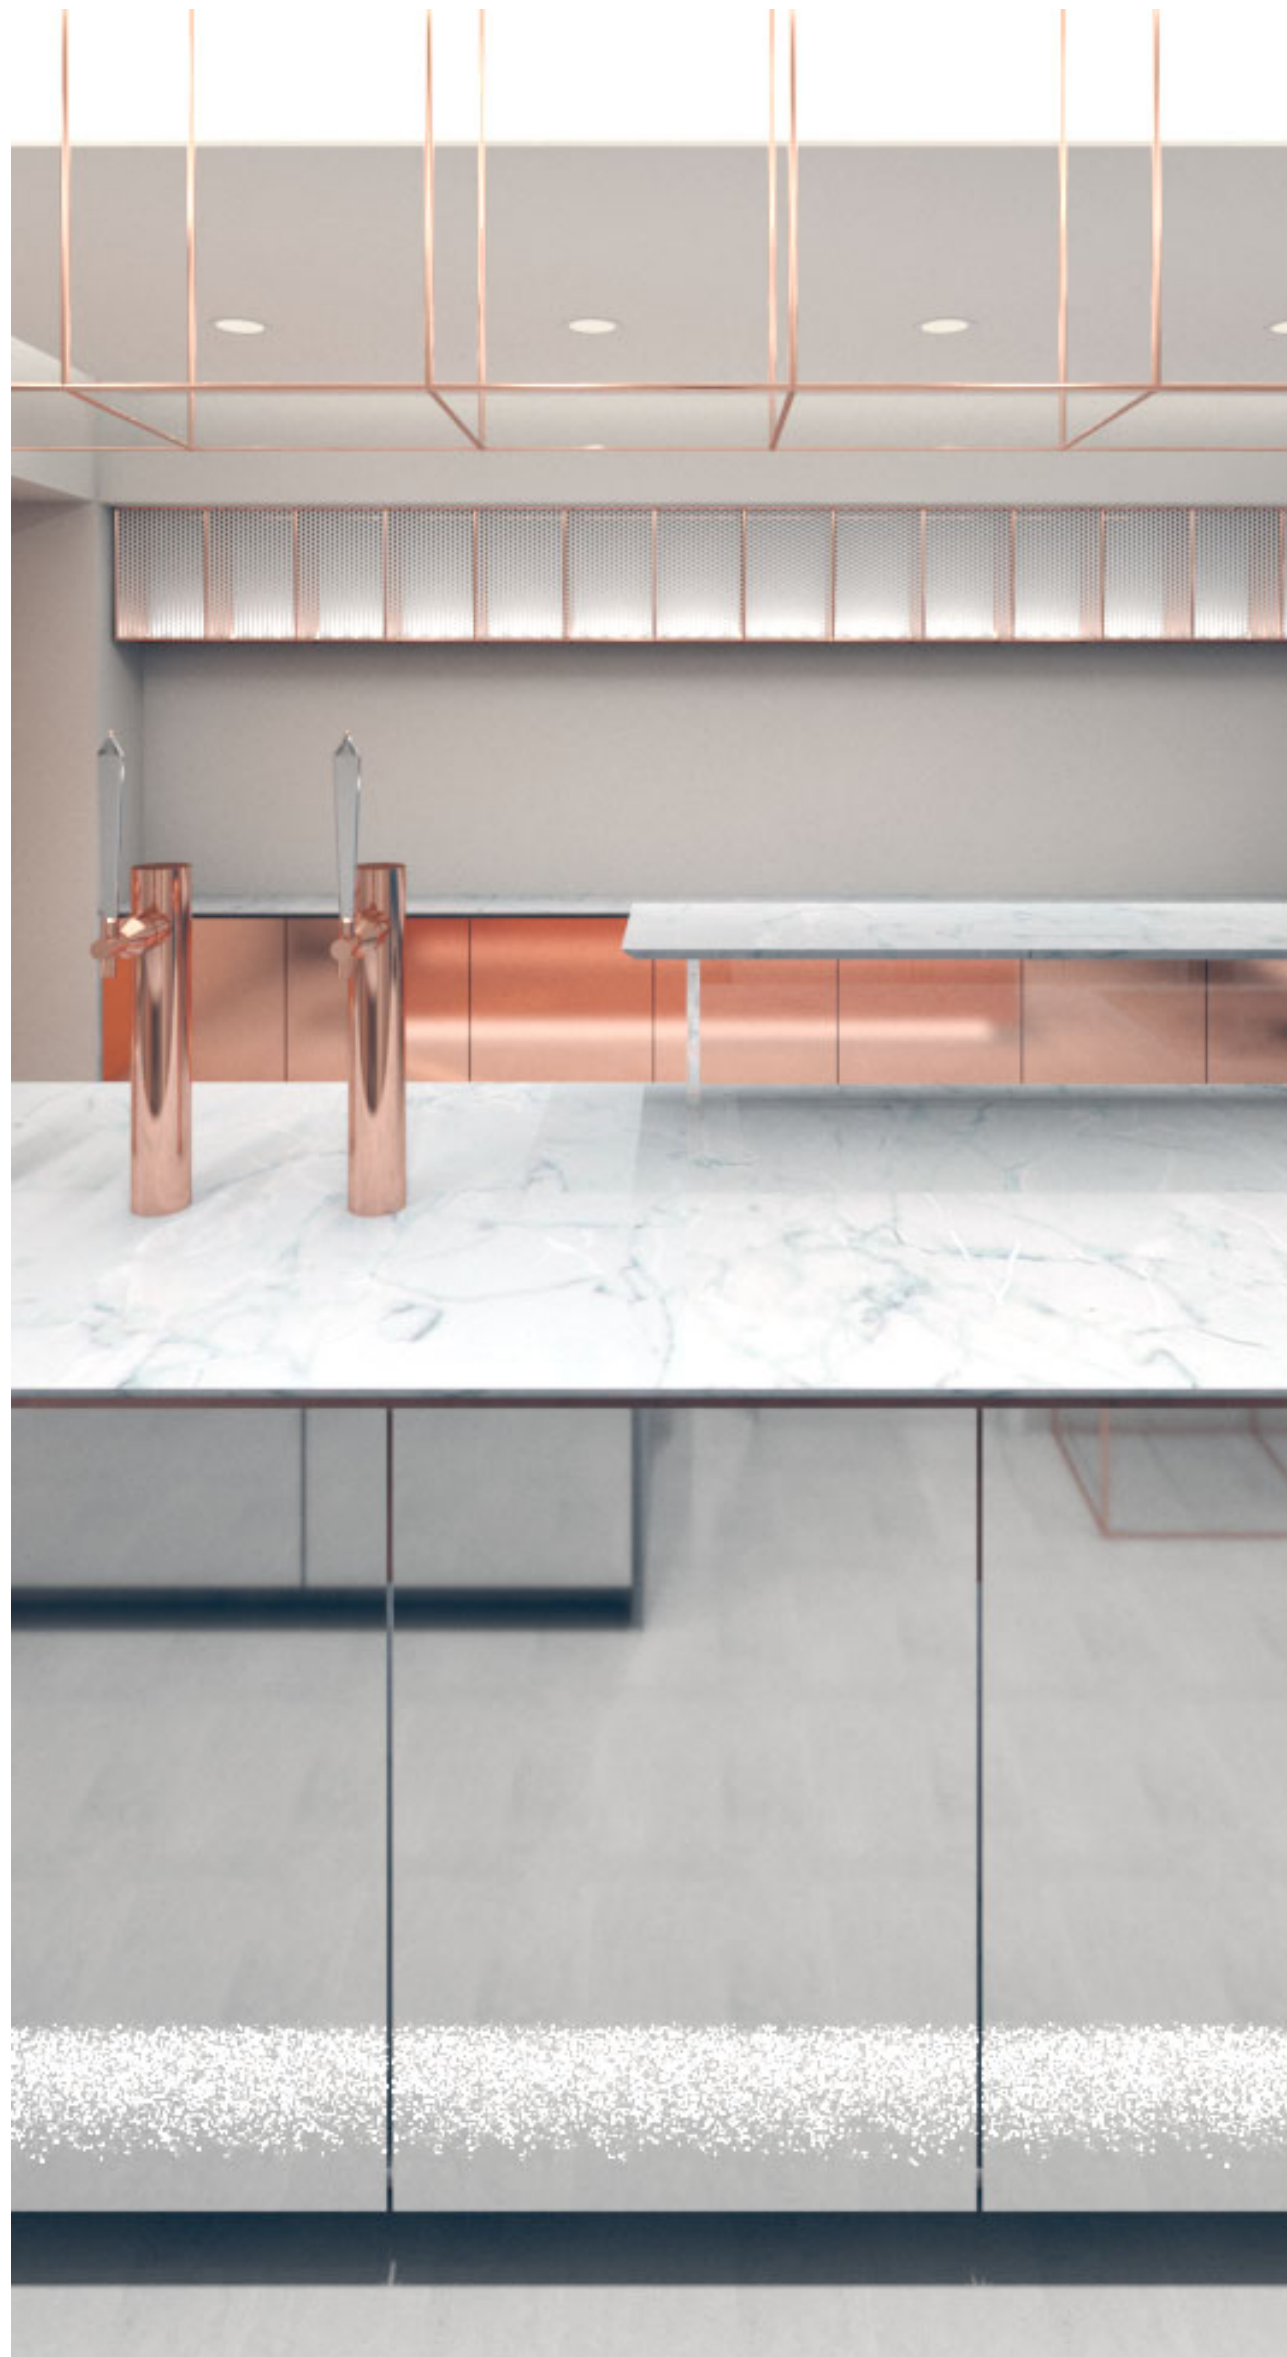


01 DEMOLITION AND CONSTRUCTION WORKS					
Description	U.M.	Quantity		Costs	
		Area	N	Unit Cost	Total Cost
Demolizion di tramezzi	sqm	14.71 m²		€30.00	€441.35
Demolizione di controsoffittatura	sqm	7.82 m²		€15.00	€117.25
Demolizione di massetto in malta cementizia	sqm	33.88 m²		€16.00	€542.11
Demolizione di pavimento in ceramica	sqm	8.35 m²		€18.00	€150.32
Demolizione di pavimento in parquet	sqm	25.58 m²		€20.00	€511.58
Rimozione di porte interne	nr		3	€50.00	€150.00
Rimozione e/o demolizioni di: sanitari, rubinetterie, lavabi, vecchi impianti elettrici e idraulici esterni alle murature	nr		4	€40.00	€160.00
Demolizion di tramezzi	sqm	1.59 m²		€30.00	€47.56
Costruzione di nuovi tramezzi compreso il tamponamento delle aperture delle porte spostate.	sqm	12.95 m²		€48.00	€621.47
Fornitura e posa in opera di controtelai per porte, compresa la quadratura del vano.	nr		3	€150.00	€450.00
Posa in opera massetto in malta cementizia	sqm	33.88 m²		€20.00	€677.64
Posa in opera pavimentazione a piastrelle	sqm	17.70 m²		€61.00	€1,079.49
Posa in opera pavimentazione a resina	sqm	16.22 m²		€93.00	€1,508.09
Realizzazione di controsoffitti con lastre di cartongesso, fissate mediante viti al soffitto, compresa la stuccatura dei giunti, le opere provvisionali e i ponteggi.	sqm	18.66 m²		€50.00	€933.15
Realizzazione di impianti idrico sanitari bagno e cucina	nr		7	€250.00	€1,750.00
Realizzazione impianto elettrico	nr		53	€60.00	€3,180.00
Total Cost for demolition and construction works		226.91 m²	103		€12,320.01

For Furniture, Finishes and fixture refer to relative sheet.

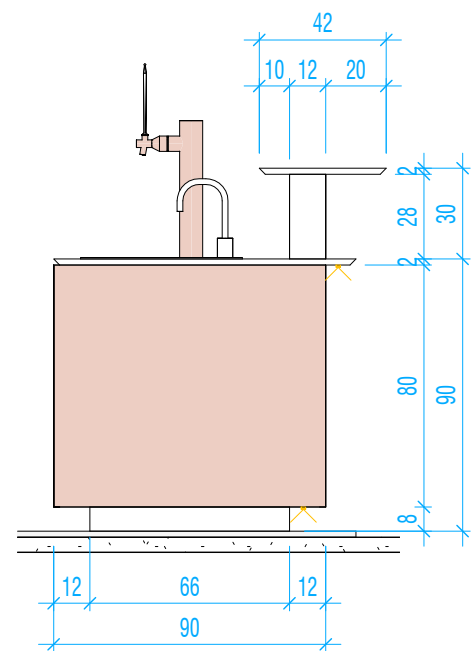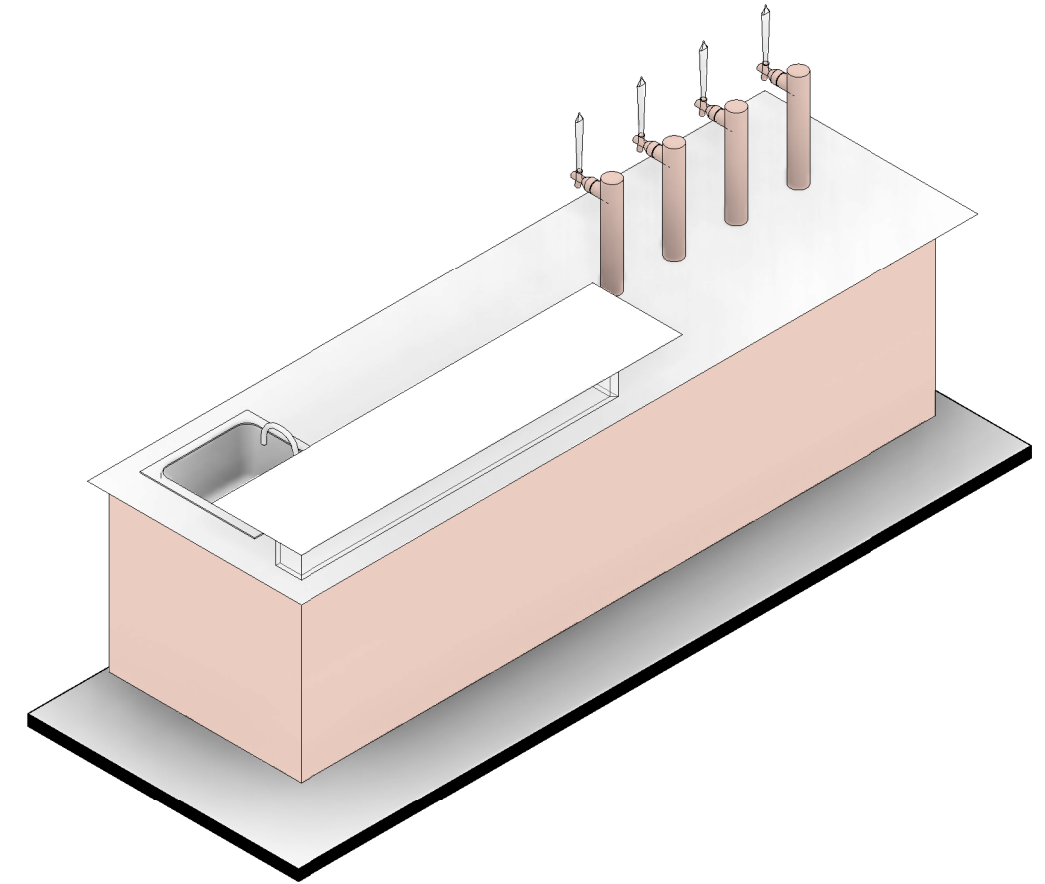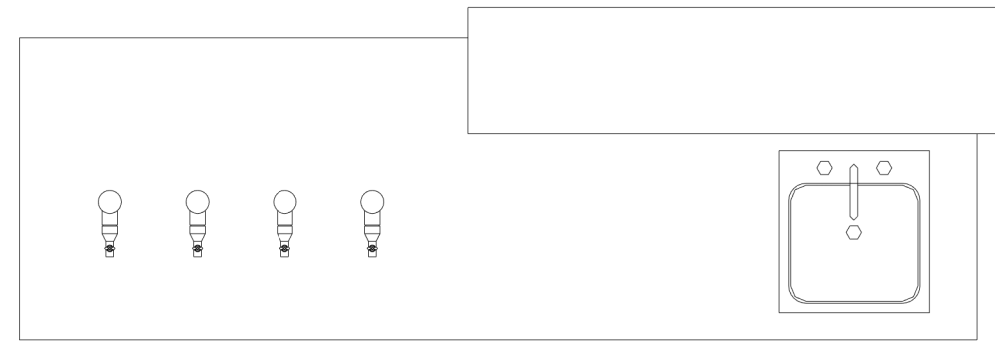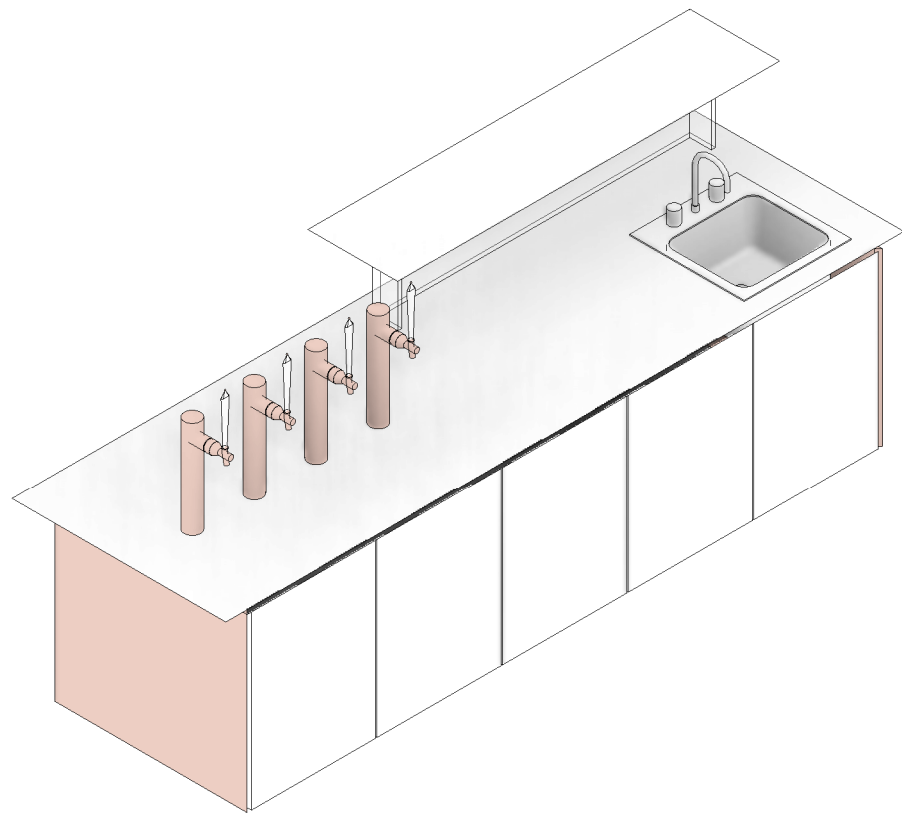


ARC_SDP_Furniture 1_N

1 : 25

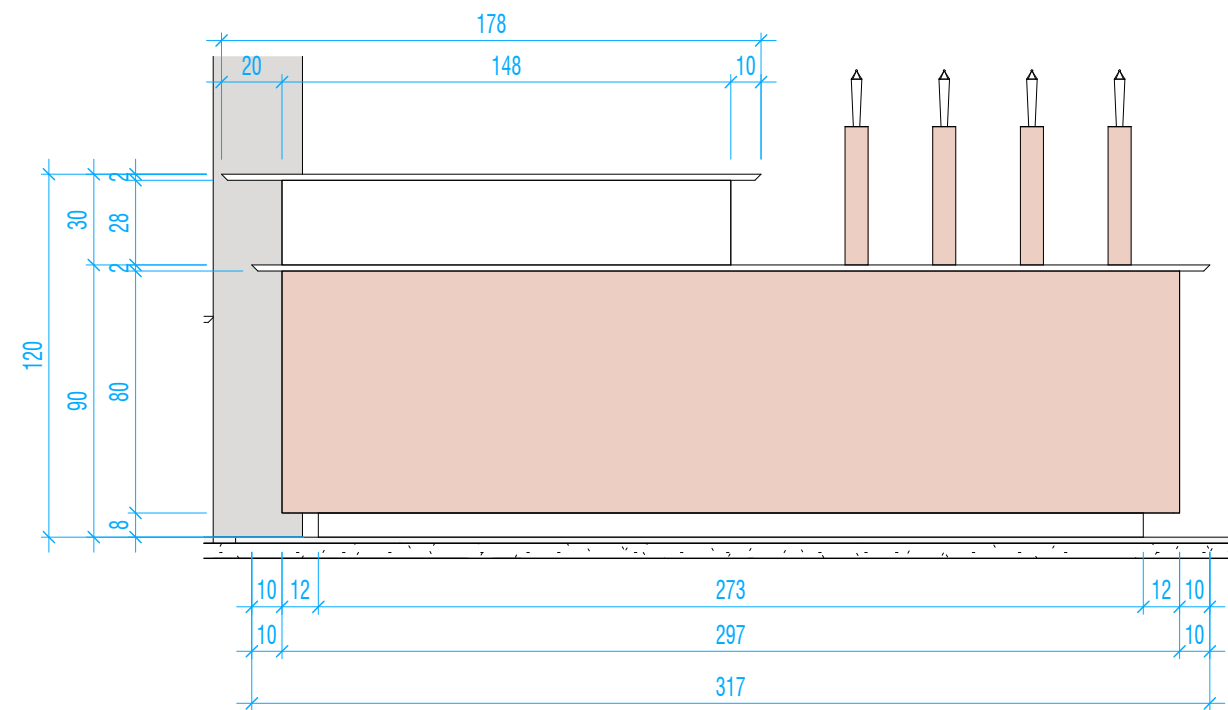

ARC_SDP_Furniture 1_W

1 : 25

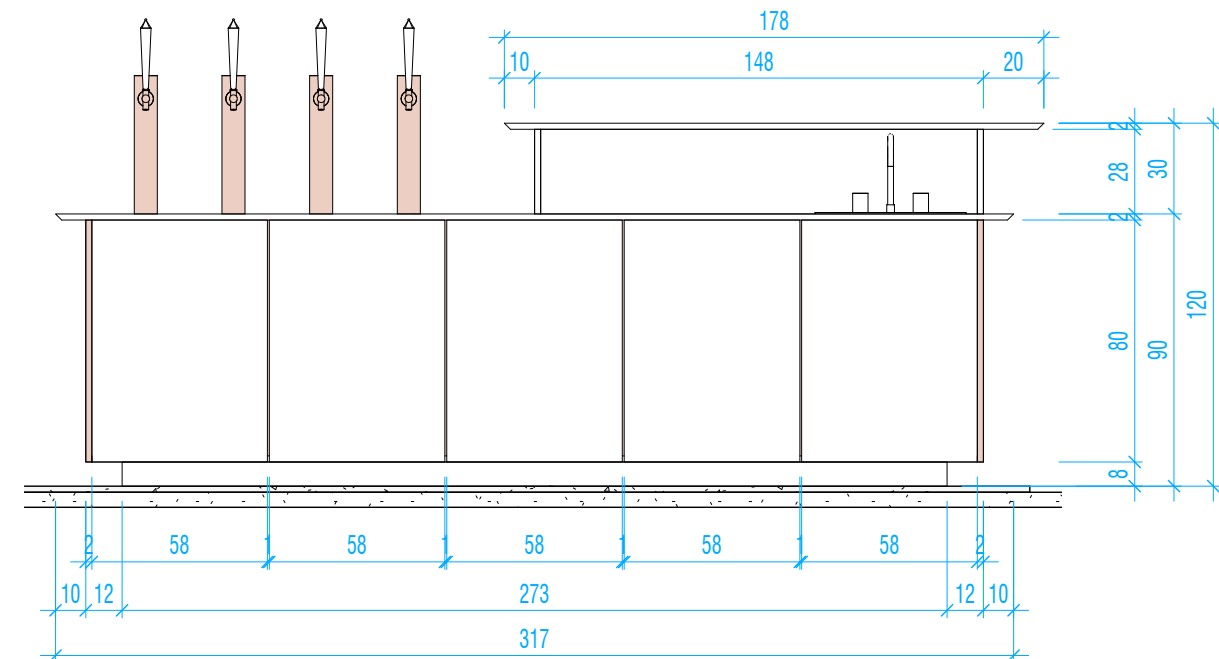

ARC_SDP_Furniture 1_E

1 : 25