




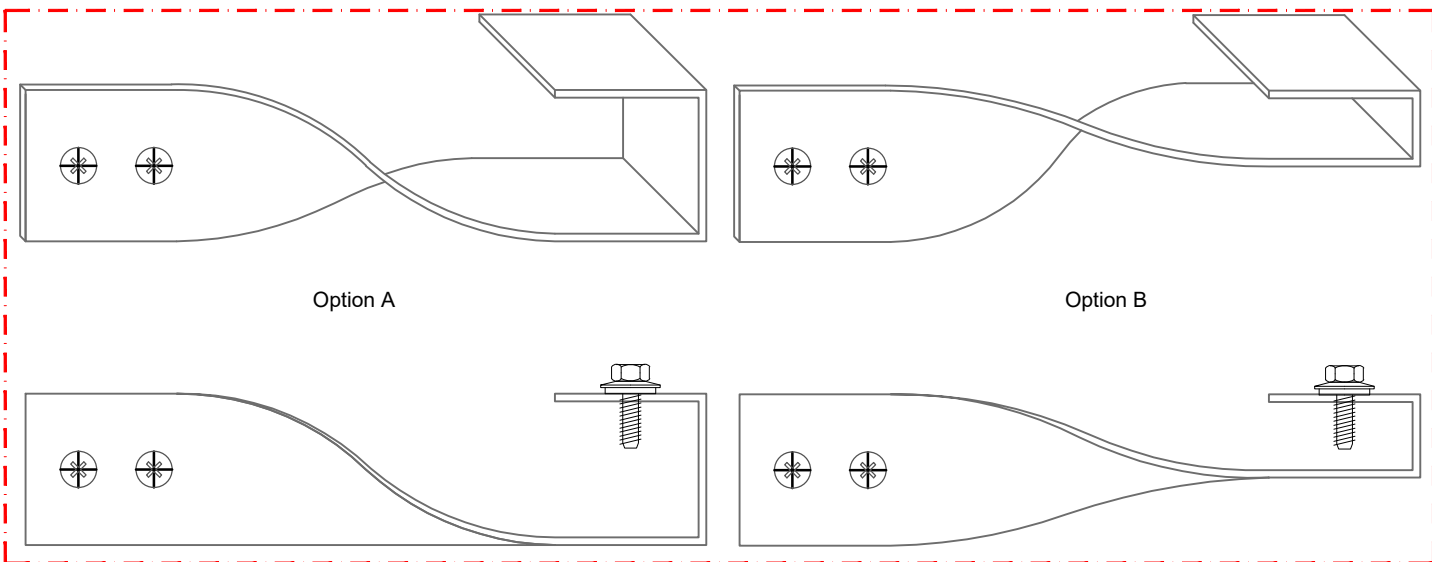


1c Stainless steel flat bars (bent) Examples (to be defined)
SCALE: 1:2

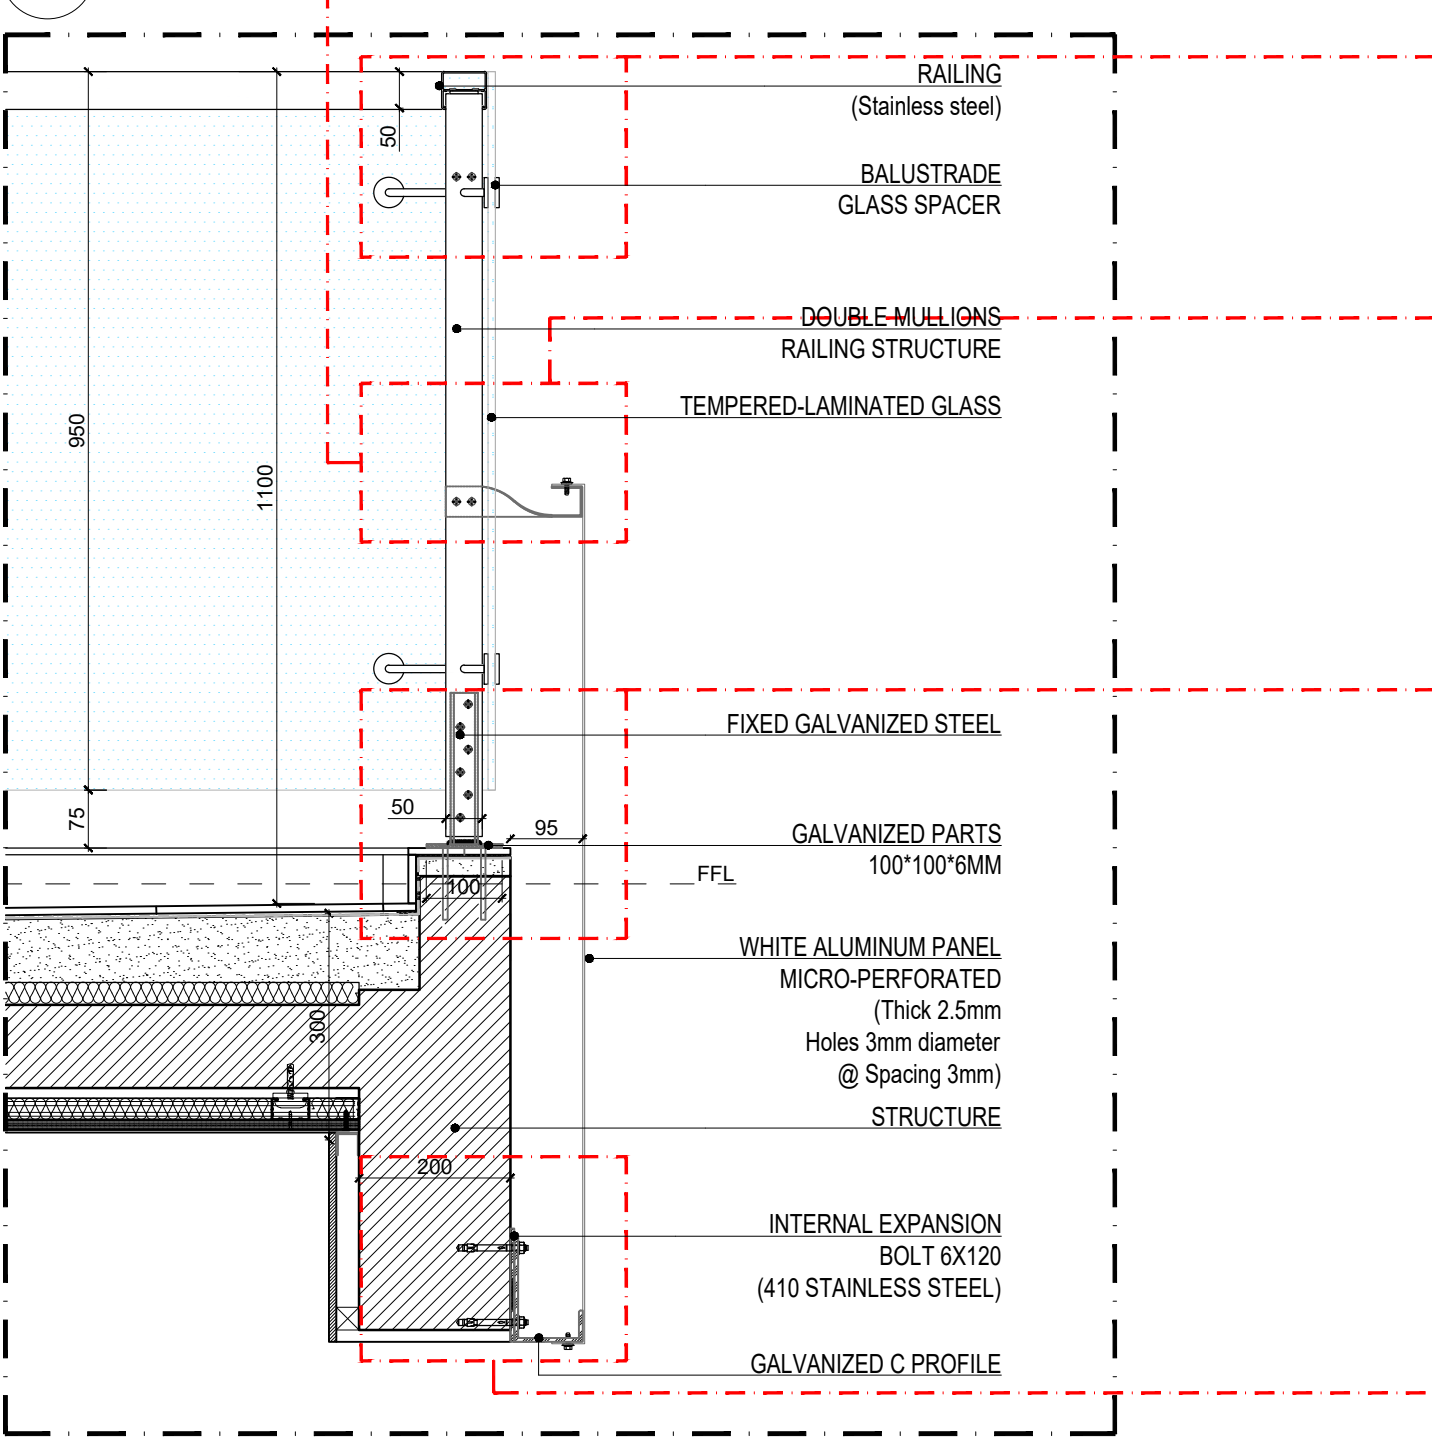


1a Section AA
SCALE: 1:10

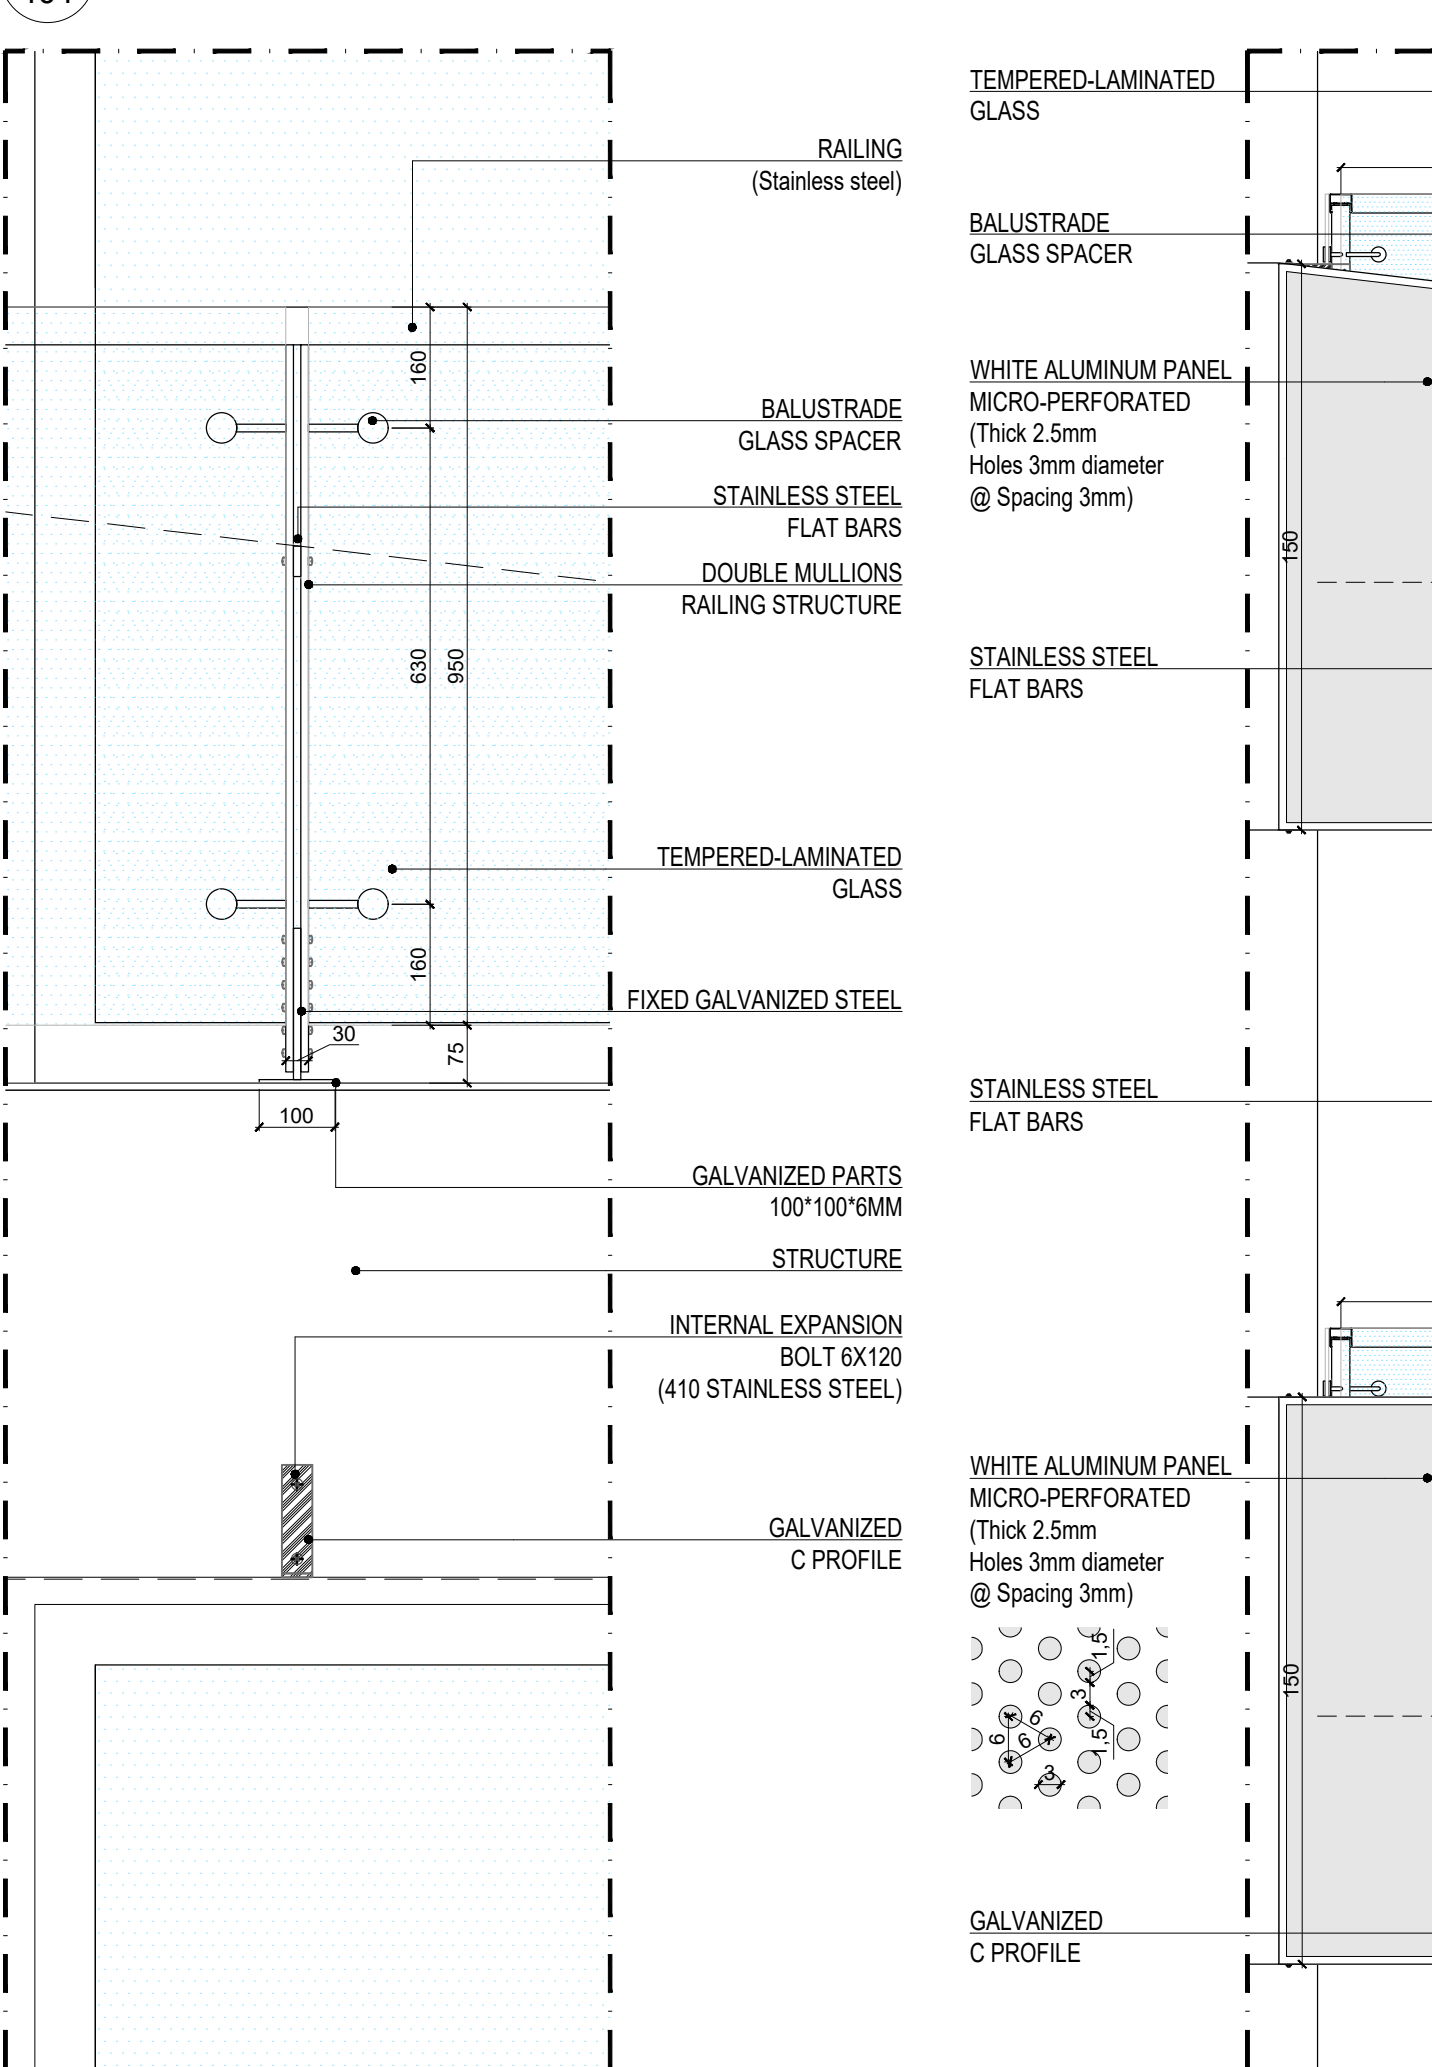


2 Section BB
SCALE: 1:10

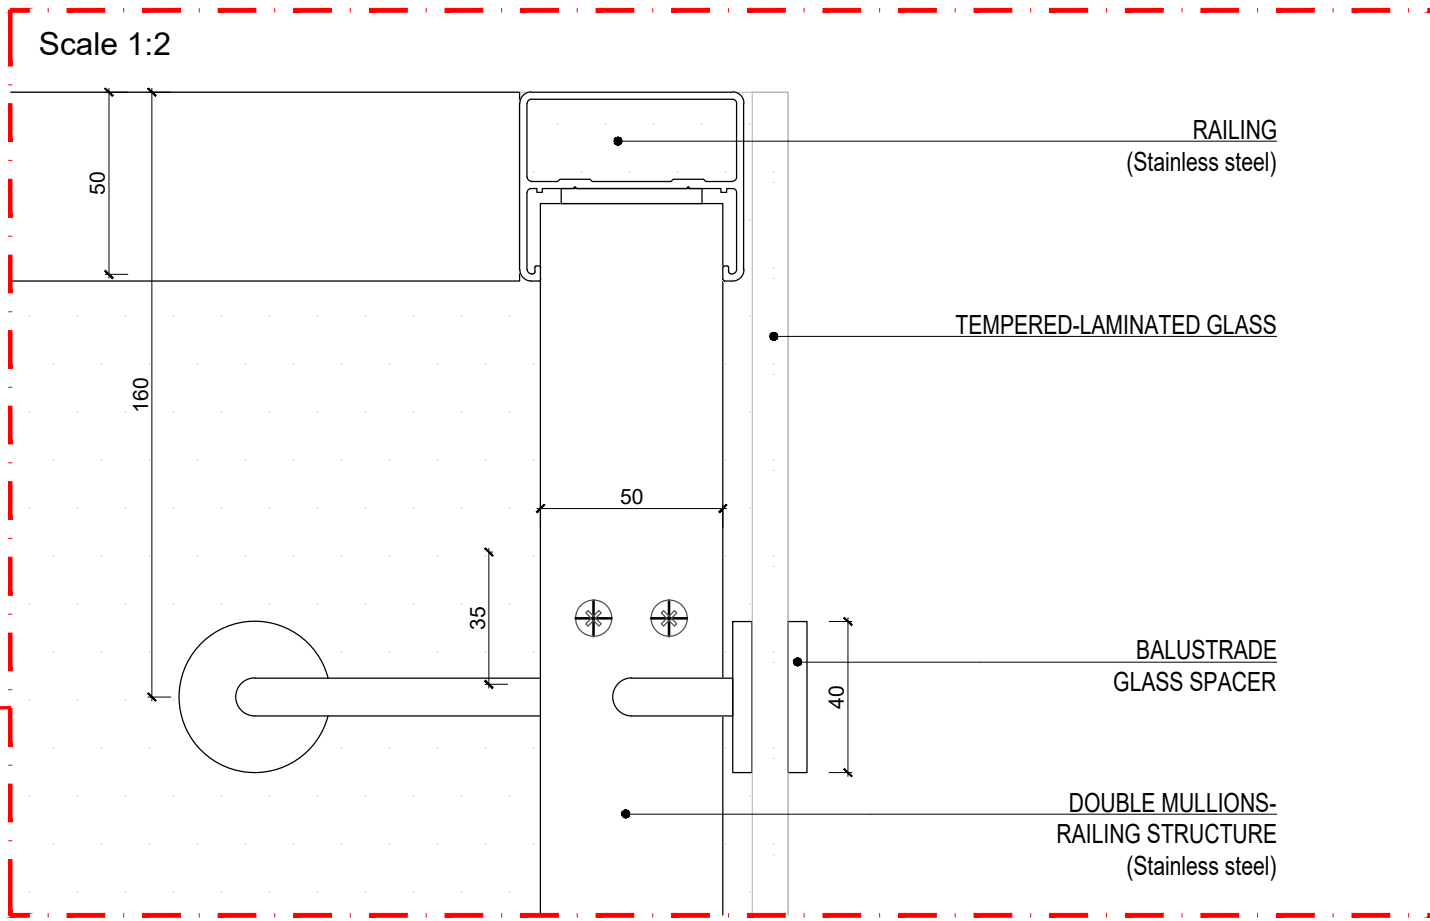


Scale 1:2

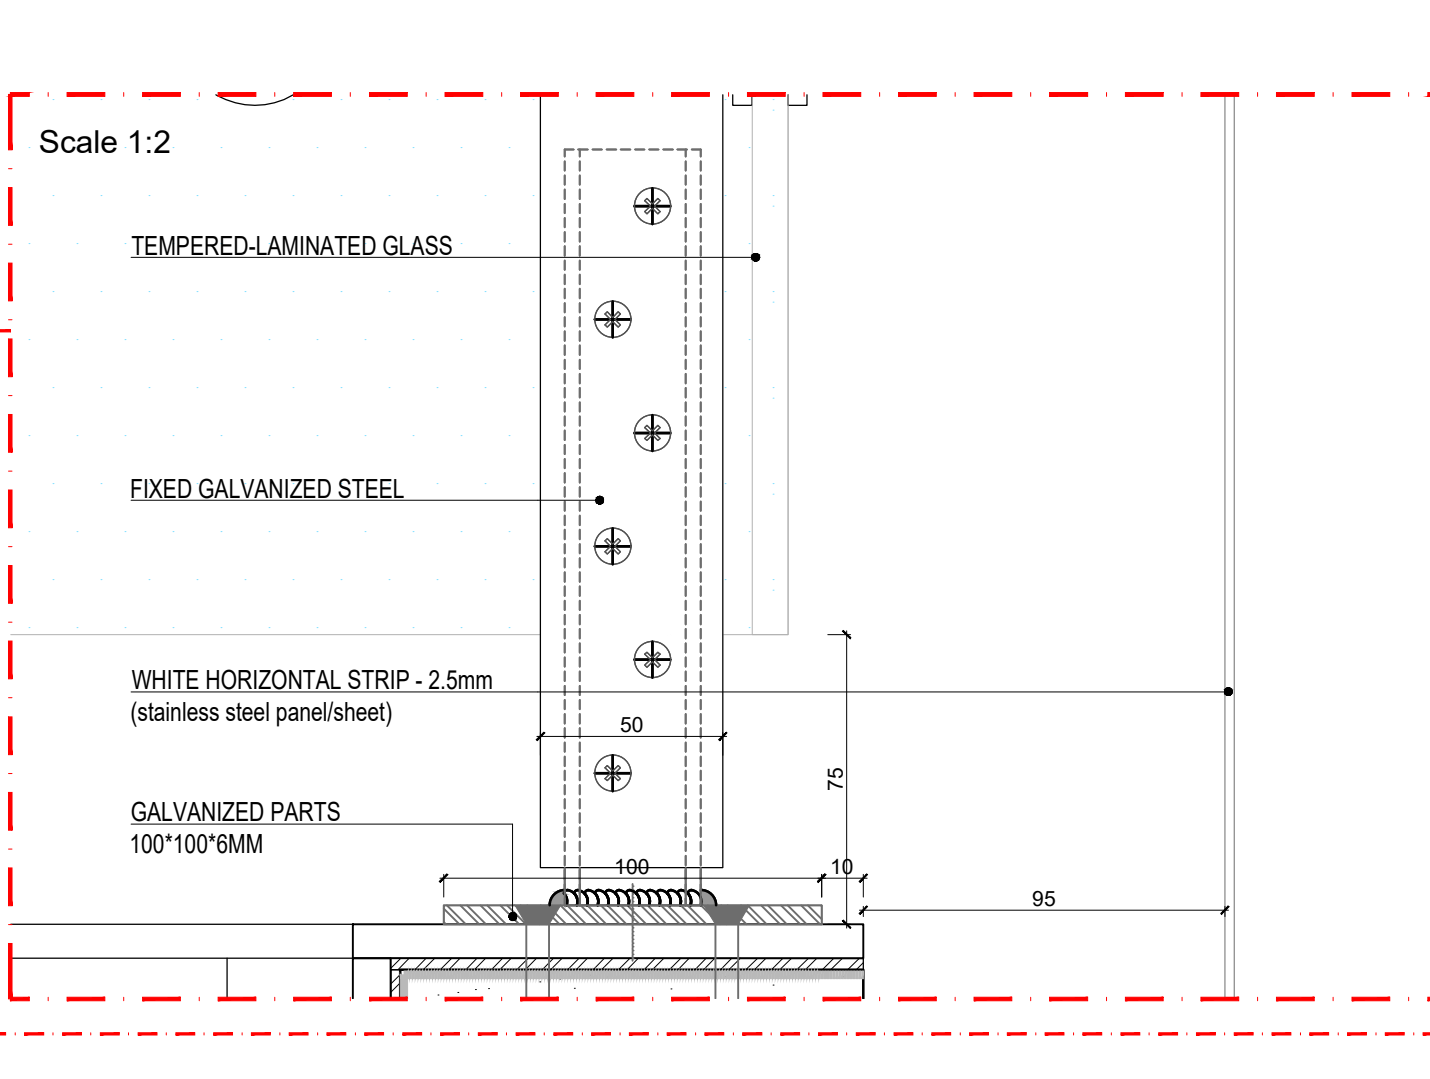


1b Section AA
SCALE: 1:2

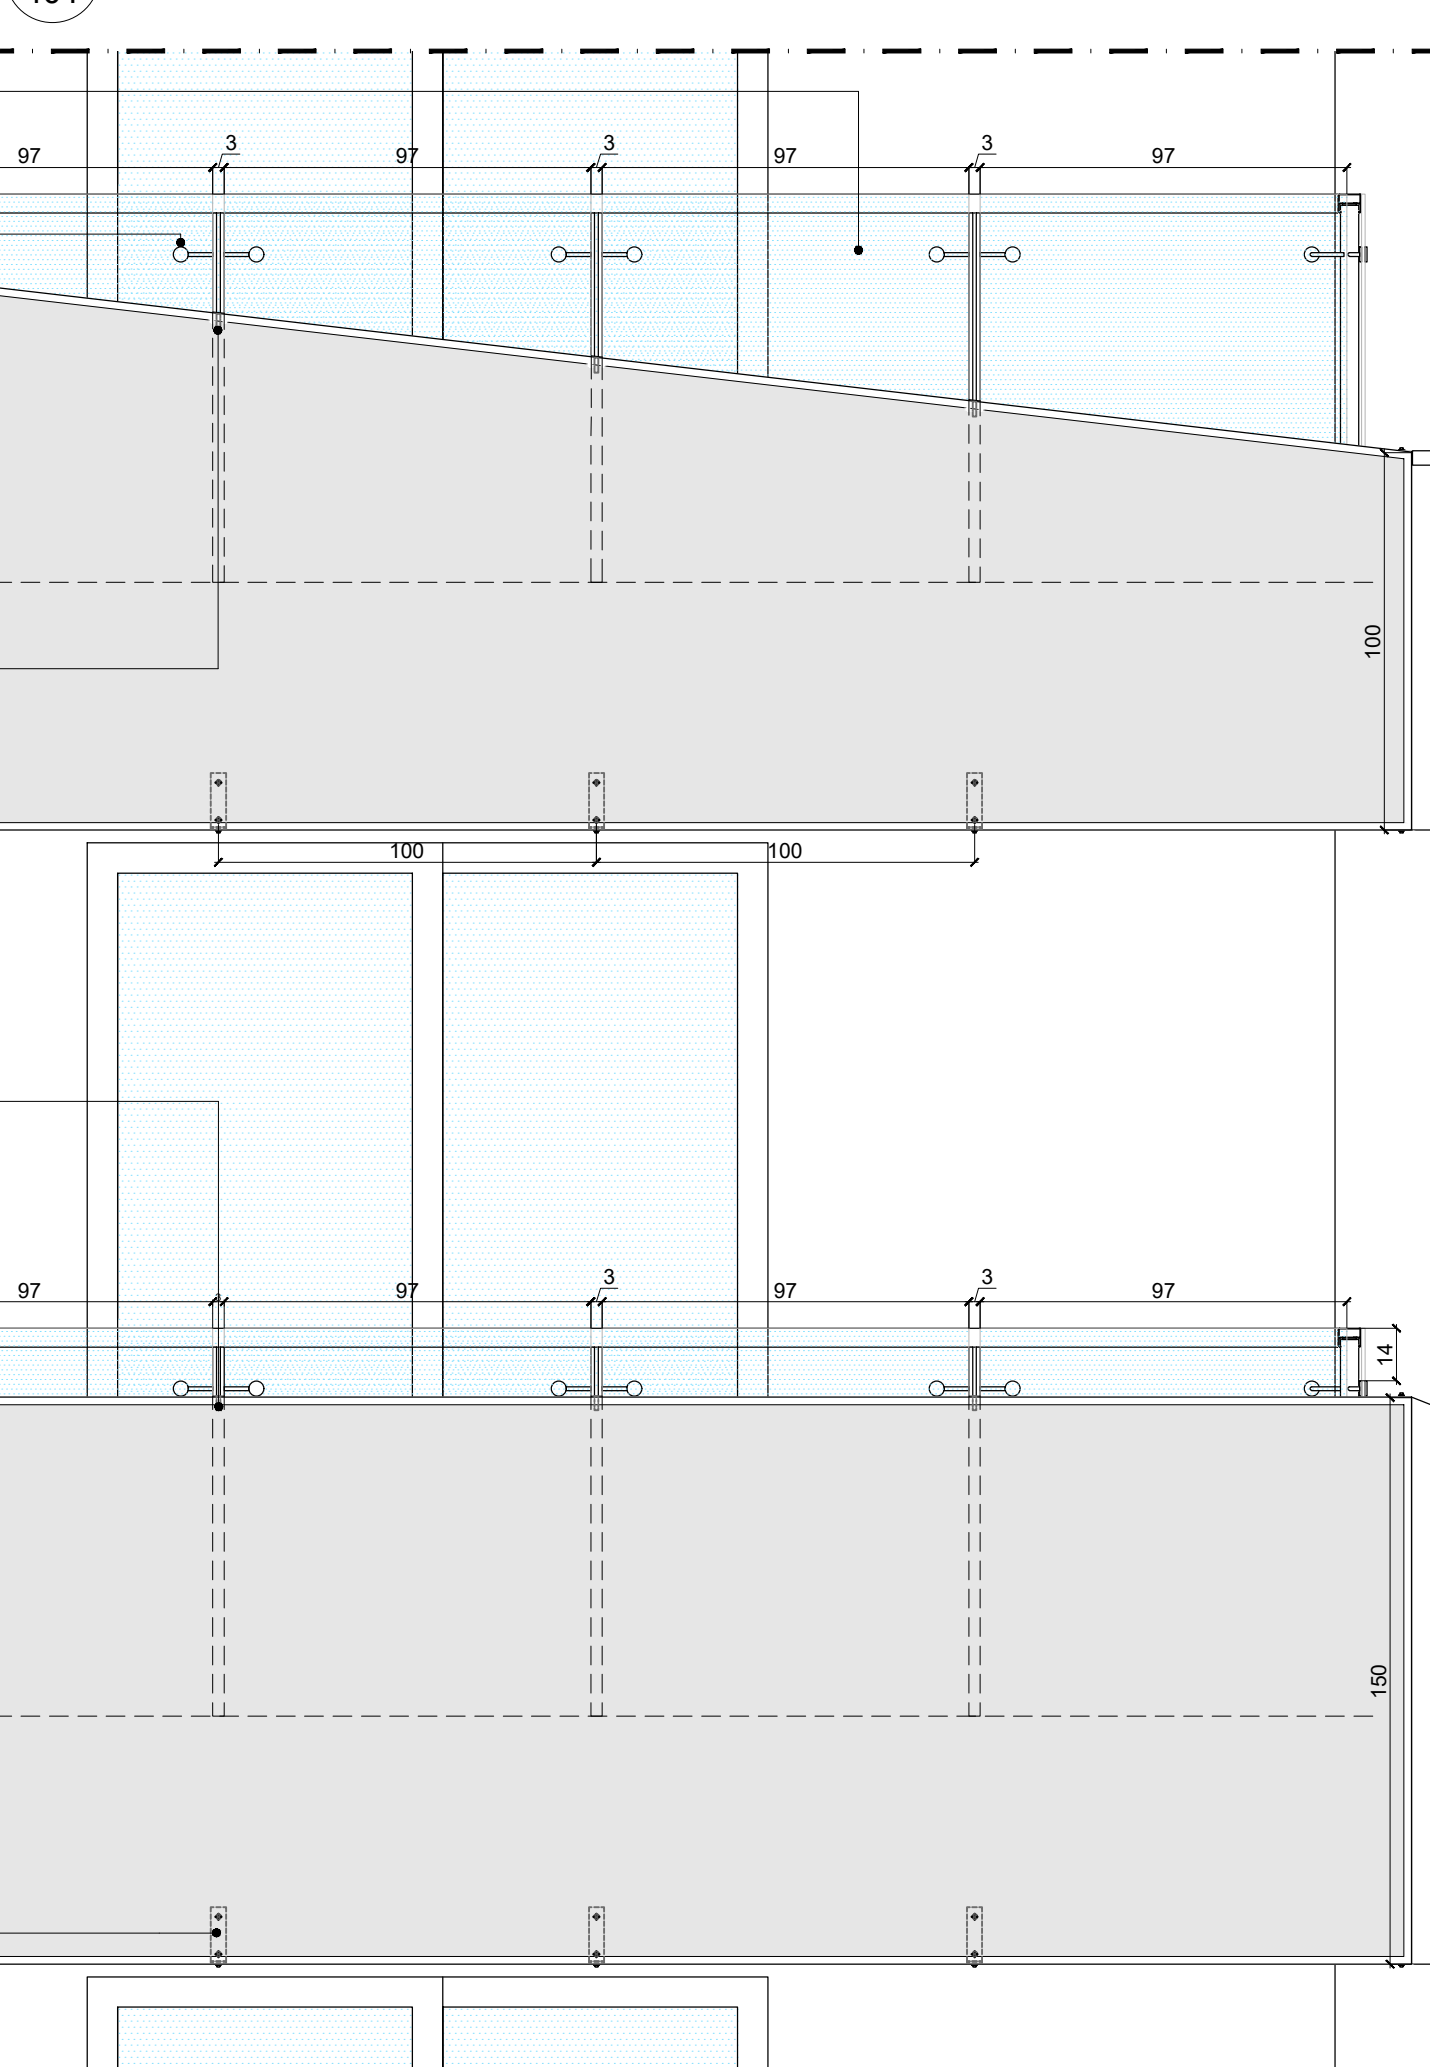


3 Elevation Typical balcony
SCALE: 1:20

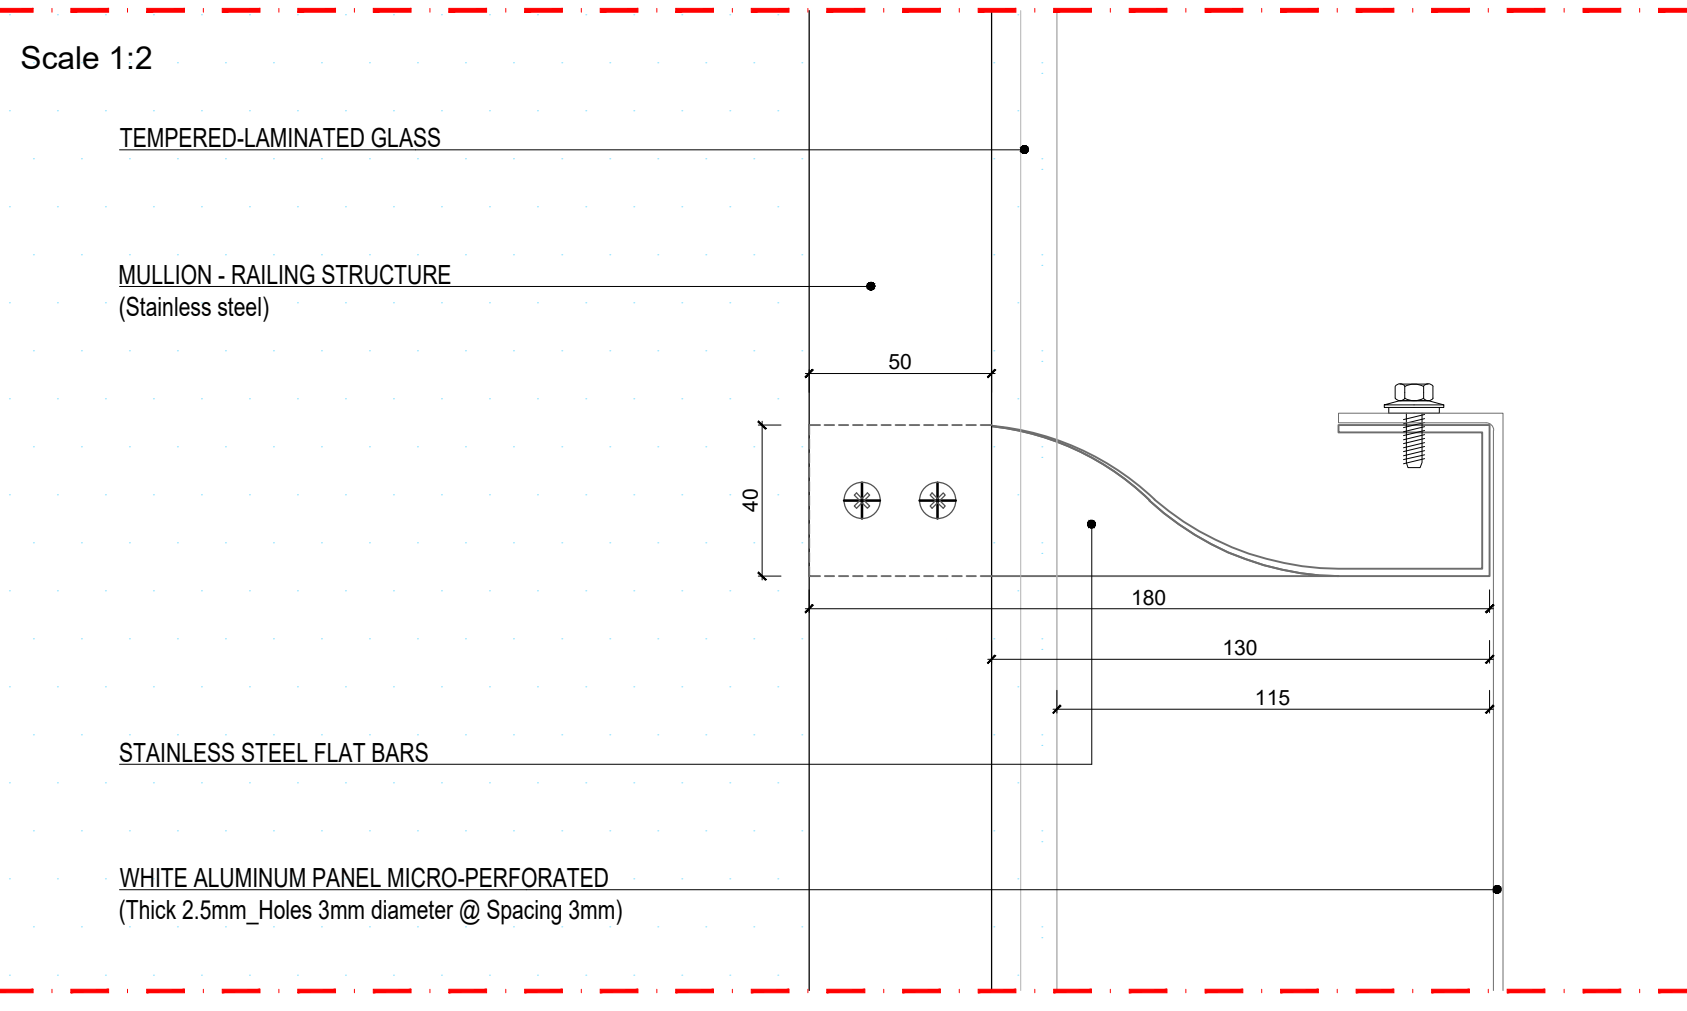


Scale 1:2

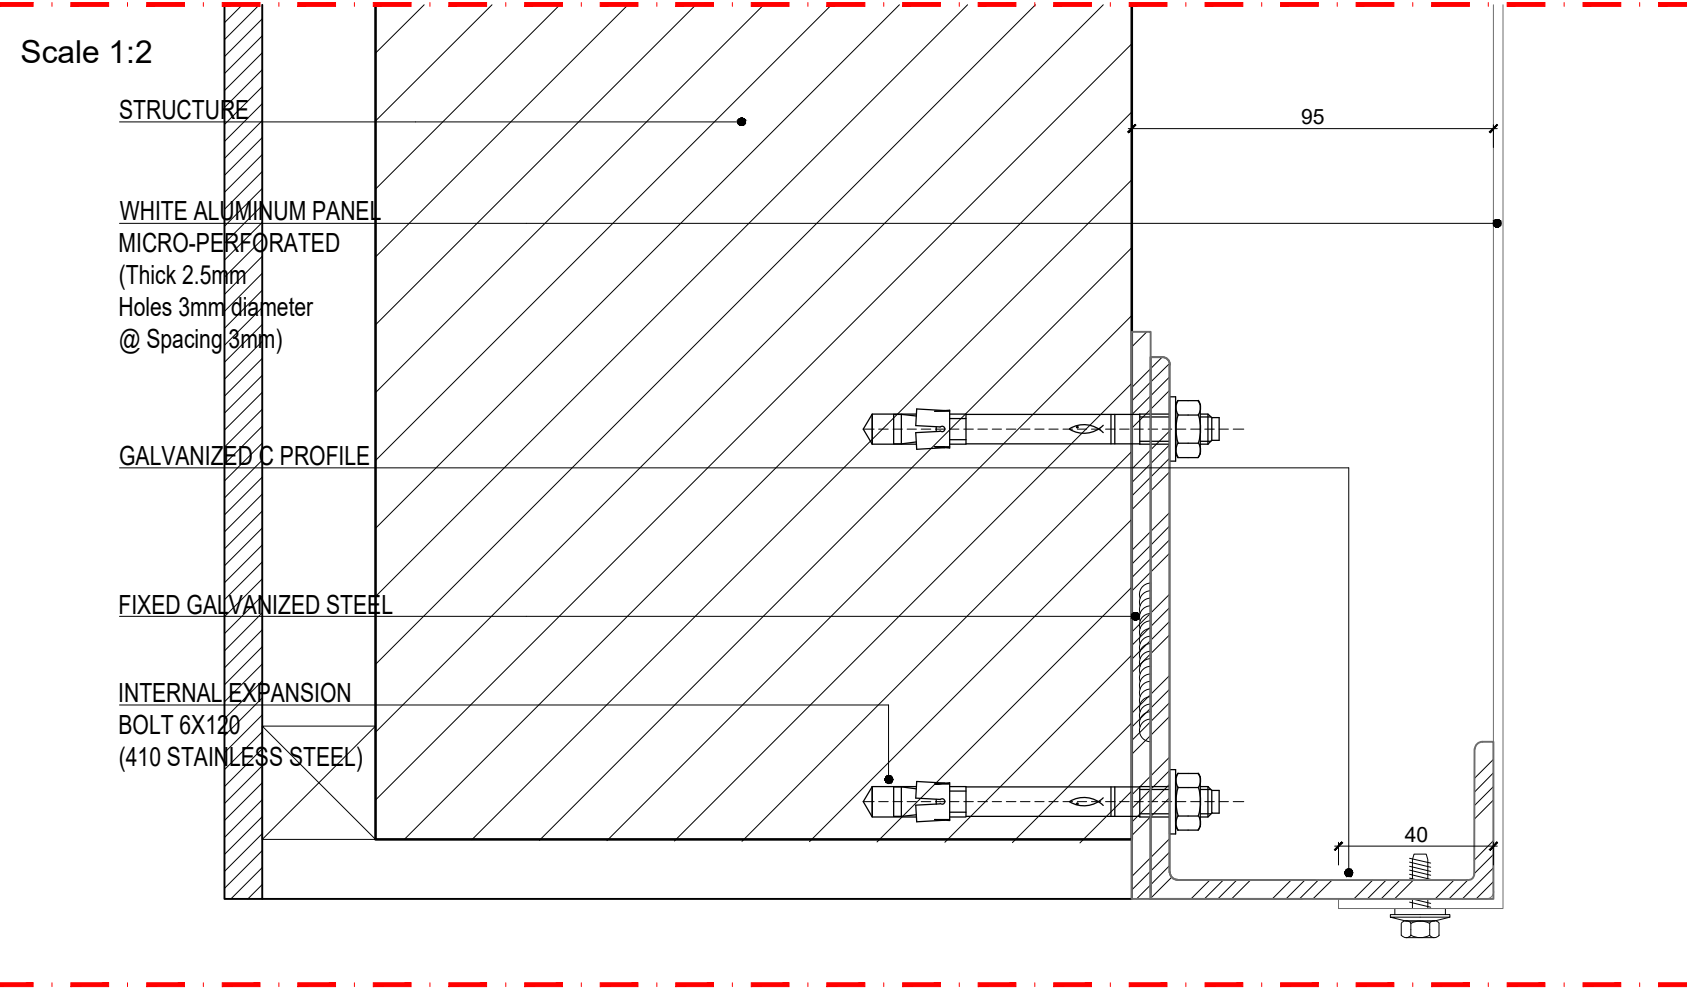


Scale 1:2

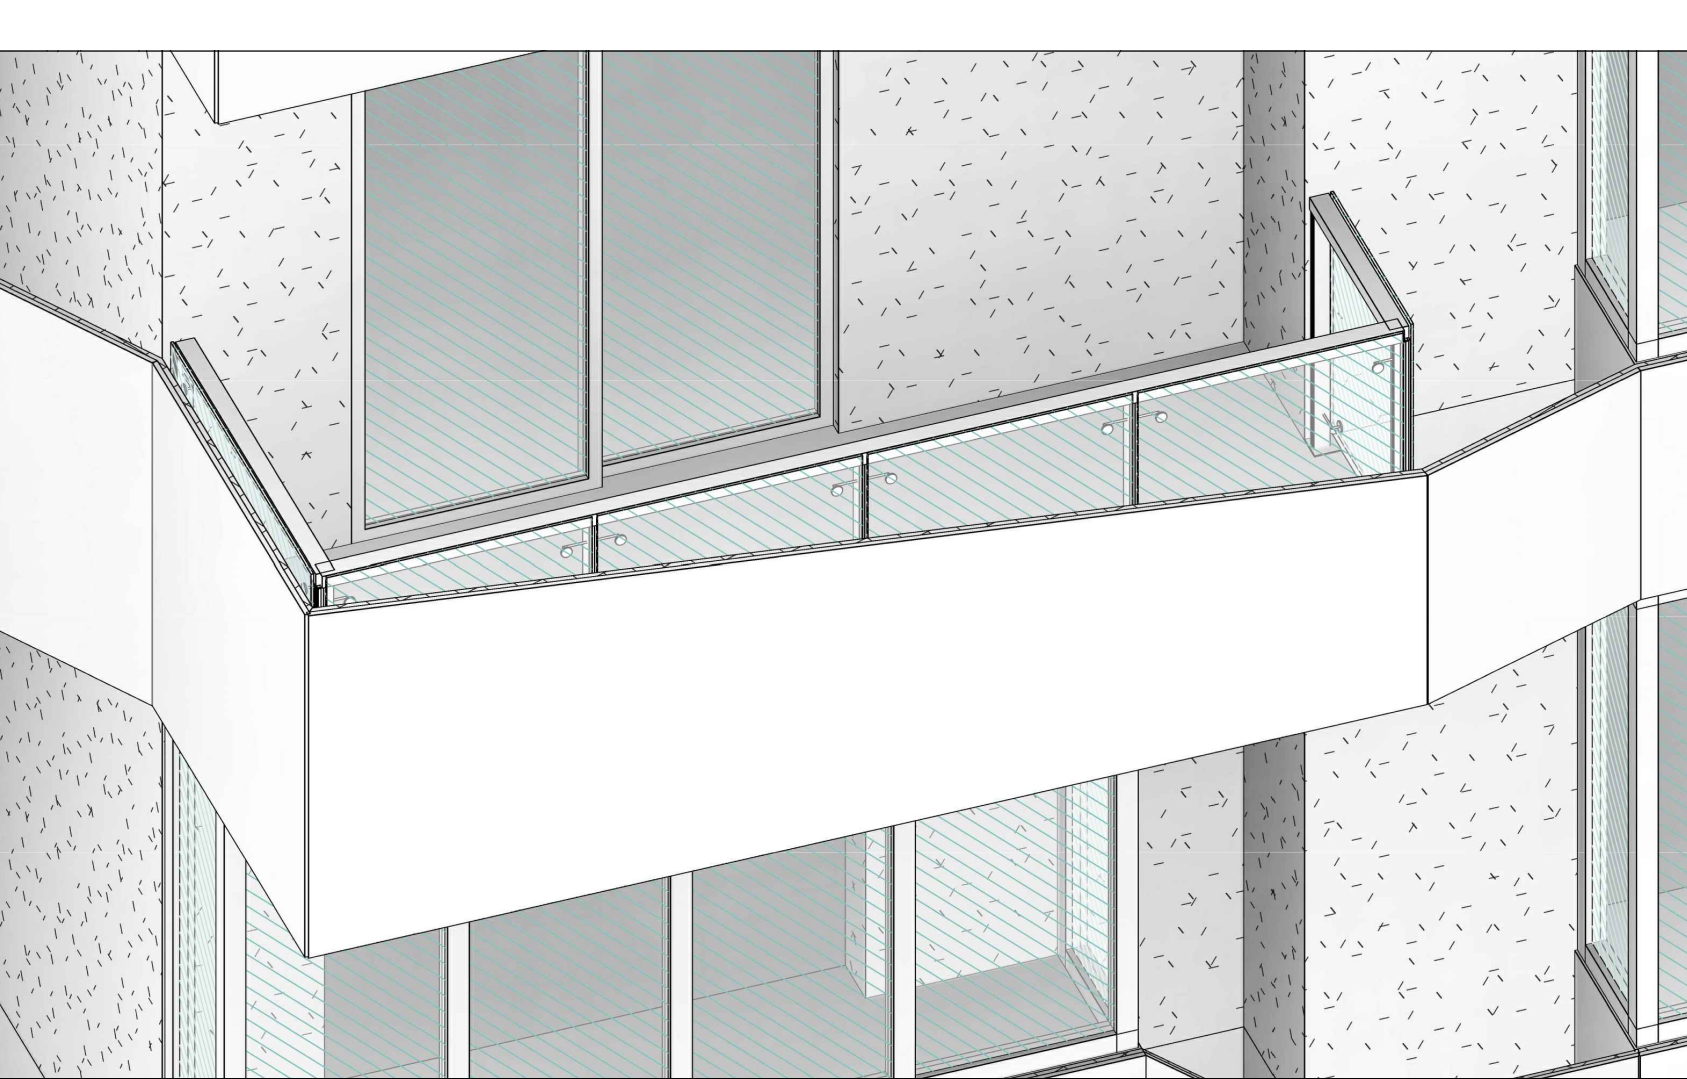

5 3D View Typical balcony
SCALE:

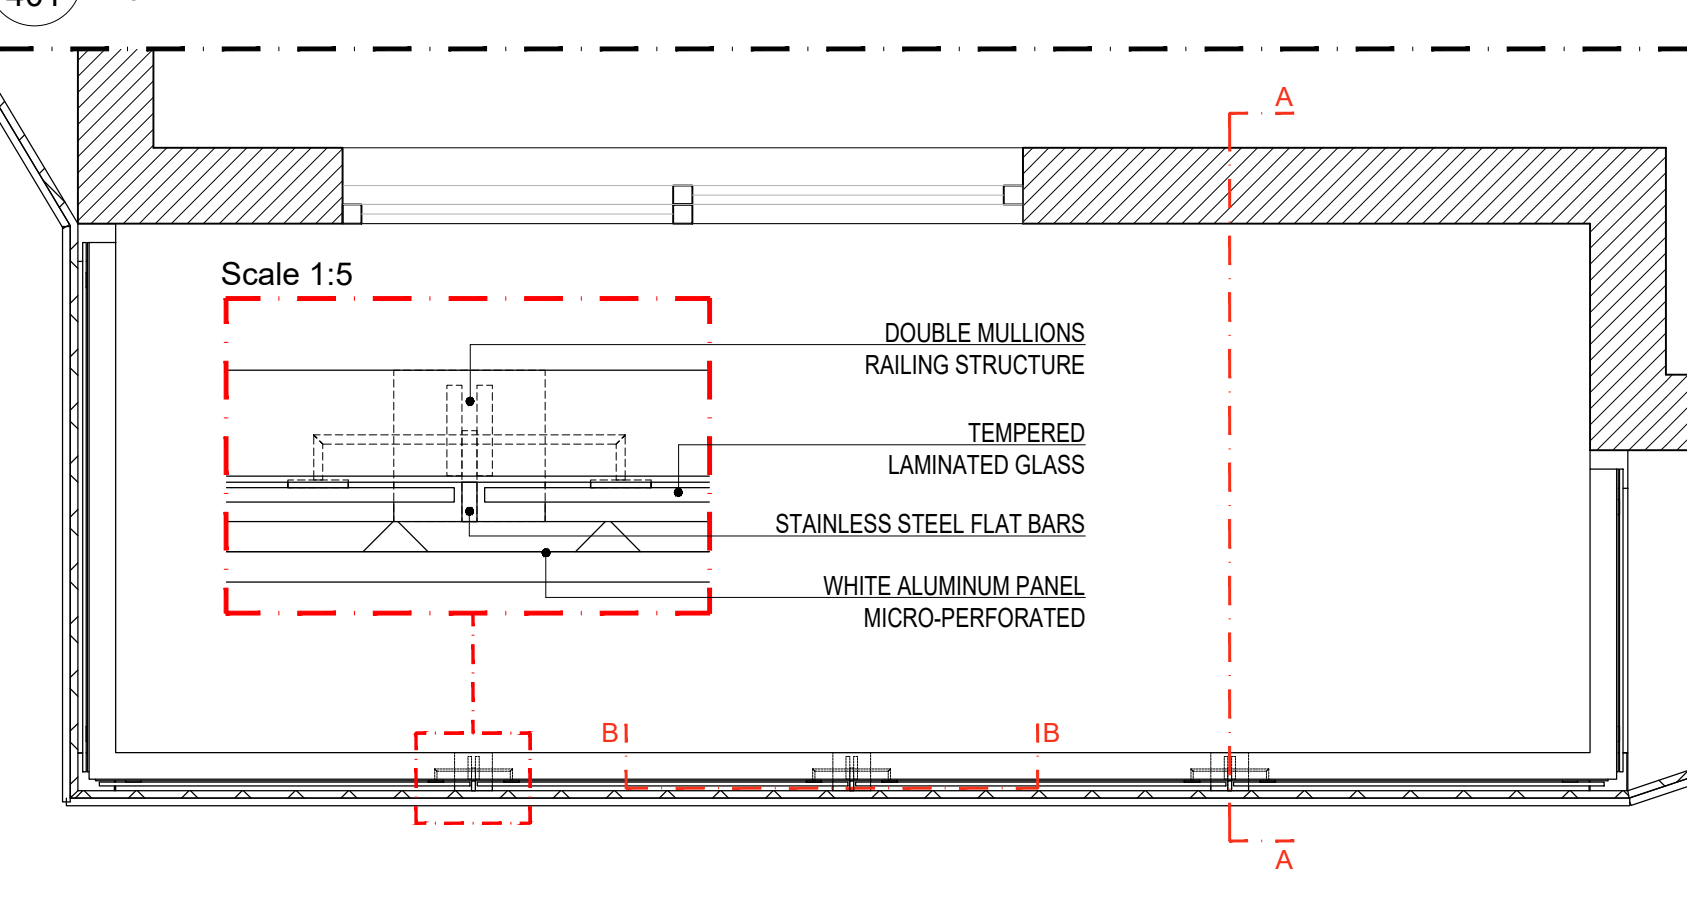

4 Plan Typical balcony
SCALE: 1:20

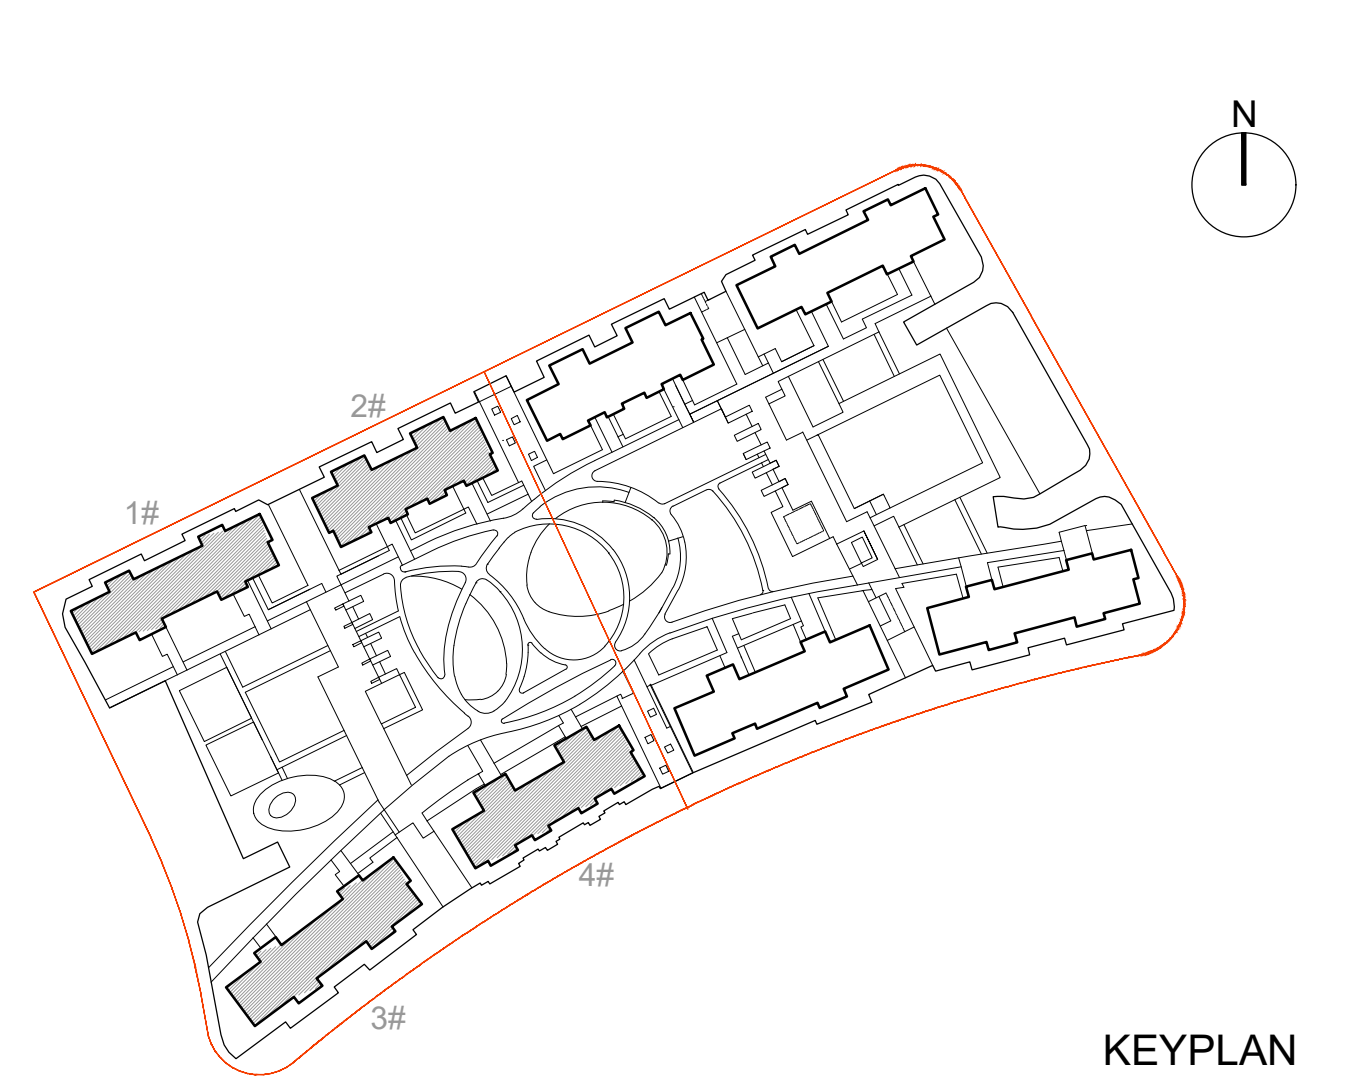

GENERAL NOTES:

A. ALL DIMENSIONS GIVEN ON THIS DRAWING ARE IN MILLIMETERS. DO NOT SCALE THE DRAWINGS. ANY DISCREPANCIES FOUND SHOULD BE REPORTED TO THE RESPONSIBLE ARCHITECT OR ENGINEER IMMEDIATELY.

B. IT IS THE RESPONSIBILITY OF THE CONTRACTOR OR BUILDERS TO ASCERTAIN AND CONFIRM THAT ALL DIMENSIONS SHOWN IN THESE DRAWINGS SHALL COMPLY WITH THE SITE DIMENSIONS AND LEVELS PRIOR TO PREPARING DRAWINGS AND EXECUTING THE WORKS.

C. ALL MEASUREMENT MUST BE VERIFIED AND CONFIRMED AT CONSTRUCTION SITE.

D. ALL WORKS ARE TO BE CARRIED OUT TO LOCAL CODES OF CONSTRUCTIONS.

E. THIS DRAWINGS SHOULD BE READ IN CONJUNCTION WITH THE OTHER RELEVANT ARCHITECTURAL, STRUCTURAL, MECHANICAL AND ELECTRICAL DRAWINGS AND ALL RELEVANT SECTIONS OF THE SPECIFICATIONS.

F. EXACT LOCATION, SIZES AND DETAILS OF ELECTRO-MECHANICAL WALL OPENINGS SHALL BE COORDINATED WITH ELECTRO-MECHANICAL ENGINEERS.

G. DIMENSION AND LOCATION OF SERVICES SHALL BE COORDINATED WITH RESPECTIVE ARCHITECTURAL AND SERVICES DRAWINGS PRIOR TO COMMENCEMENT OF ANY WORK. ANY DISCREPANCY FOUND SHOULD BE BROUGHT TO THE NOTICE OF THE CONCERNED ENGINEER.

H. ALL MATERIALS MUST BE VERIFIED AND CONFIRMED BY PEIA ASSOCIATI SRL ON SHOP DRAWINGS AND SAMPLES BY CONTRACTOR.

I. REFER TO SCHEDULE OF FINISHES FOR FLOORS, WALLS AND CEILINGS.

J. ALL MATERIAL FINISHES AND WORKMANSHIP SHOULD BE OF HIGH STANDARD QUALITY OF WORKS.

K. ALL TEXTURES AND COLORS SHOULD BE REFERED TO SCHEDULE OF FINISHES AND HAVE APPROVAL OF ARCHITECT.

LEGEND:

F.F.L. = FLOOR FINISHING LEVEL

Architect:	Peia associati srl Via Cadolini, 30 - 20137 Milano, Italy Tel: +39 02 6598647 Fax: +39 02 36554984 e-mail: info@peiaassociati.it		
Engineering:	PEIA		
Owner:	Yanfull (Shanghai) Co. Ltd.		
Project:	ROYAL GARDEN PHASE 4 Shanghai, China		
Drawing Subject:	RG3_DETAIL_TYPICAL BALCONY SECTION		
Designed:	Peia Associati s.r.l.	Draft:	YV
Checked:	GP	Review:	01
Date:	2017-12-01	Scale:	vary @A1 (841x594mm)
ID Dwg:	1501_RG_RG4_DET_Details	Sheet No.:	401