




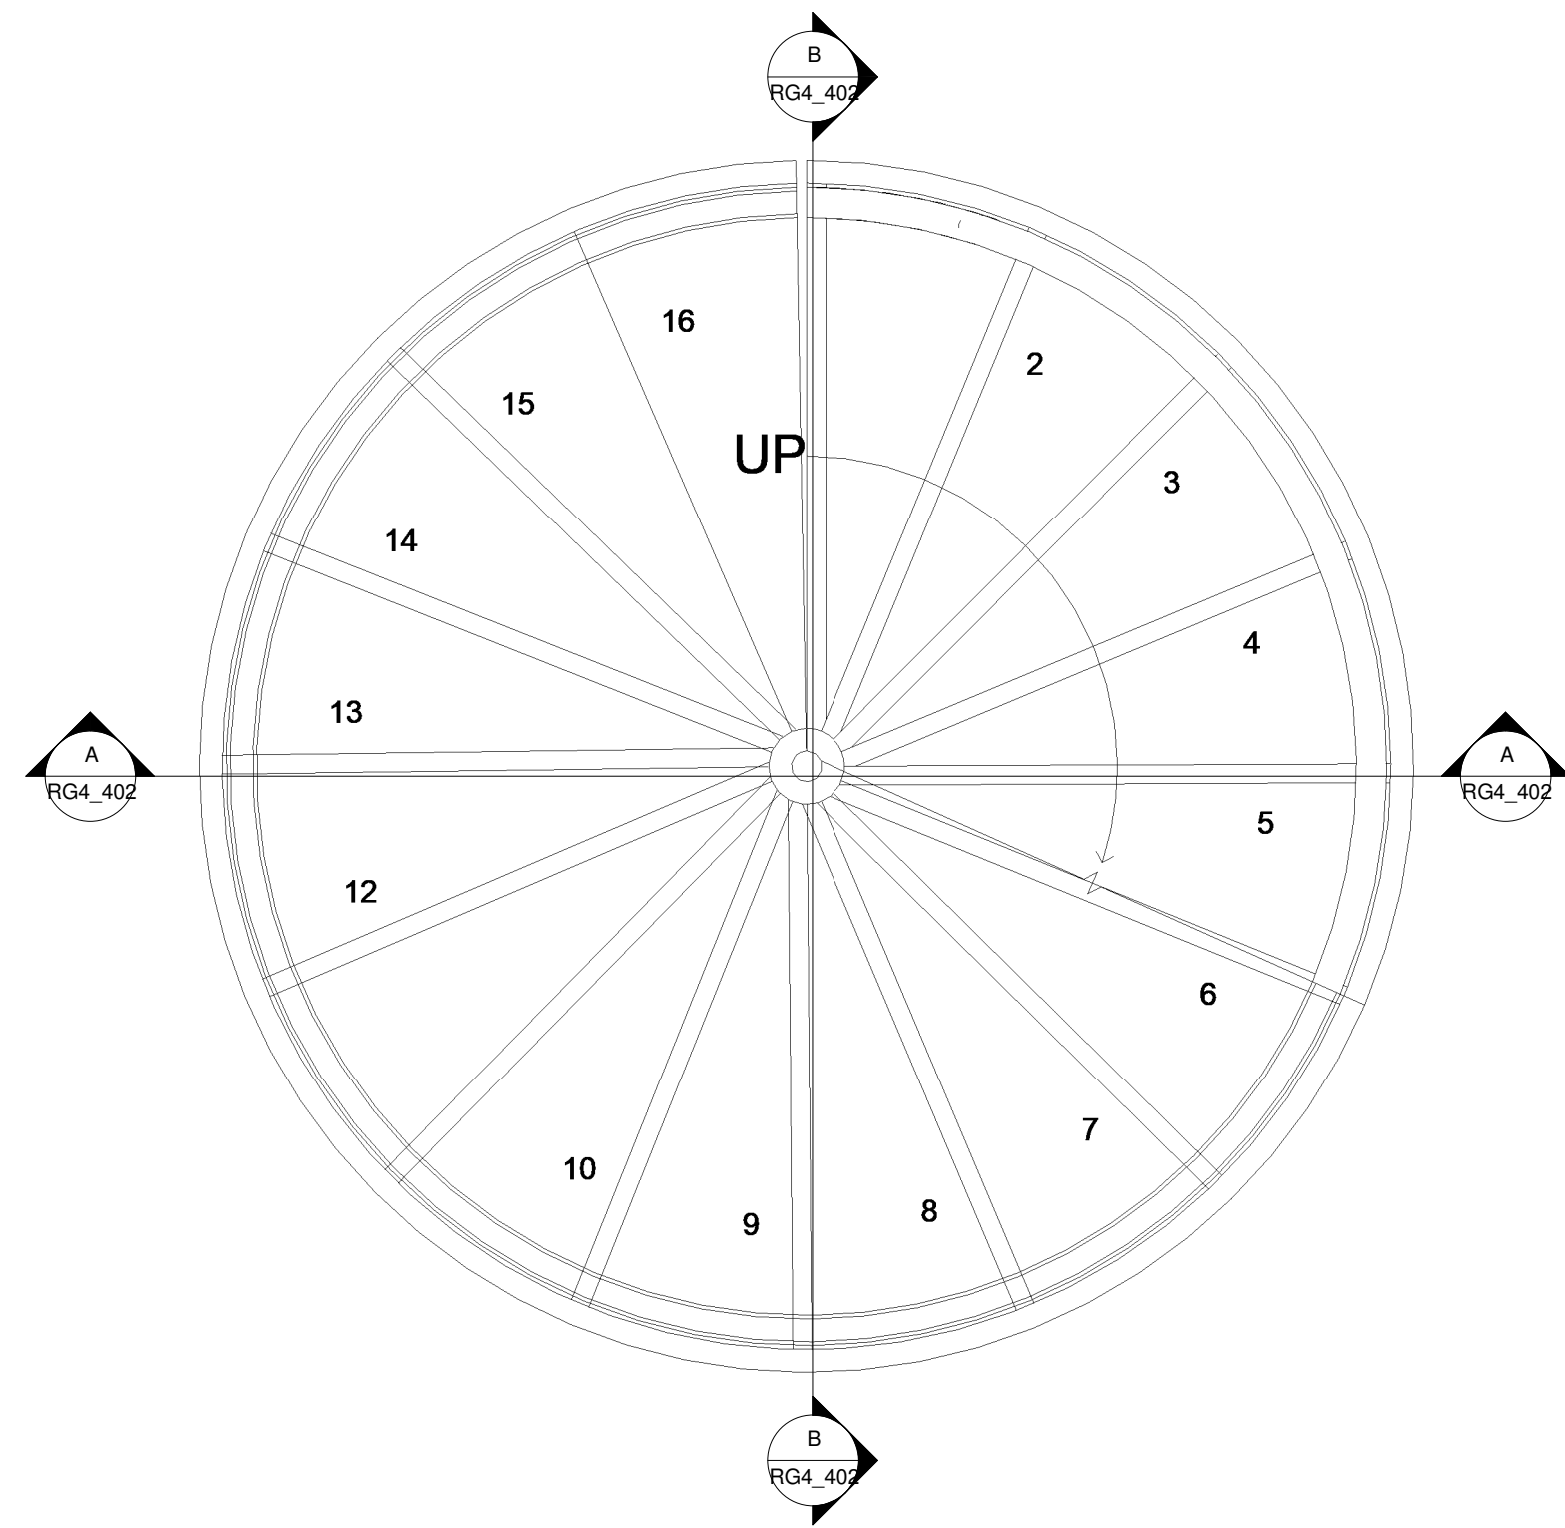


1 DETAIL ROOF STAIRCASE_PLAN
1 : 10

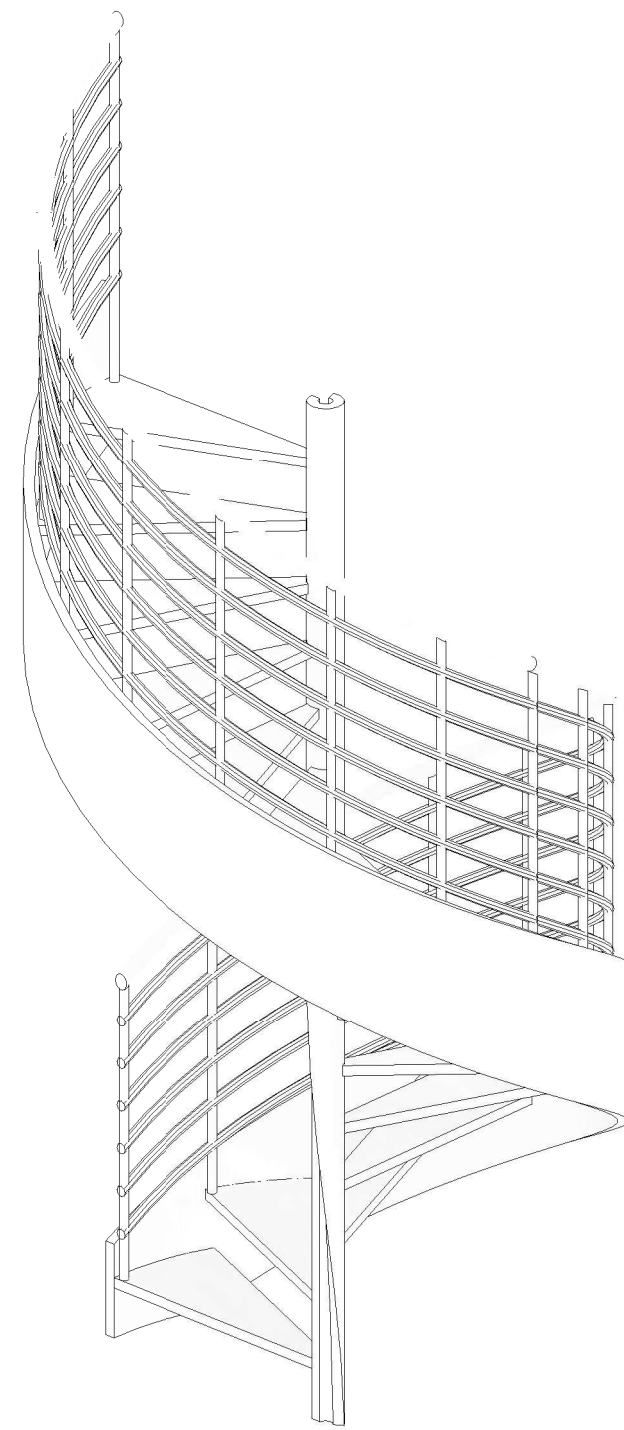


2 3D DETAIL ROOF STAIRCASE

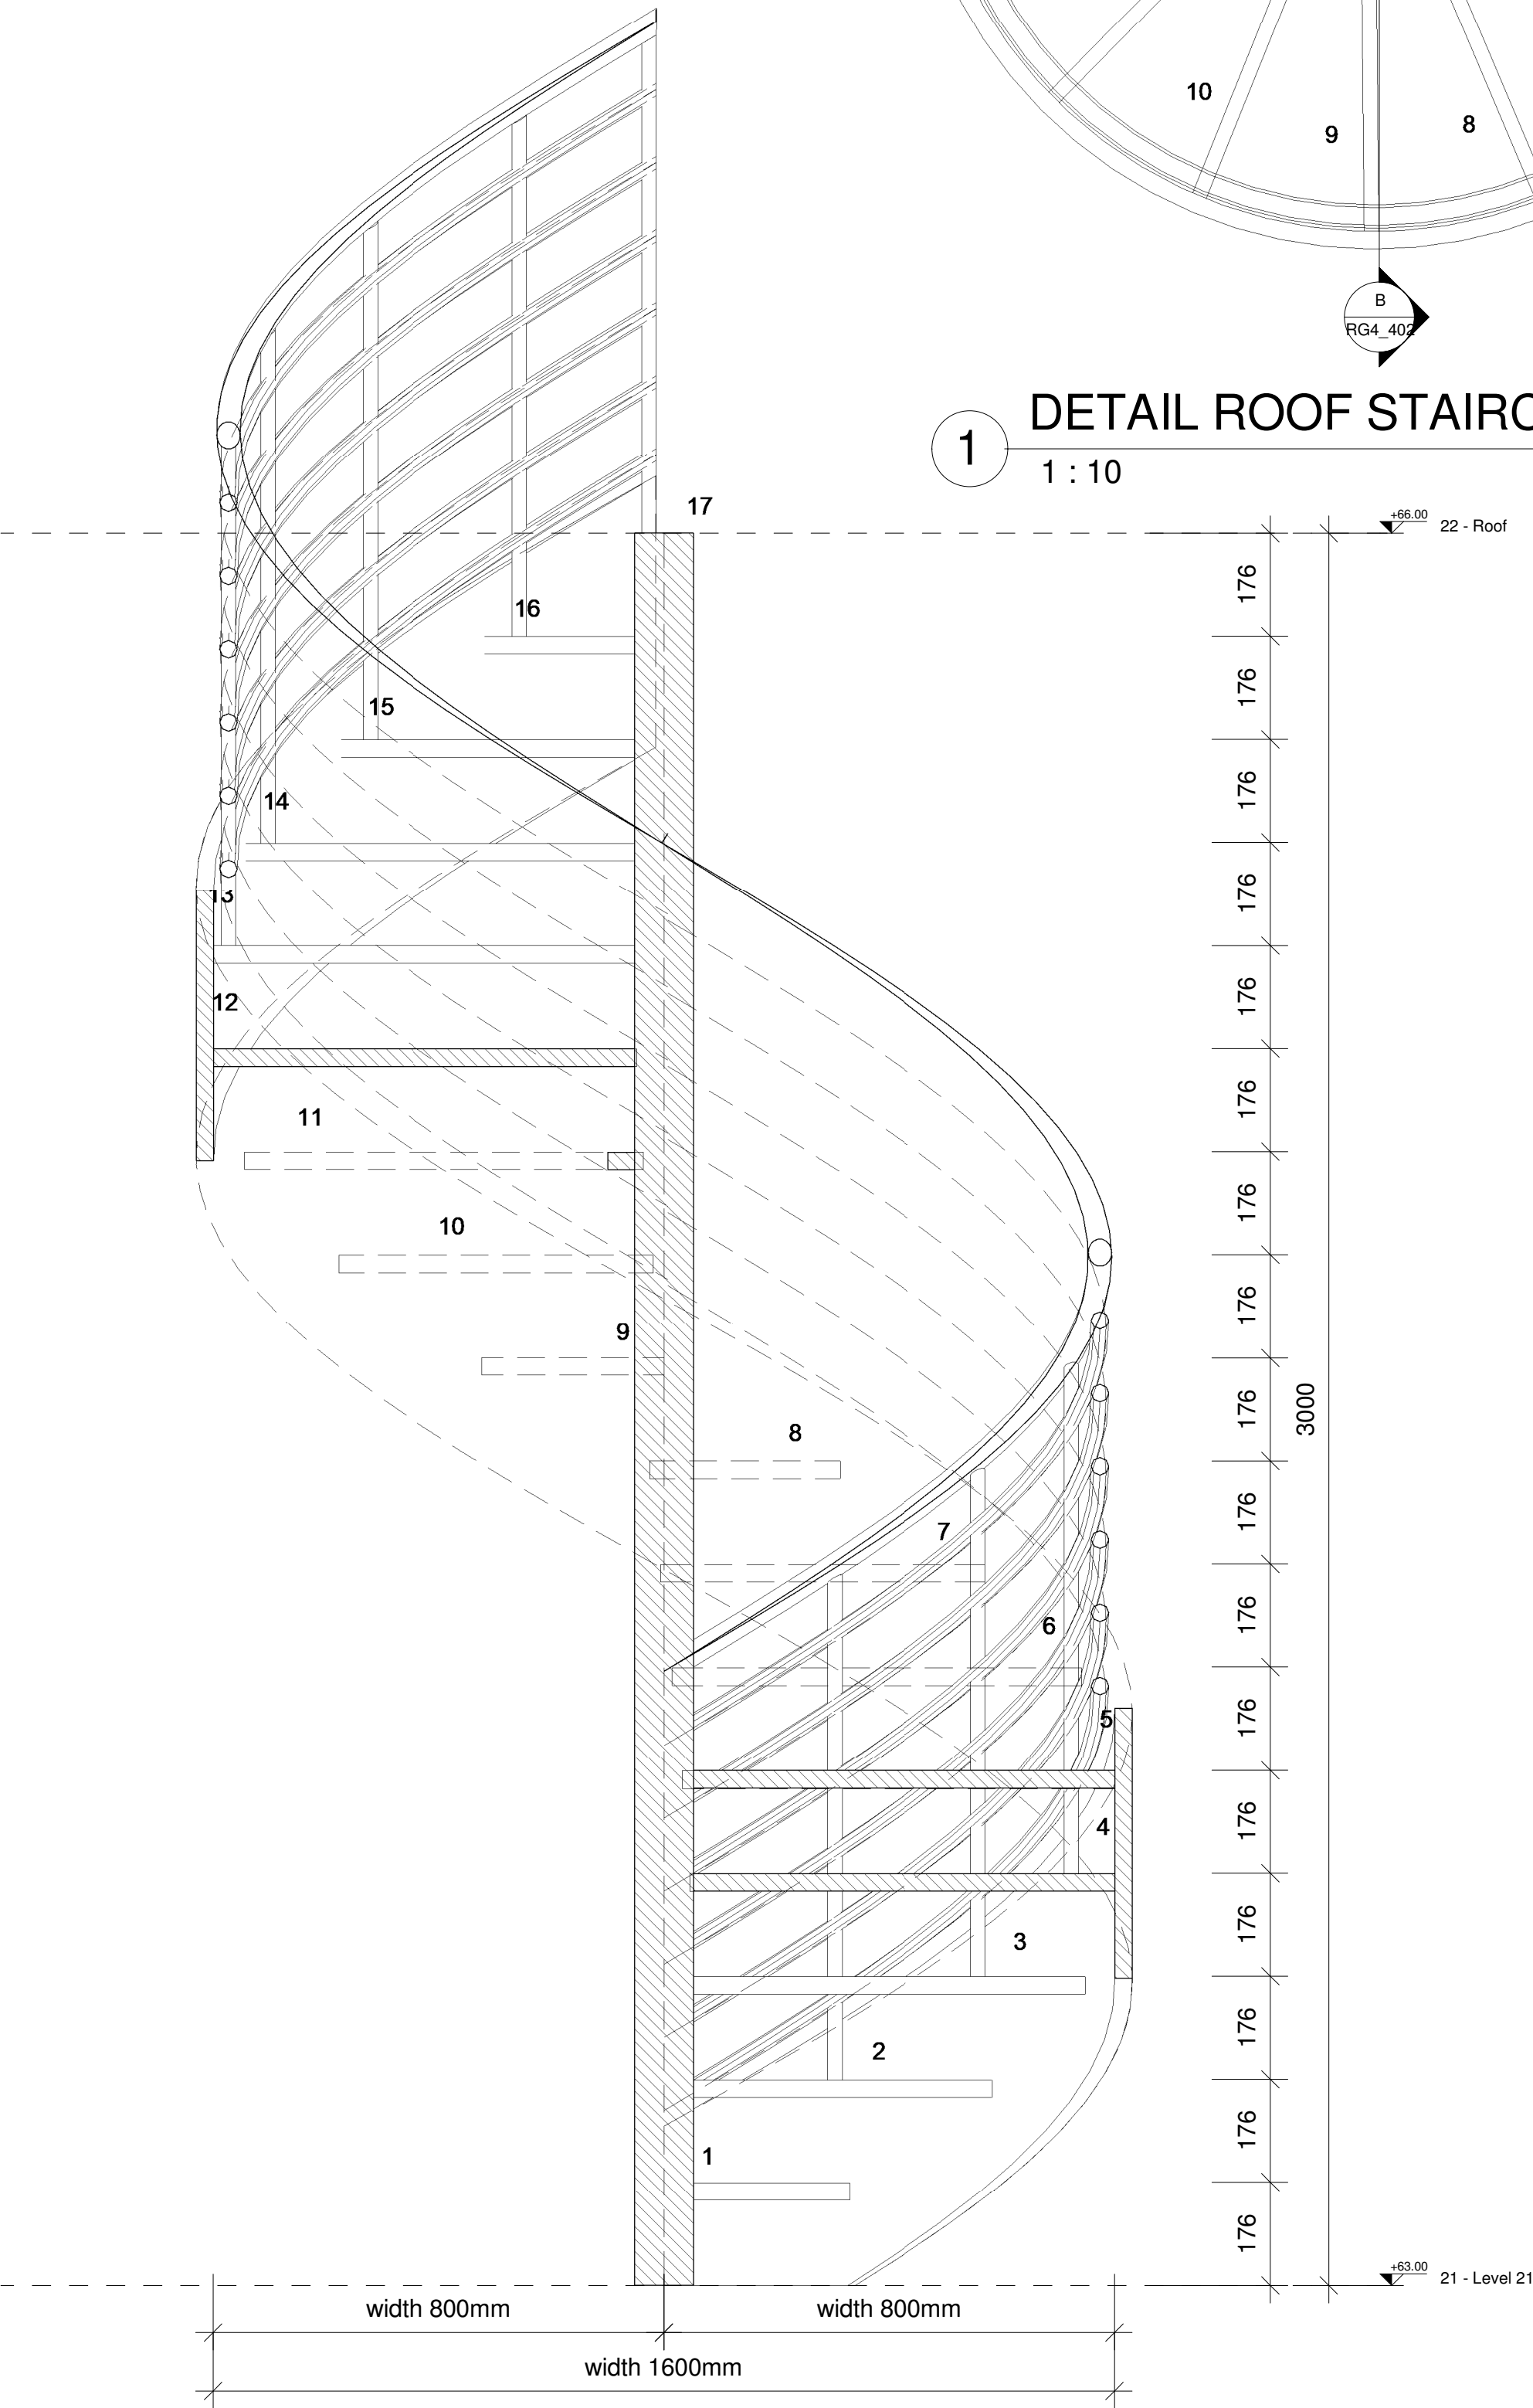


A Section AA
1 : 10

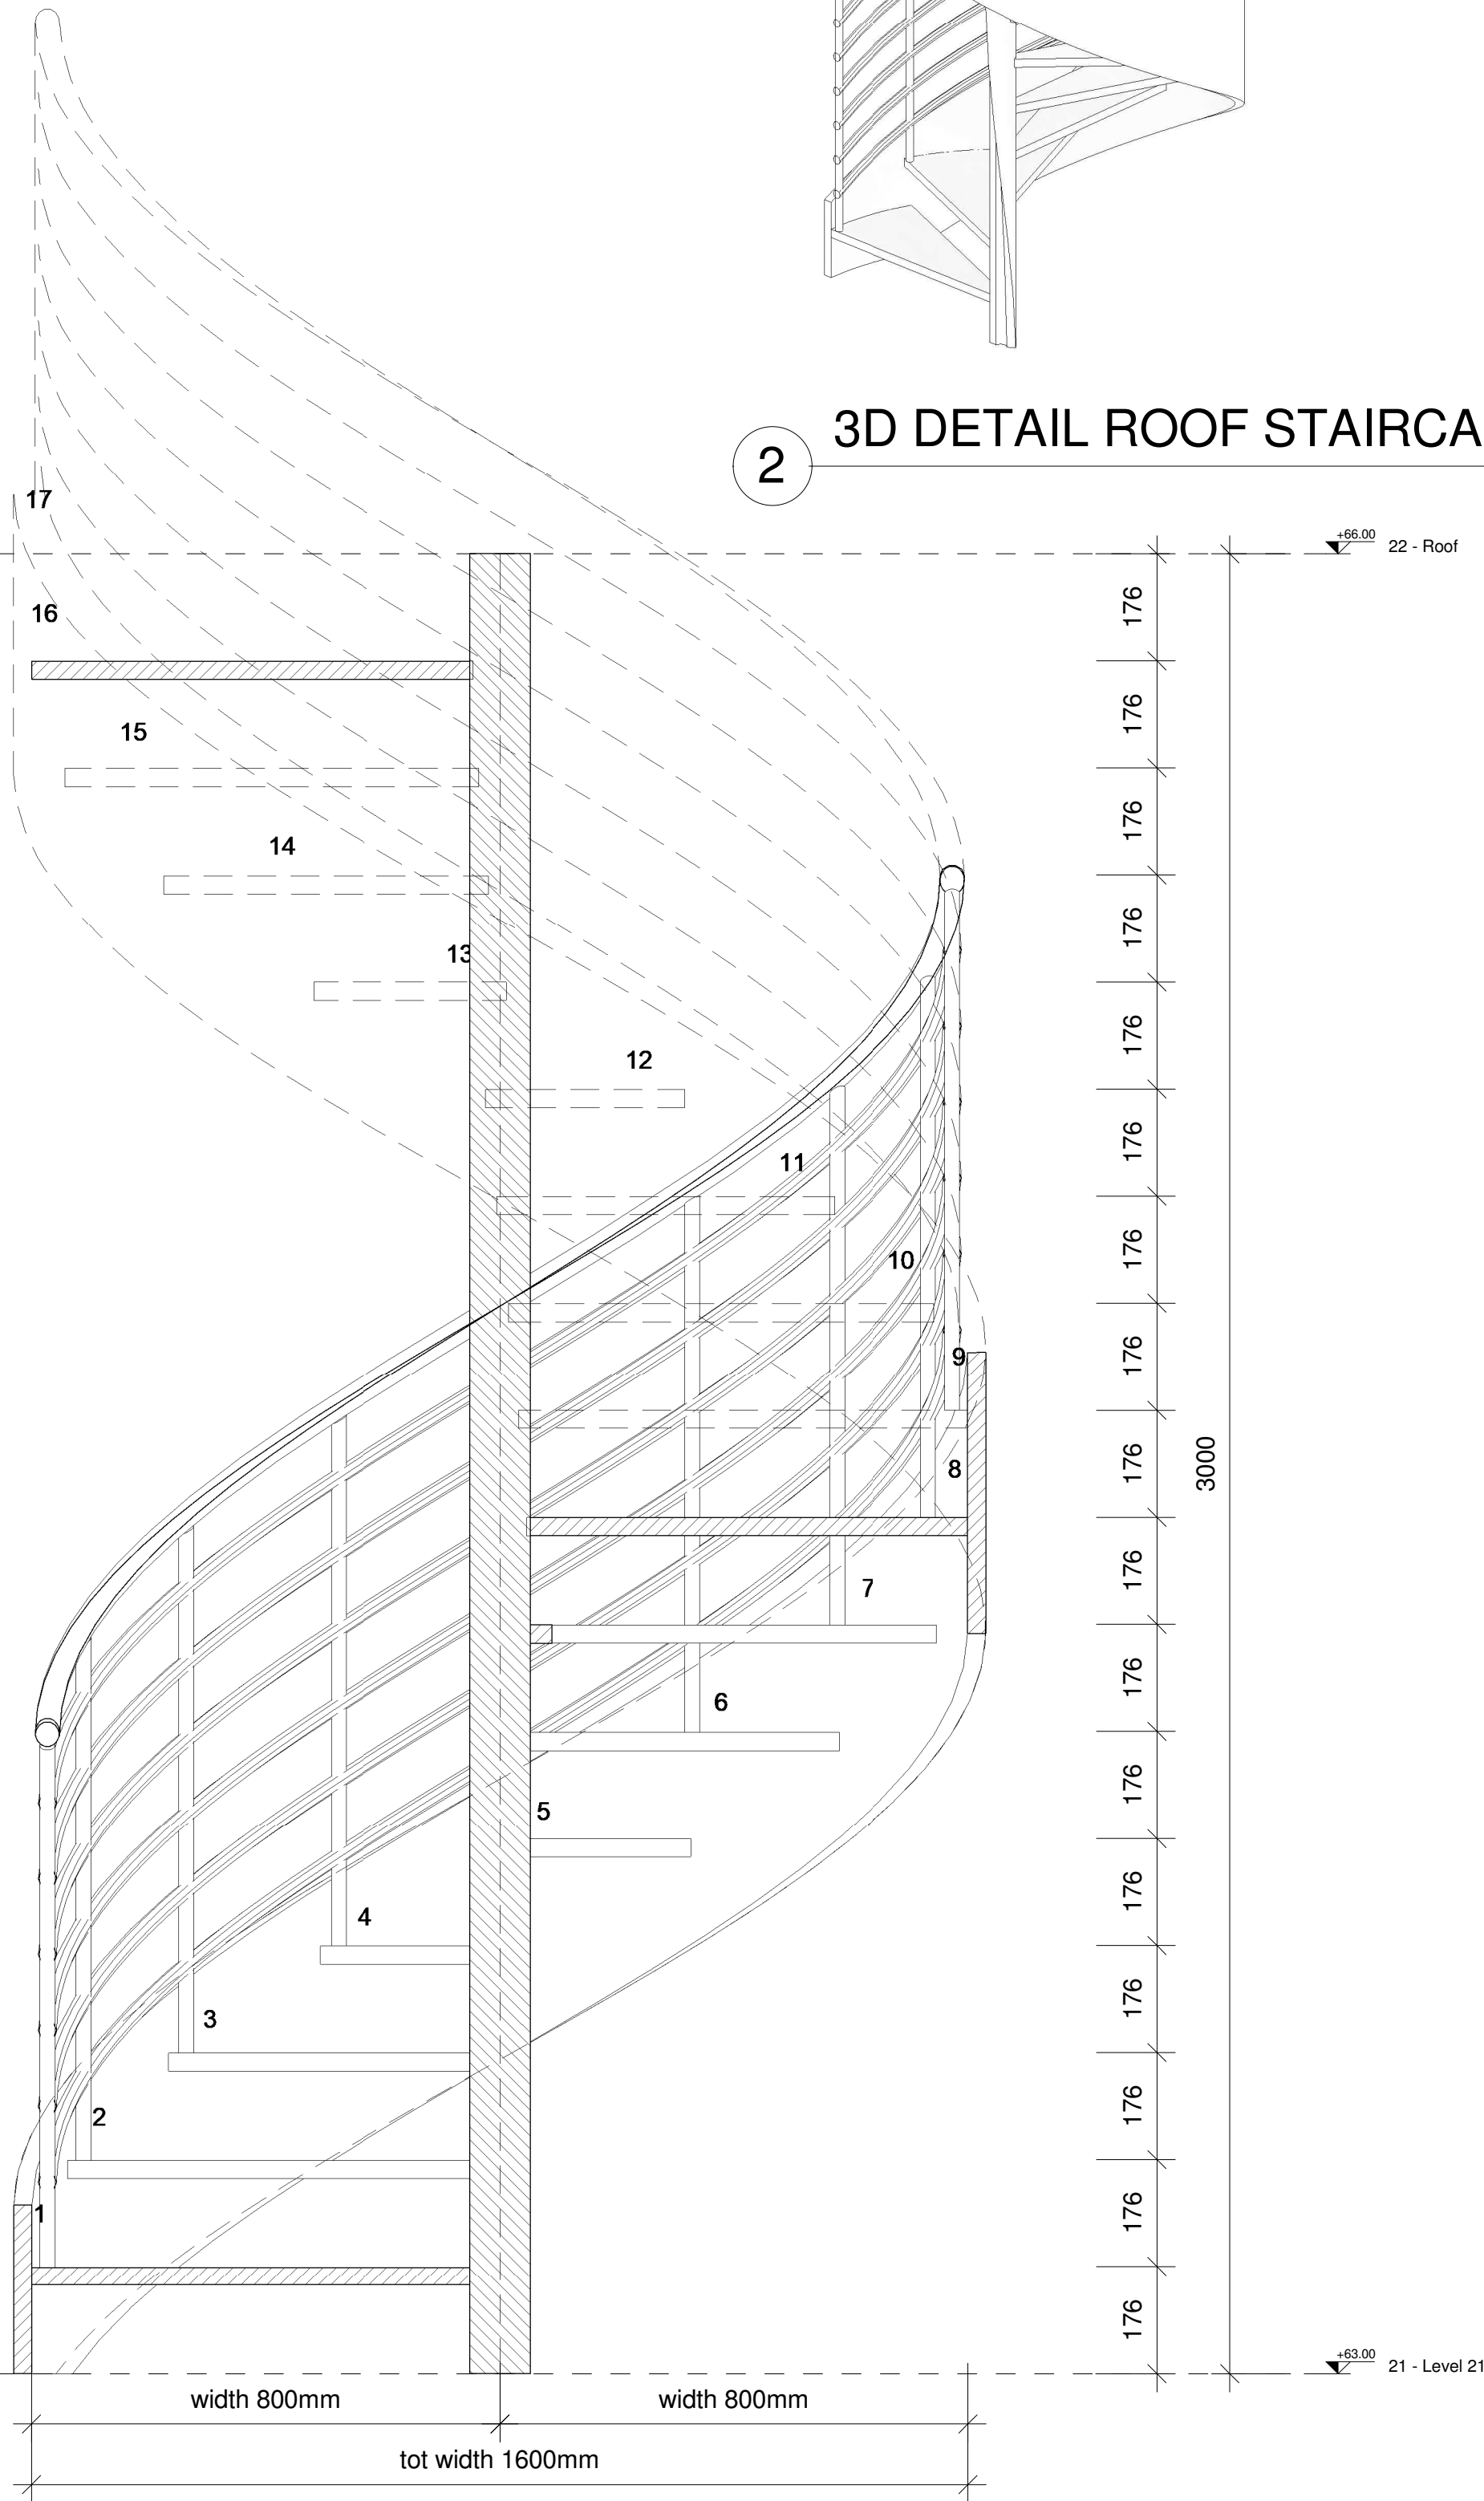

B Section BB
1 : 10

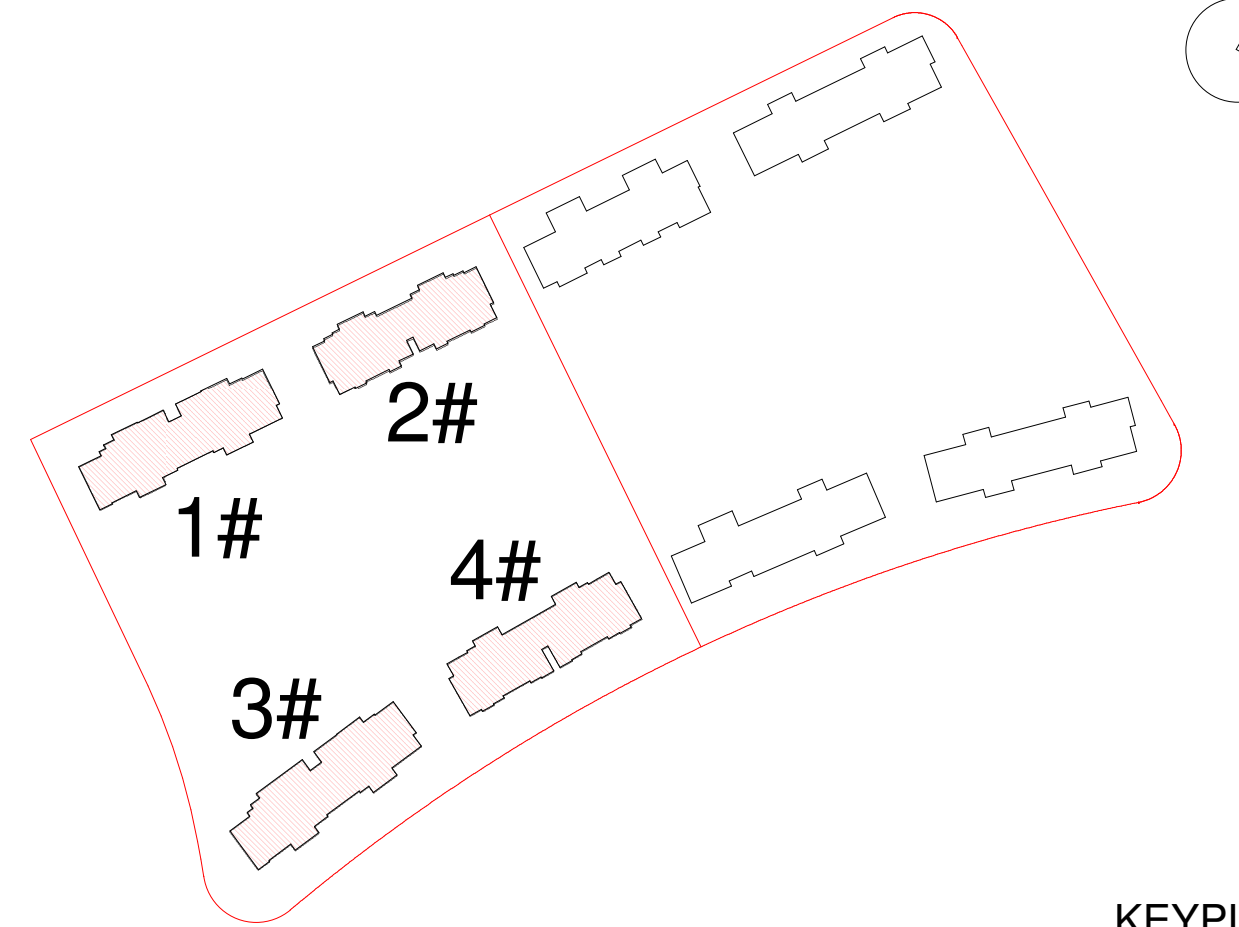

KEYPLAN

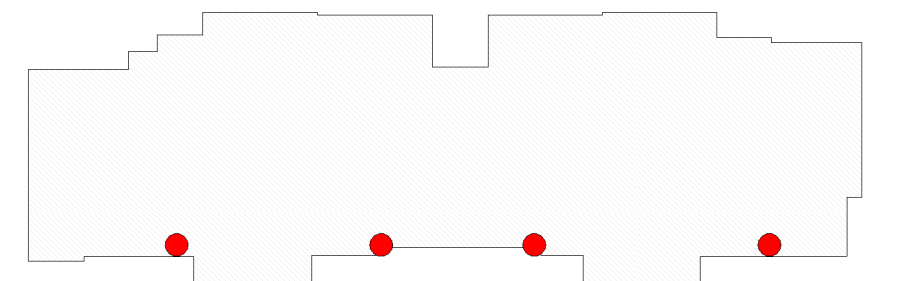

GENERAL NOTES:

- A. ALL DIMENSIONS GIVEN ON THIS DRAWING ARE INMILLIMETERS. DO NOT SCALE THE DRAWINGS. ANY DISCREPANCIES FOUND SHOULD BE REPORTED TO THE RESPONSIBLE ARCHITECT OR ENGINEER IMMEDIATELY.
- B. IT IS THE RESPONSIBILITY OF THE CONTRACTOR OR BUILDERS TO ASCERTAIN AND CONFIRM THAT ALL DIMENSIONS SHOWN IN THESE DRAWINGS SHALL COMPLY WITH THE SITE DIMENSIONS AND LEVELS PRIOR TO PREPARING DRAWINGS AND EXECUTING THE WORKS.
- C. ALL MEASUREMENT MUST BE VERIFIED AND CONFIRMED AT CONSTRUCTION SITE.
- D. ALL WORKS ARE TO BE CARRIED OUT TO LOCAL CODES OF CONSTRUCTIONS.
- E. THIS DRAWINGS SHOULD BE READ IN CONJUNCTION WITH THE OTHER RELEVANT ARCHITECTURAL, STRUCTURAL, MECHANICAL AND ELECTRICAL DRAWINGS AND ALL RELEVANT SECTIONS OF THE SPECIFICATIONS.
- F. EXACT LOCATION, SIZES AND DETAILS OF ELECTRO-MECHANICAL WALL OPENINGS SHALL BE COORDINATED WITH ELECTRO-MECHANICAL ENGINEERS.
- G. DIMENSION AND LOCATION OF SERVICES SHALL BE COORDINATED WITH RESPECTIVE ARCHITECTURAL AND SERVICES DRAWINGS PRIOR TO COMMENCEMENT OF ANY WORK. ANY DISCREPANCY FOUND SHOULD BE BROUGHT TO THE NOTICE OF THE CONCERNED ENGINEER.
- H. ALL MATERIALS MUST BE VERIFIED AND CONFIRMED BY PEIA ASSOCIATI SRL ON SHOP DRAWINGS AND SAMPLES BY CONTRACTOR.
- I. REFER TO SCHEDULE OF FINISHES FOR FLOORS, WALLS AND CEILINGS.
- J. ALL MATERIAL FINISHES AND WORMANSHIP SHOULD BE OF HIGH STANDARD QUALITY OF WORKS.
- K. ALL TEXTURES AND COLORS SHOULD BE REFERED TO SCHEDULE OF FINISHES AND HAVE APPROVAL OF ARCHITECT.

LEGEND:

F.F.L. = FLOOR FINISHING LEVEL

Architect:		Peia associati srl Via Cadolini, 30 - 20137 Milano, Italy Tel: +39 02 6598647 Fax: +39 02 36554984 e-mail: info@peiaassociati.it	
Engineering:			
Owner:		Yanfull (Shanghai) Co. Ltd. 78, Xin Zhen road Qi Bao town Min Hang district Shanghai 201101 P.R. China	
Project:		ROYAL GARDEN PHASE 4 Shanghai, China	
Drawing Subject:		DET_DETAIL TYPICAL ROOF STAIRCASE	
Designed:	Draft:	Checked:	Review:
Peia Associati s.r.l.	YW	GP	1
Date:	Scale:	ID File:	Sheet No.:
12/06/2017	@A1 (841x594mm)	1501_RG_Block A1N(West)	RG4_402