
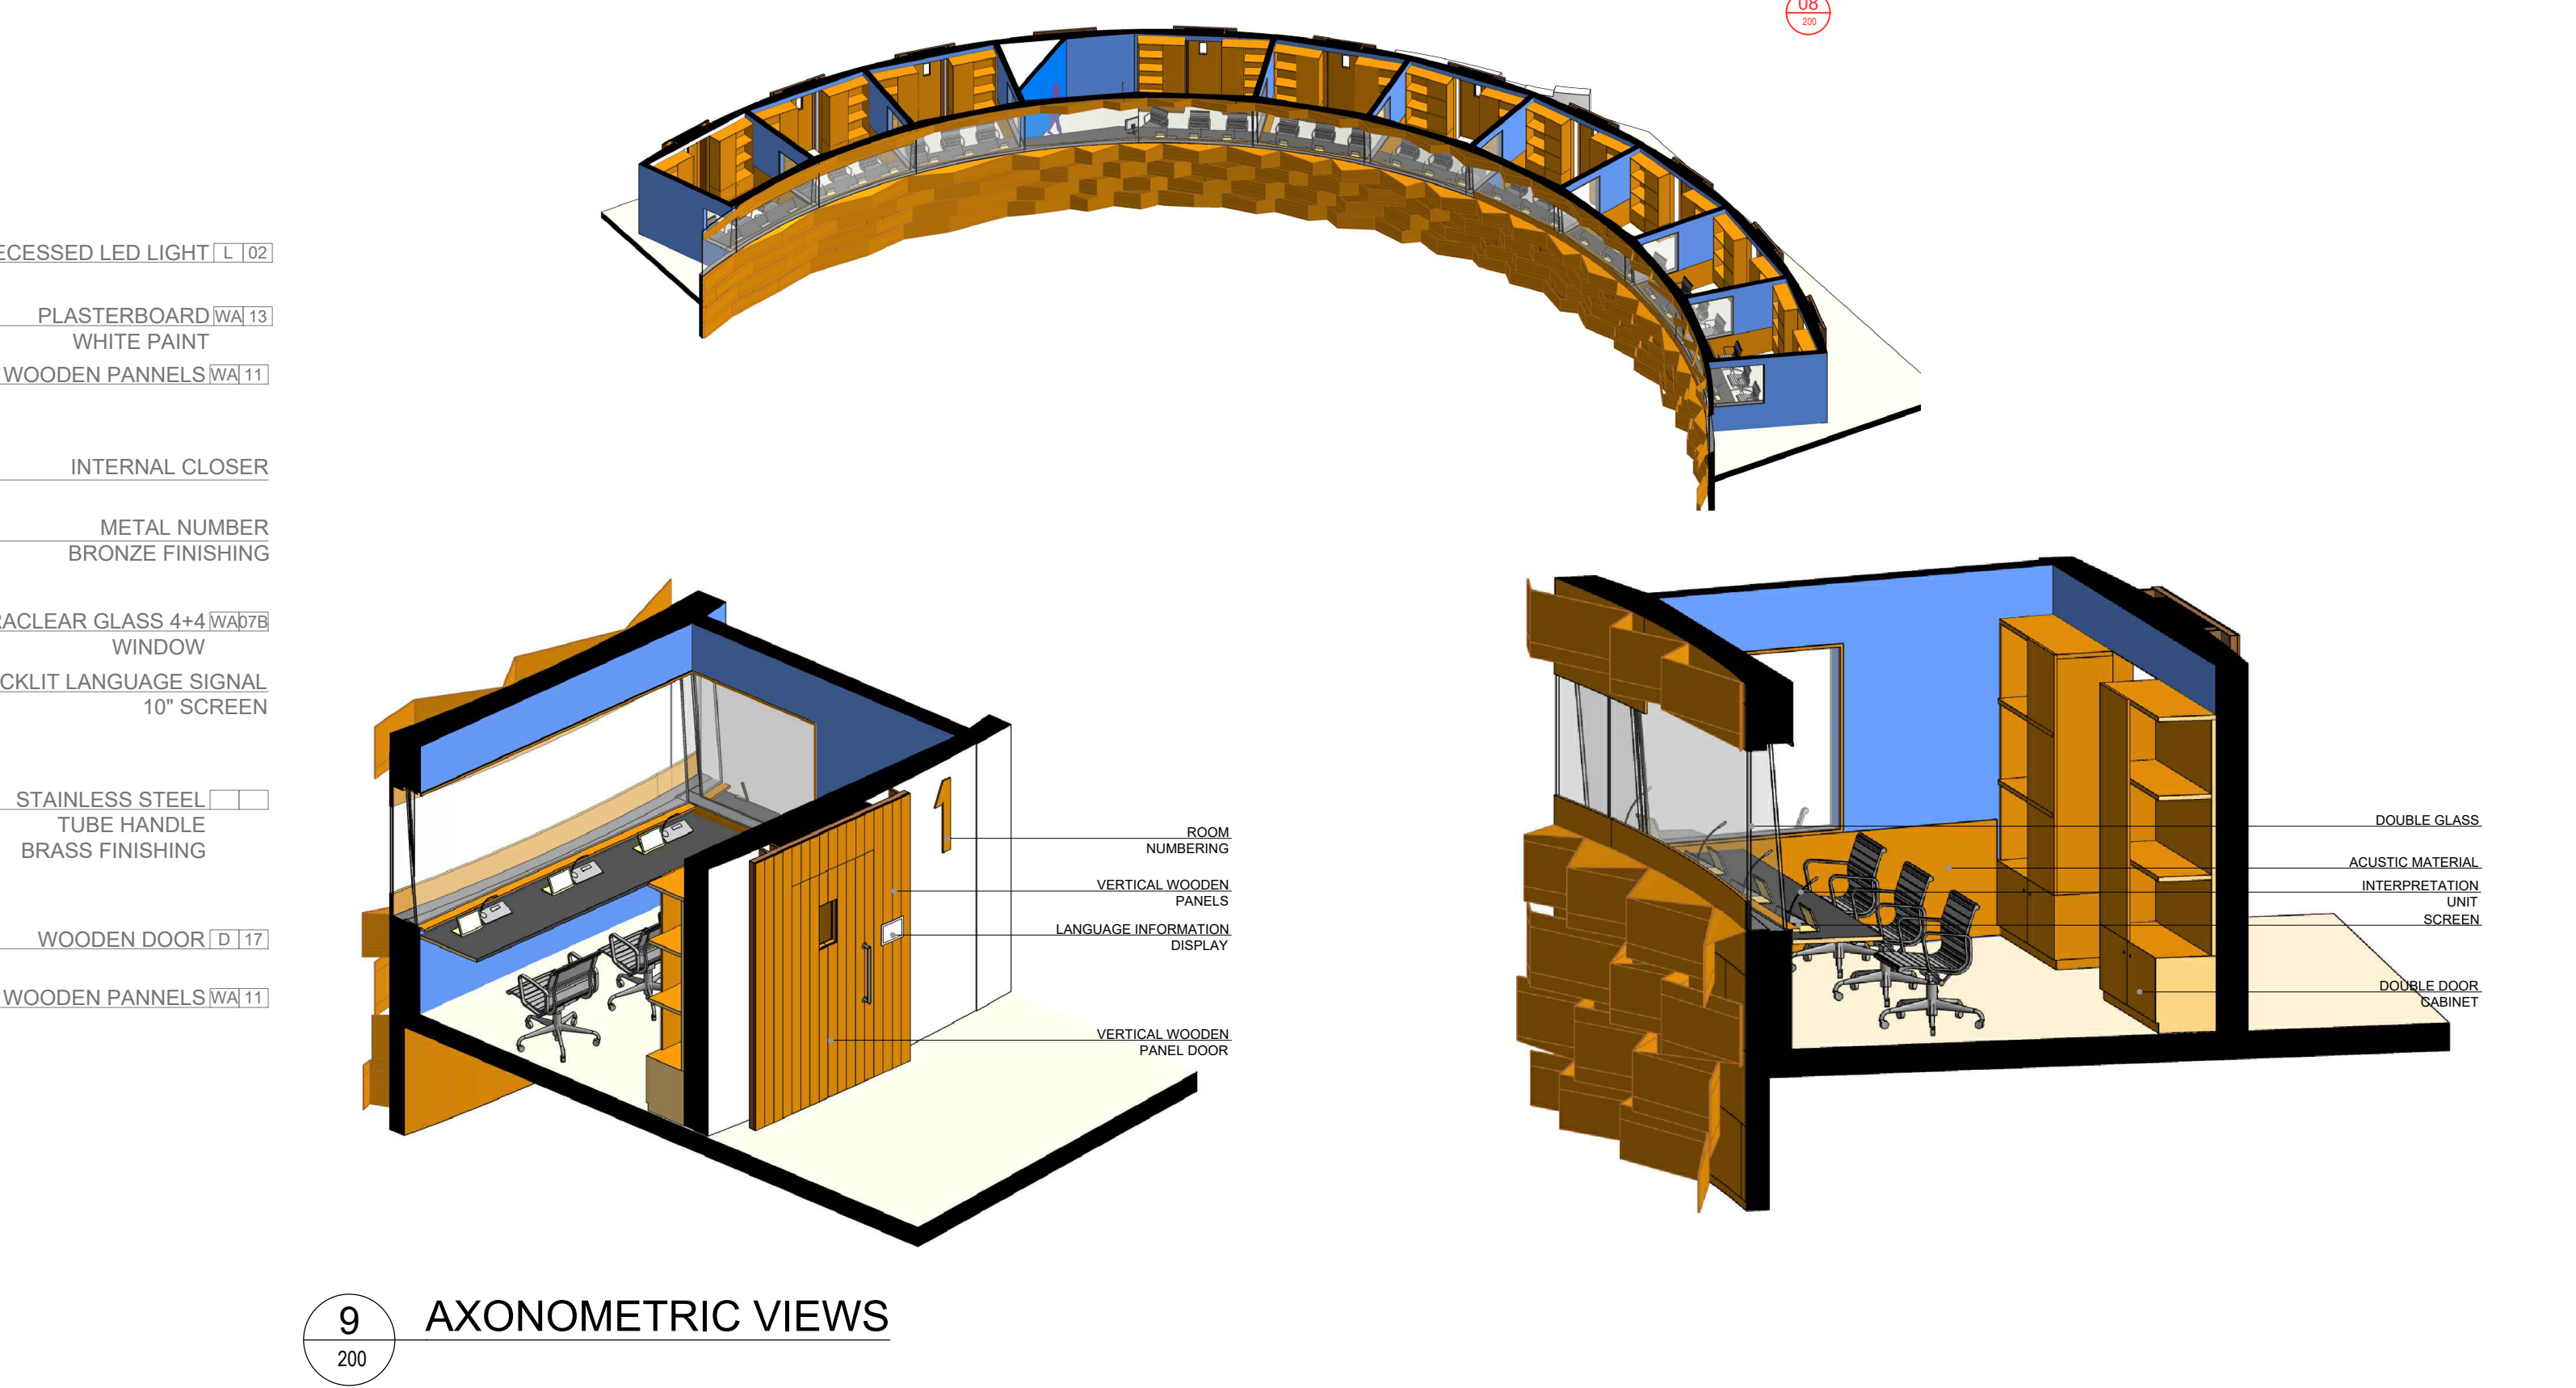
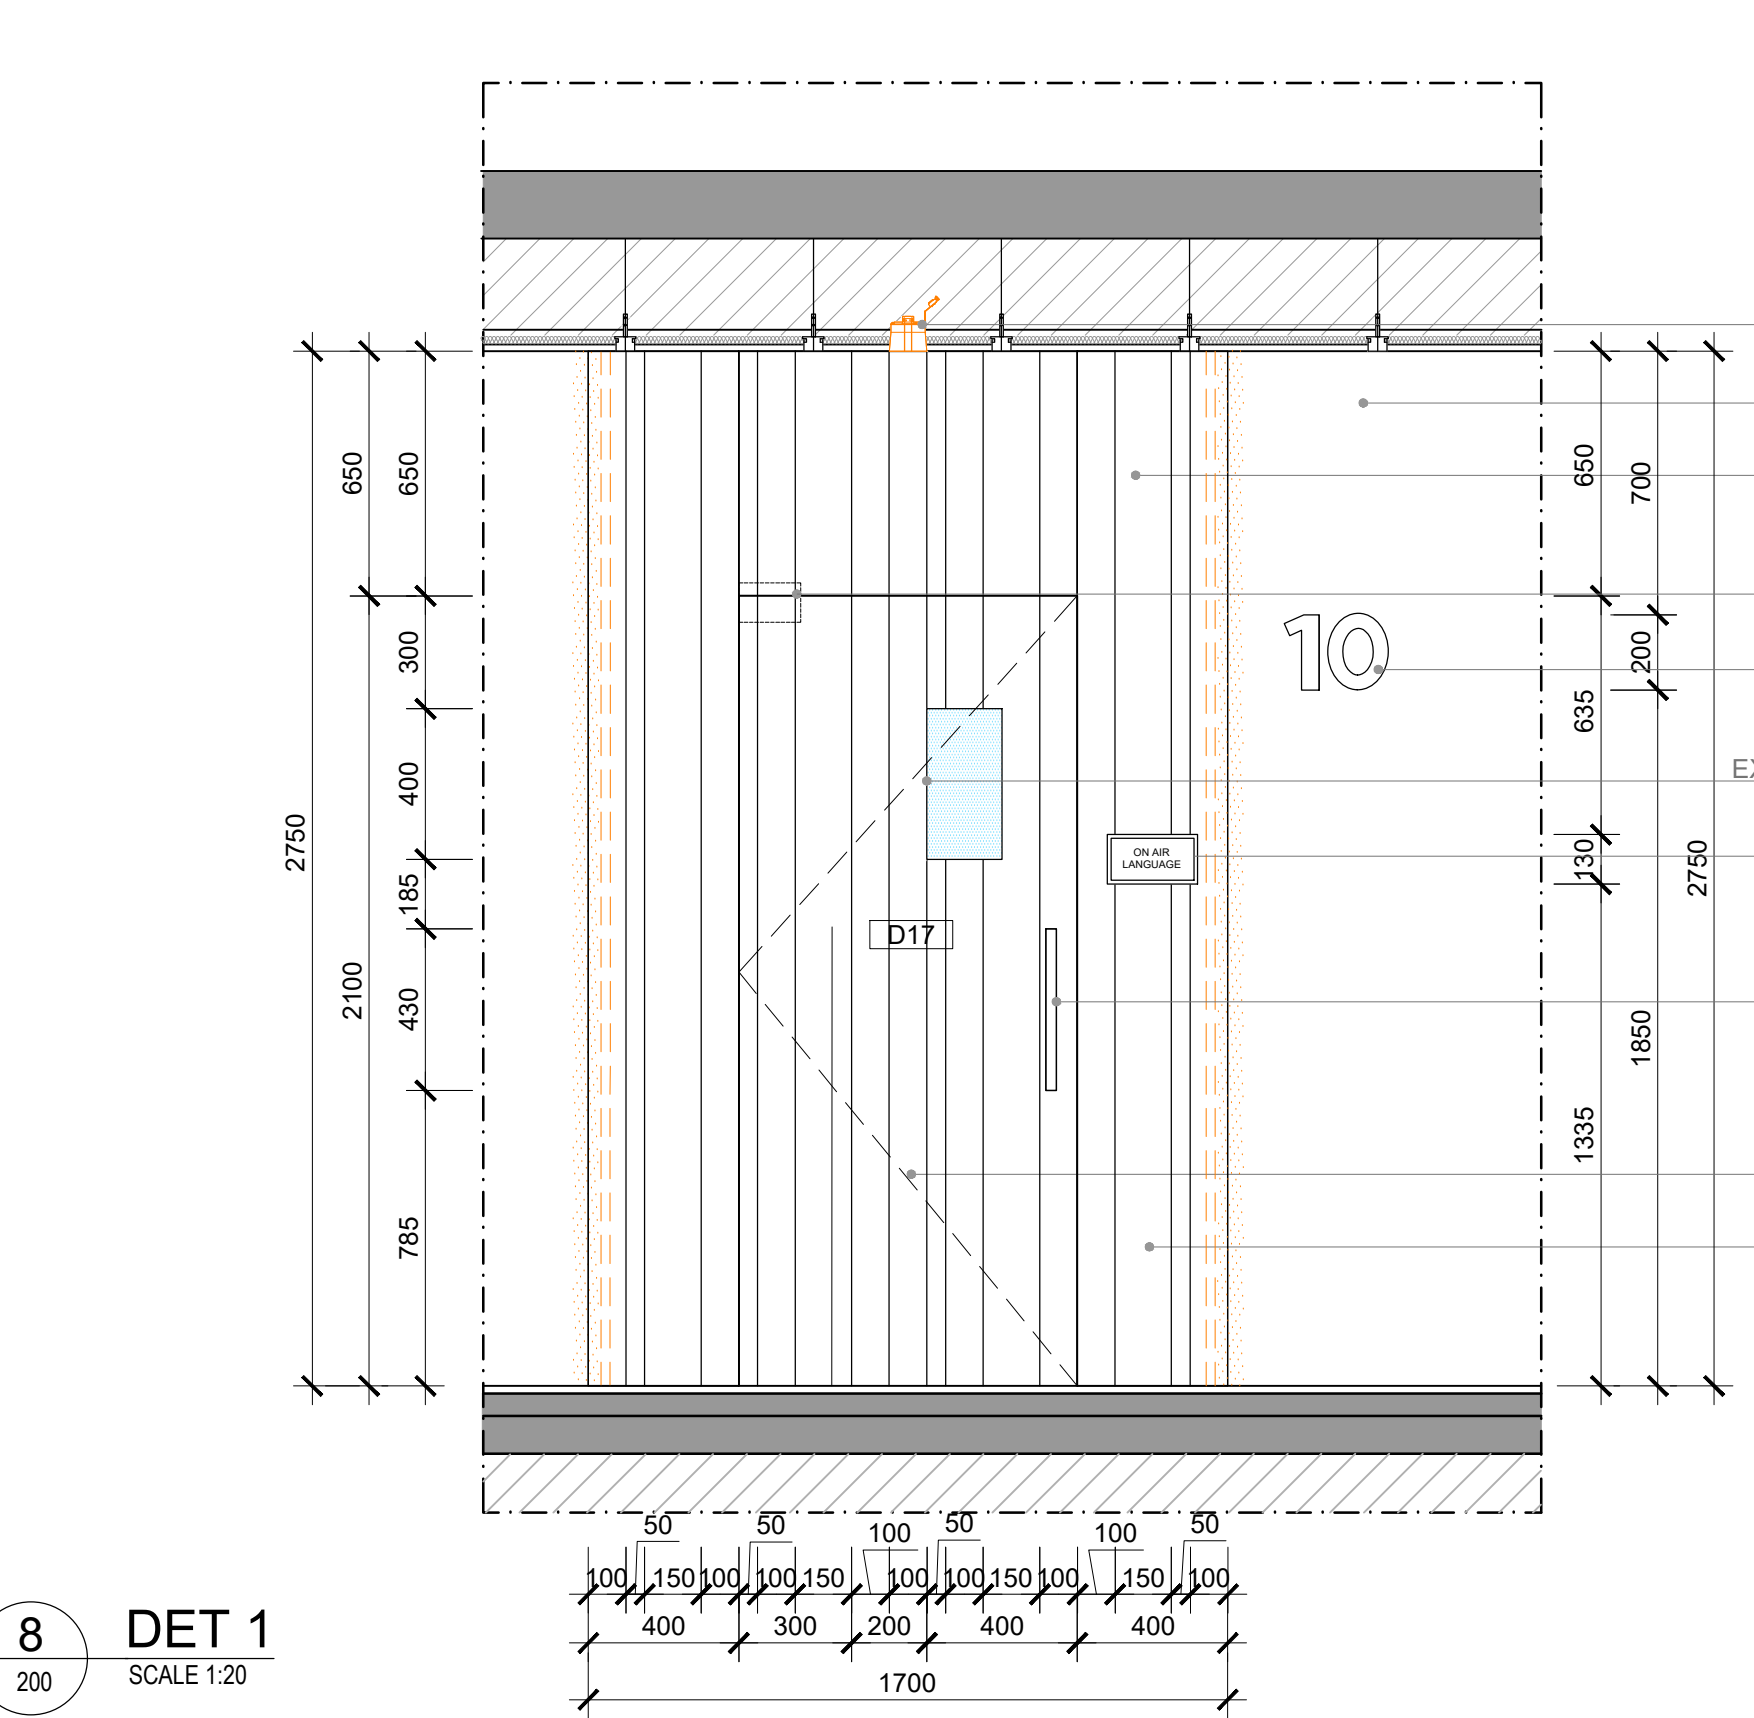
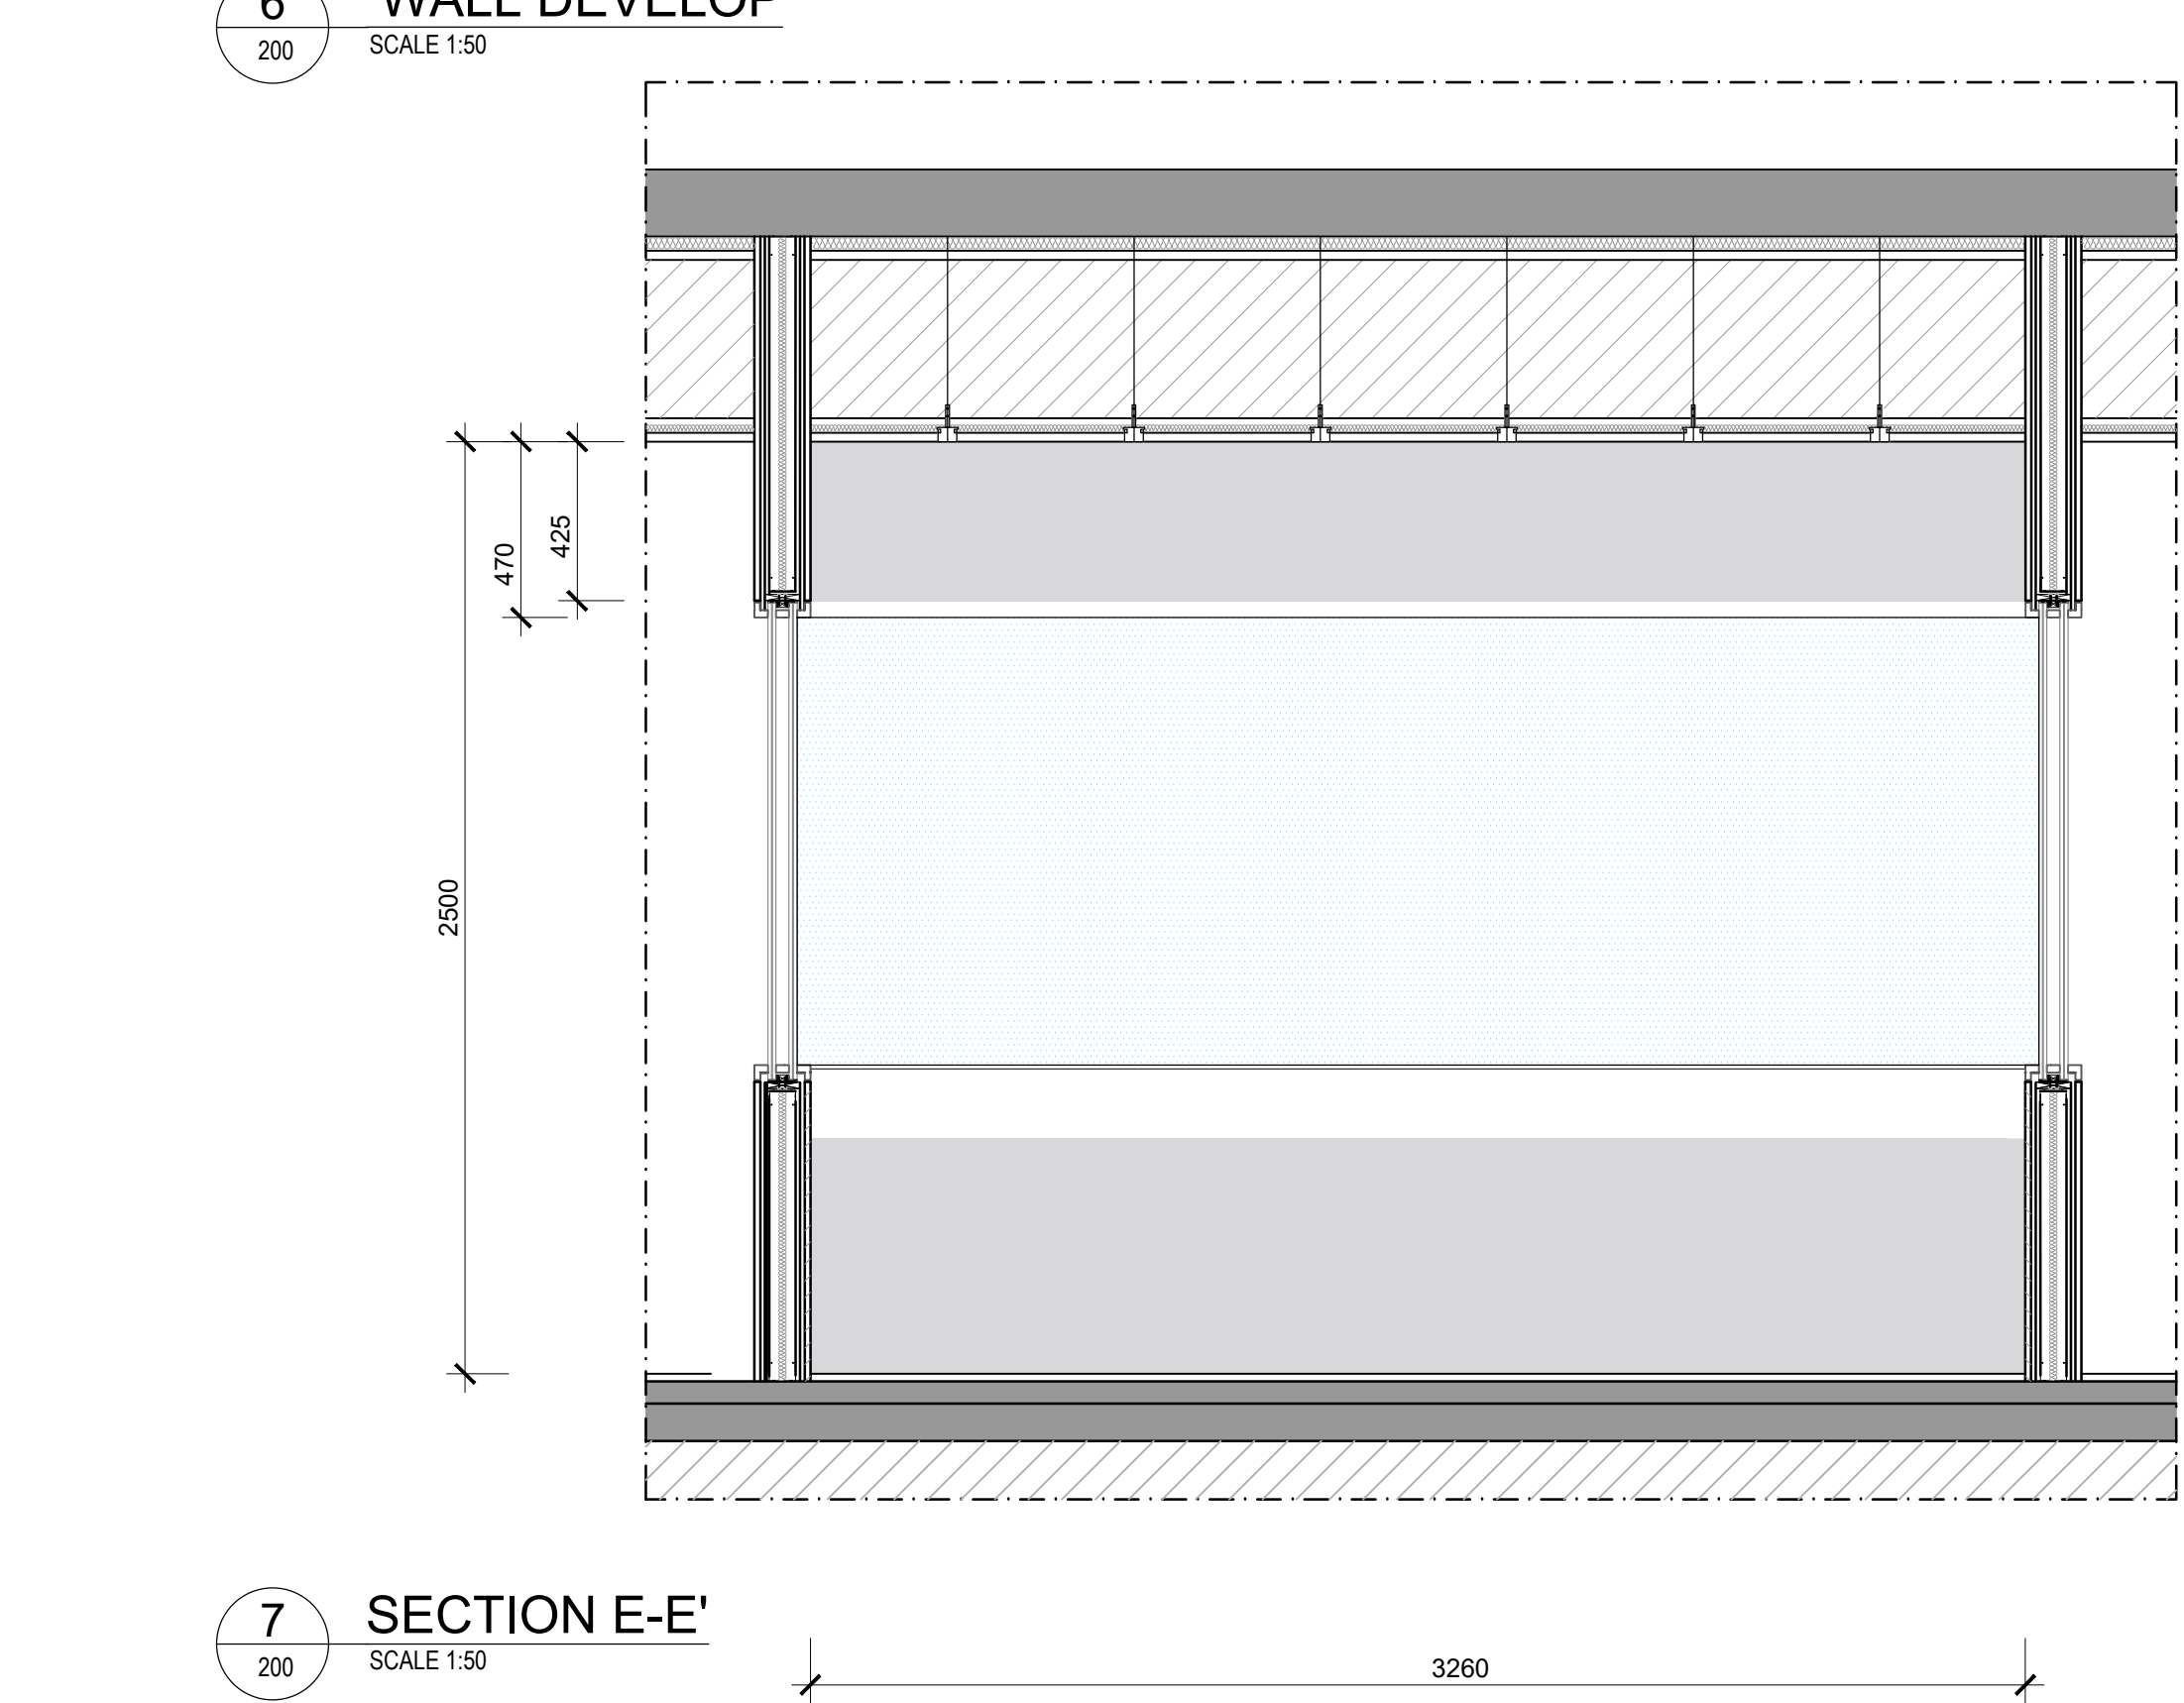
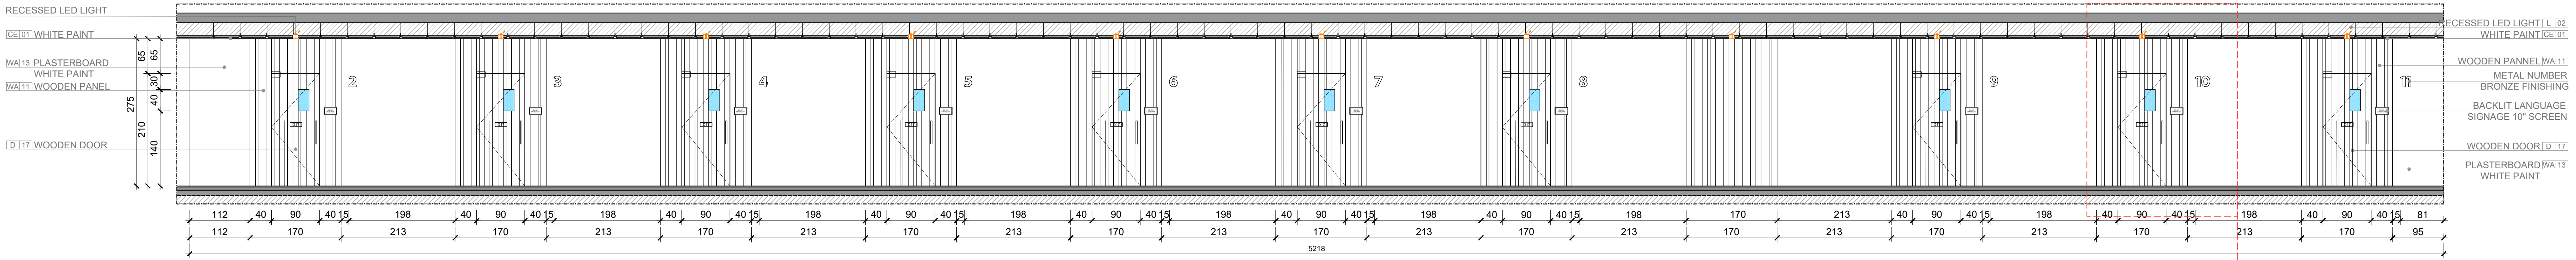
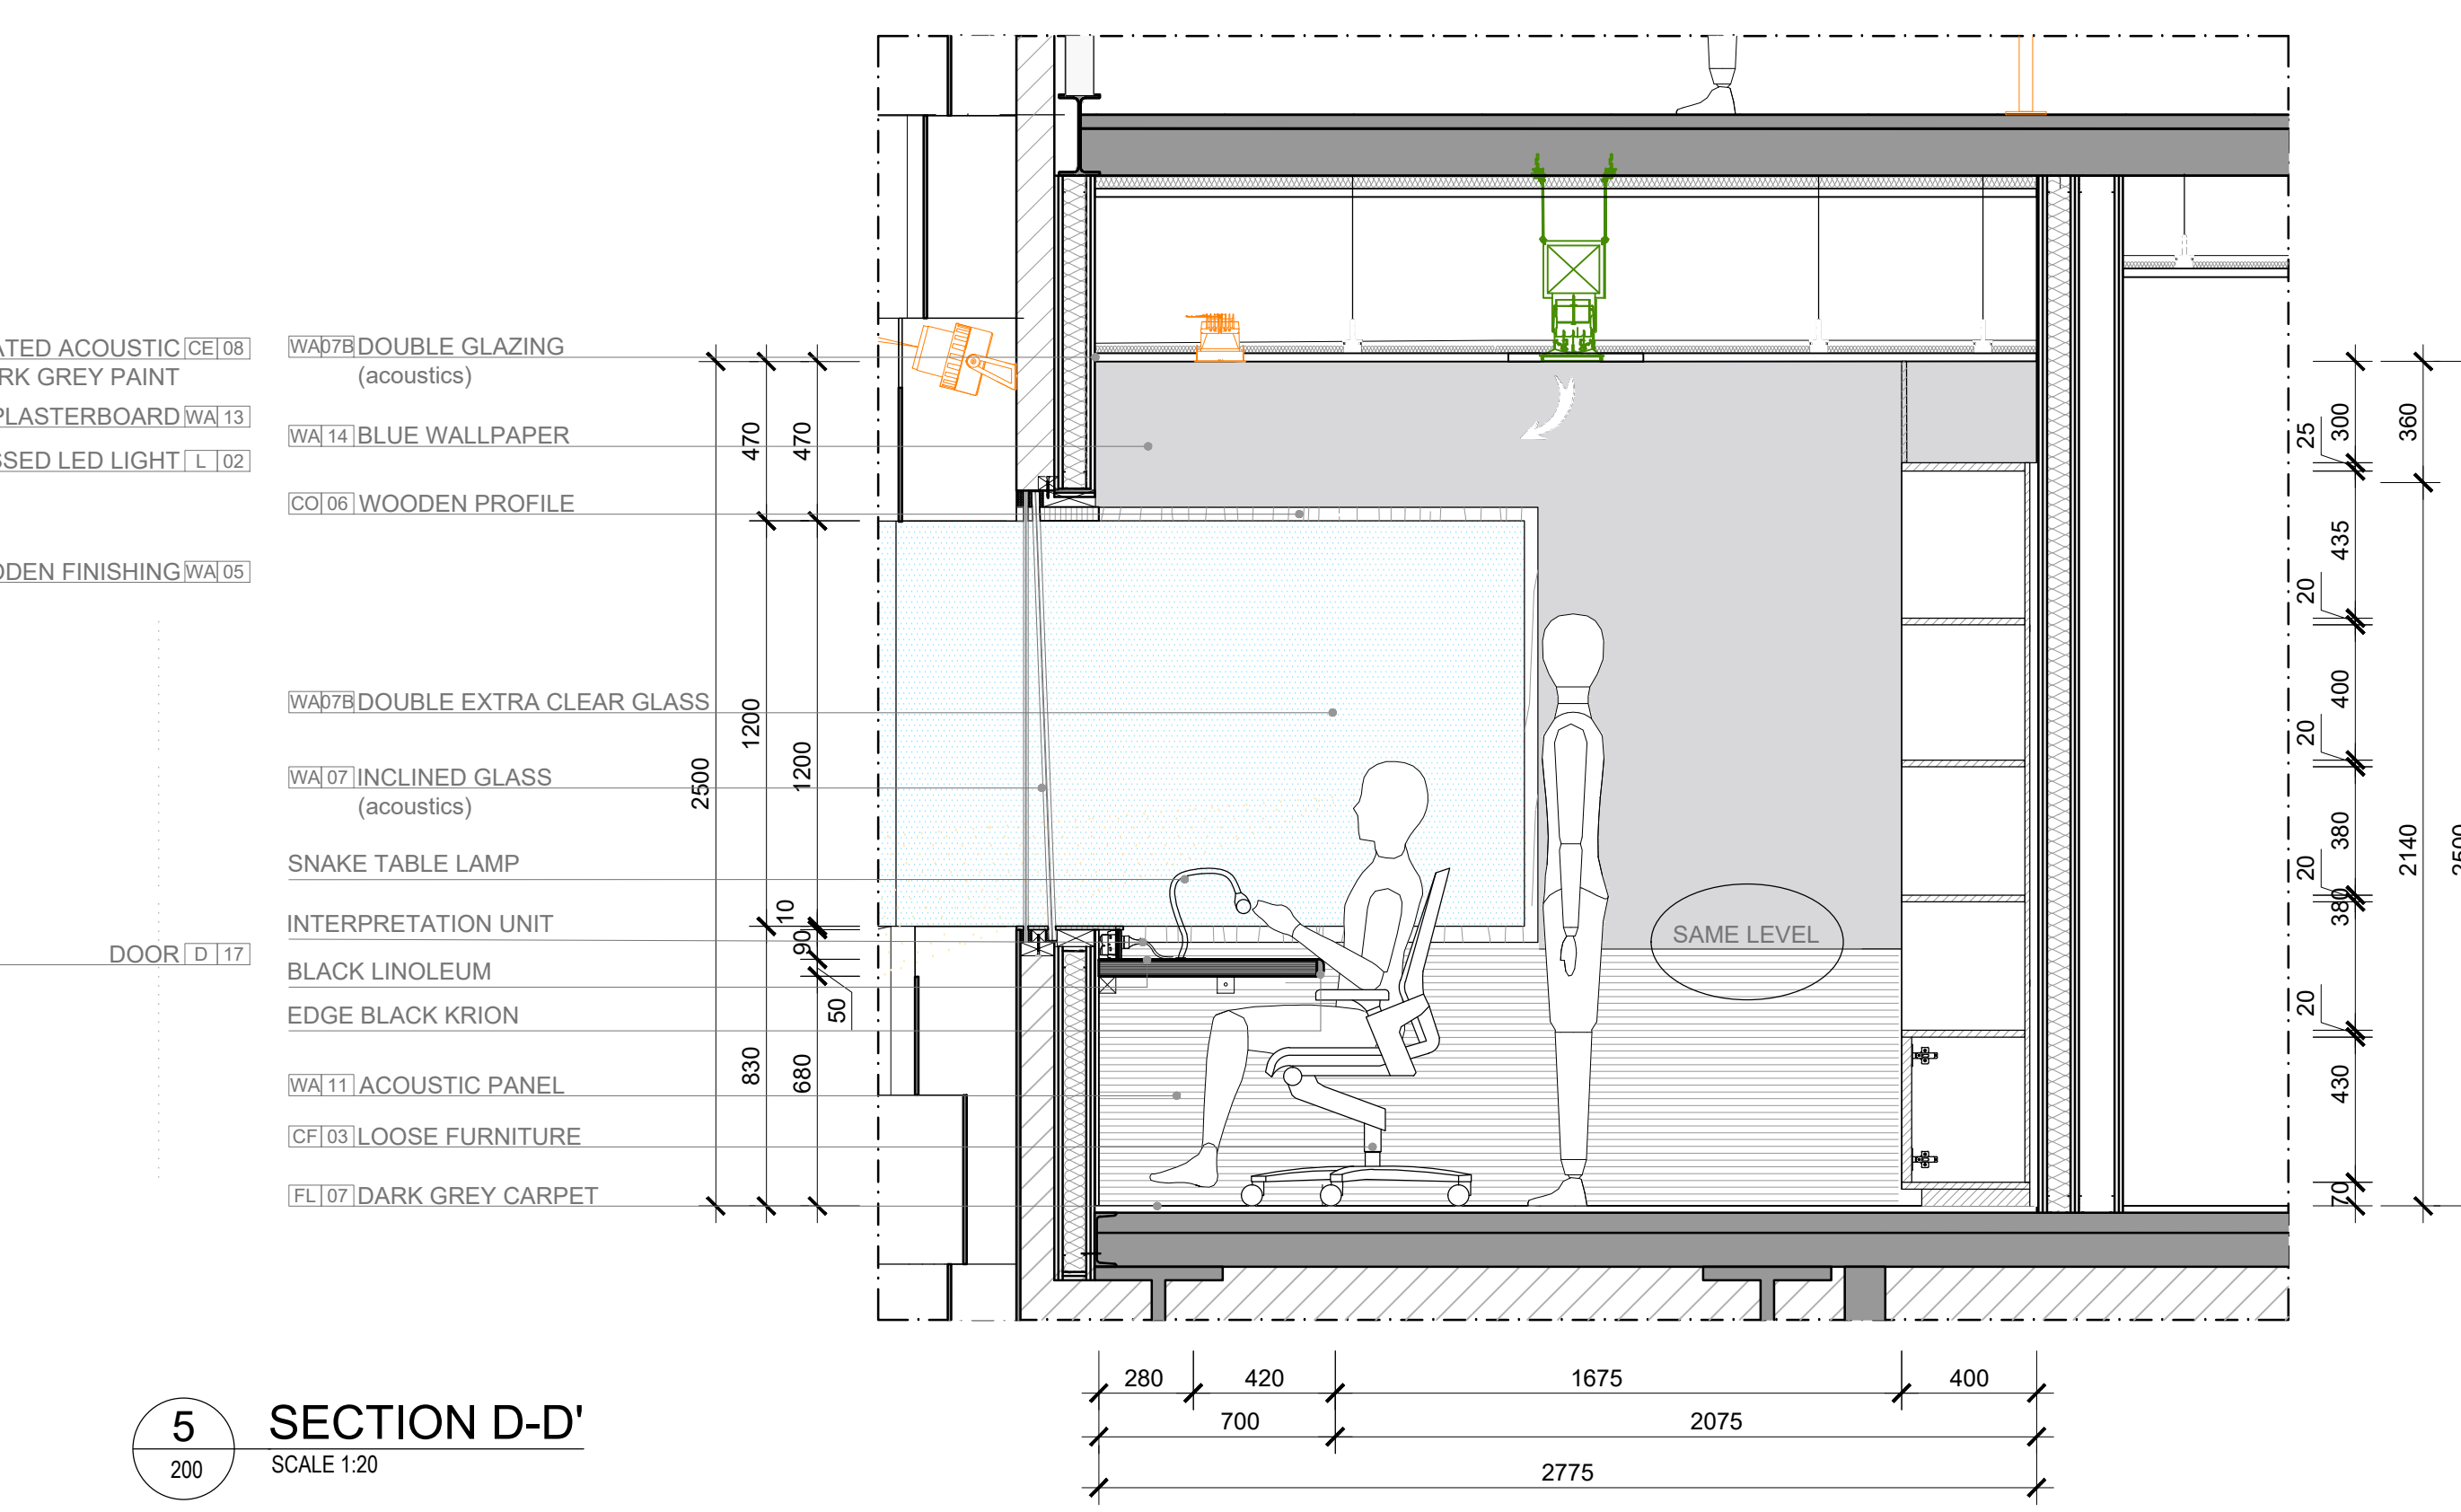
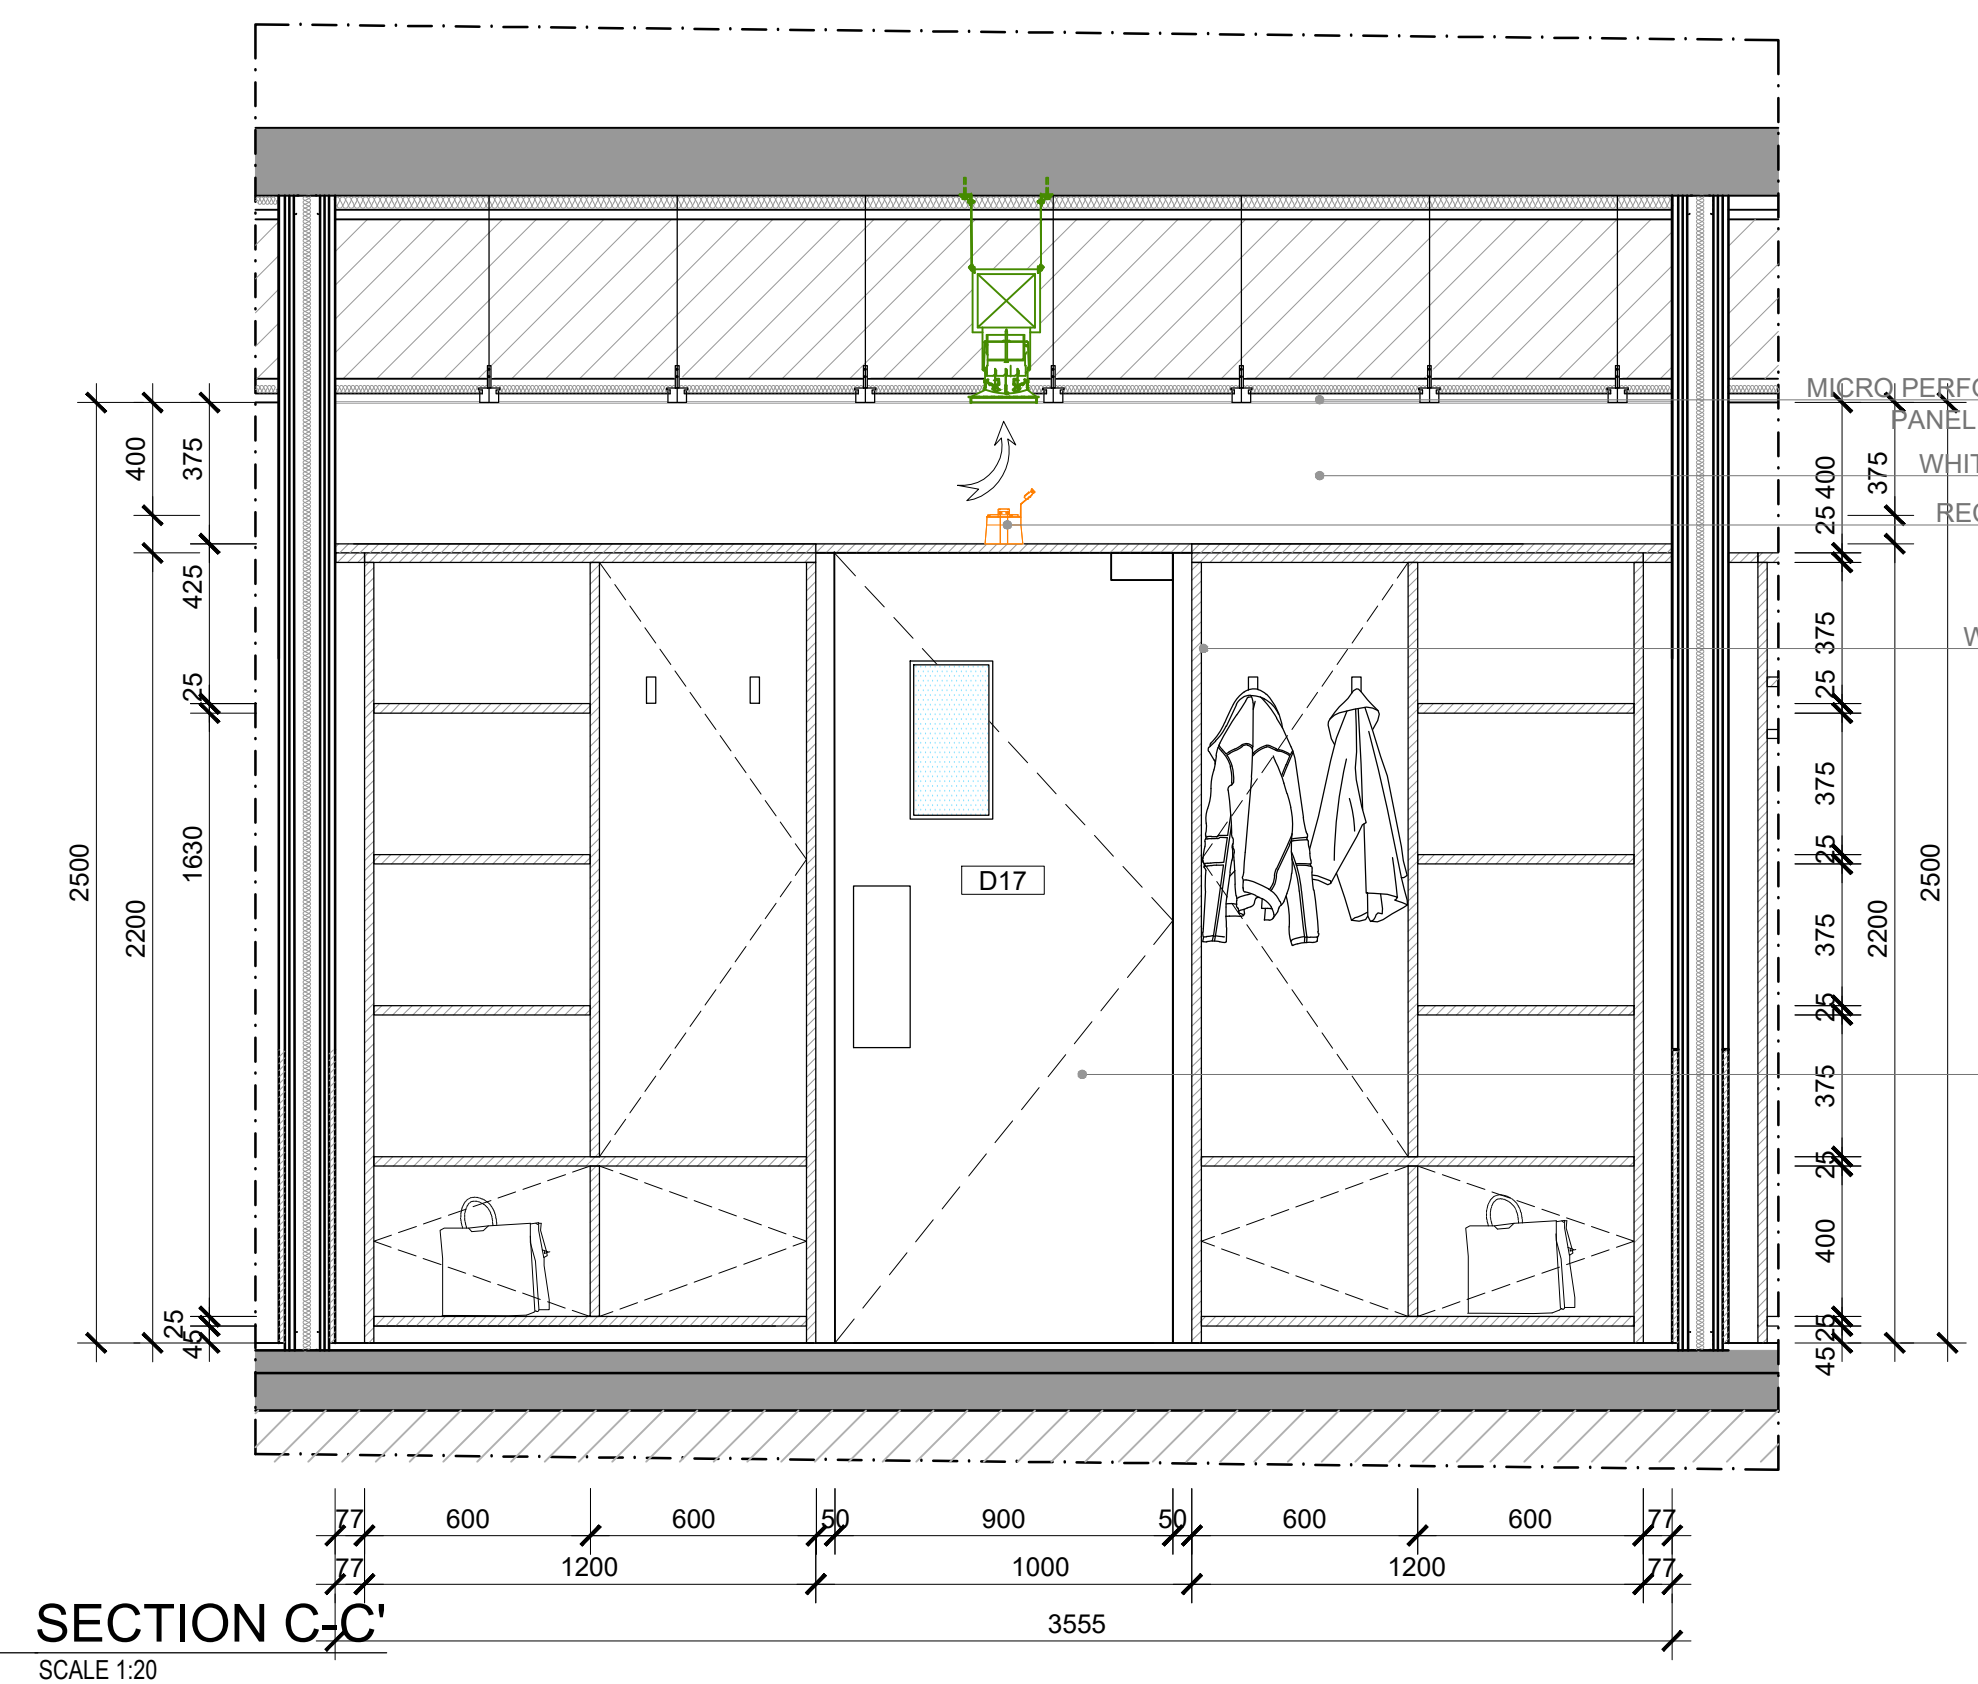
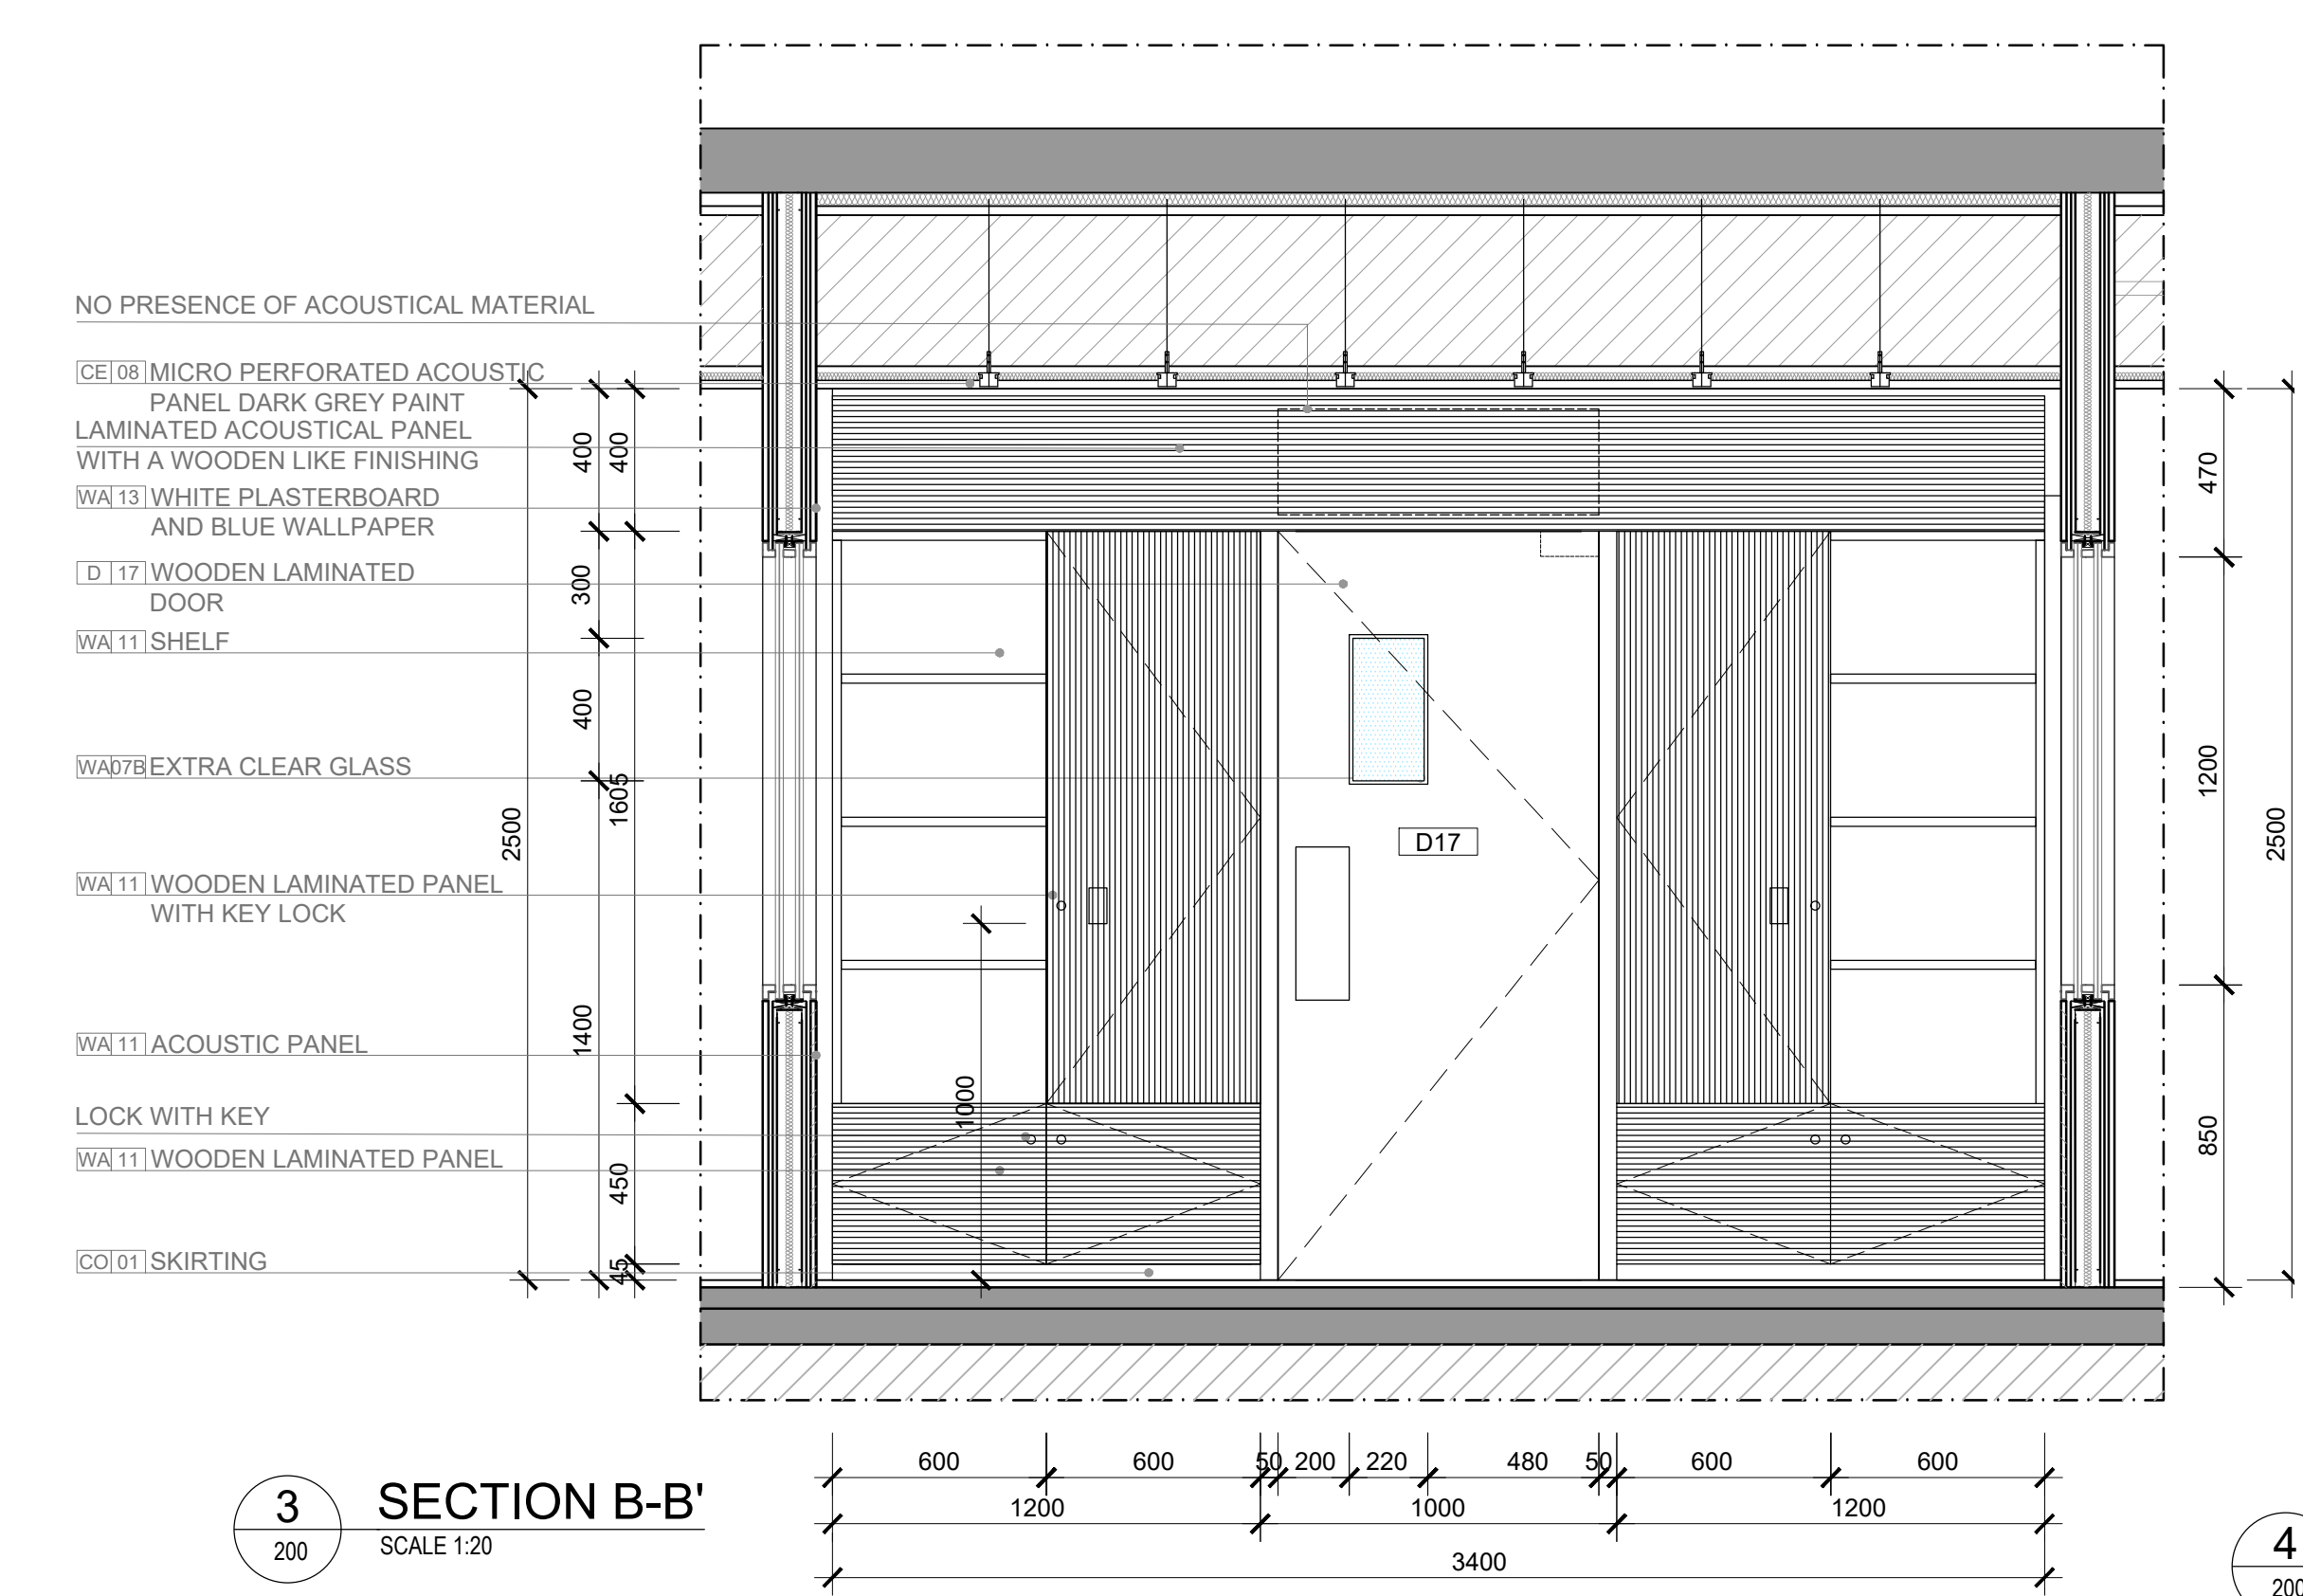
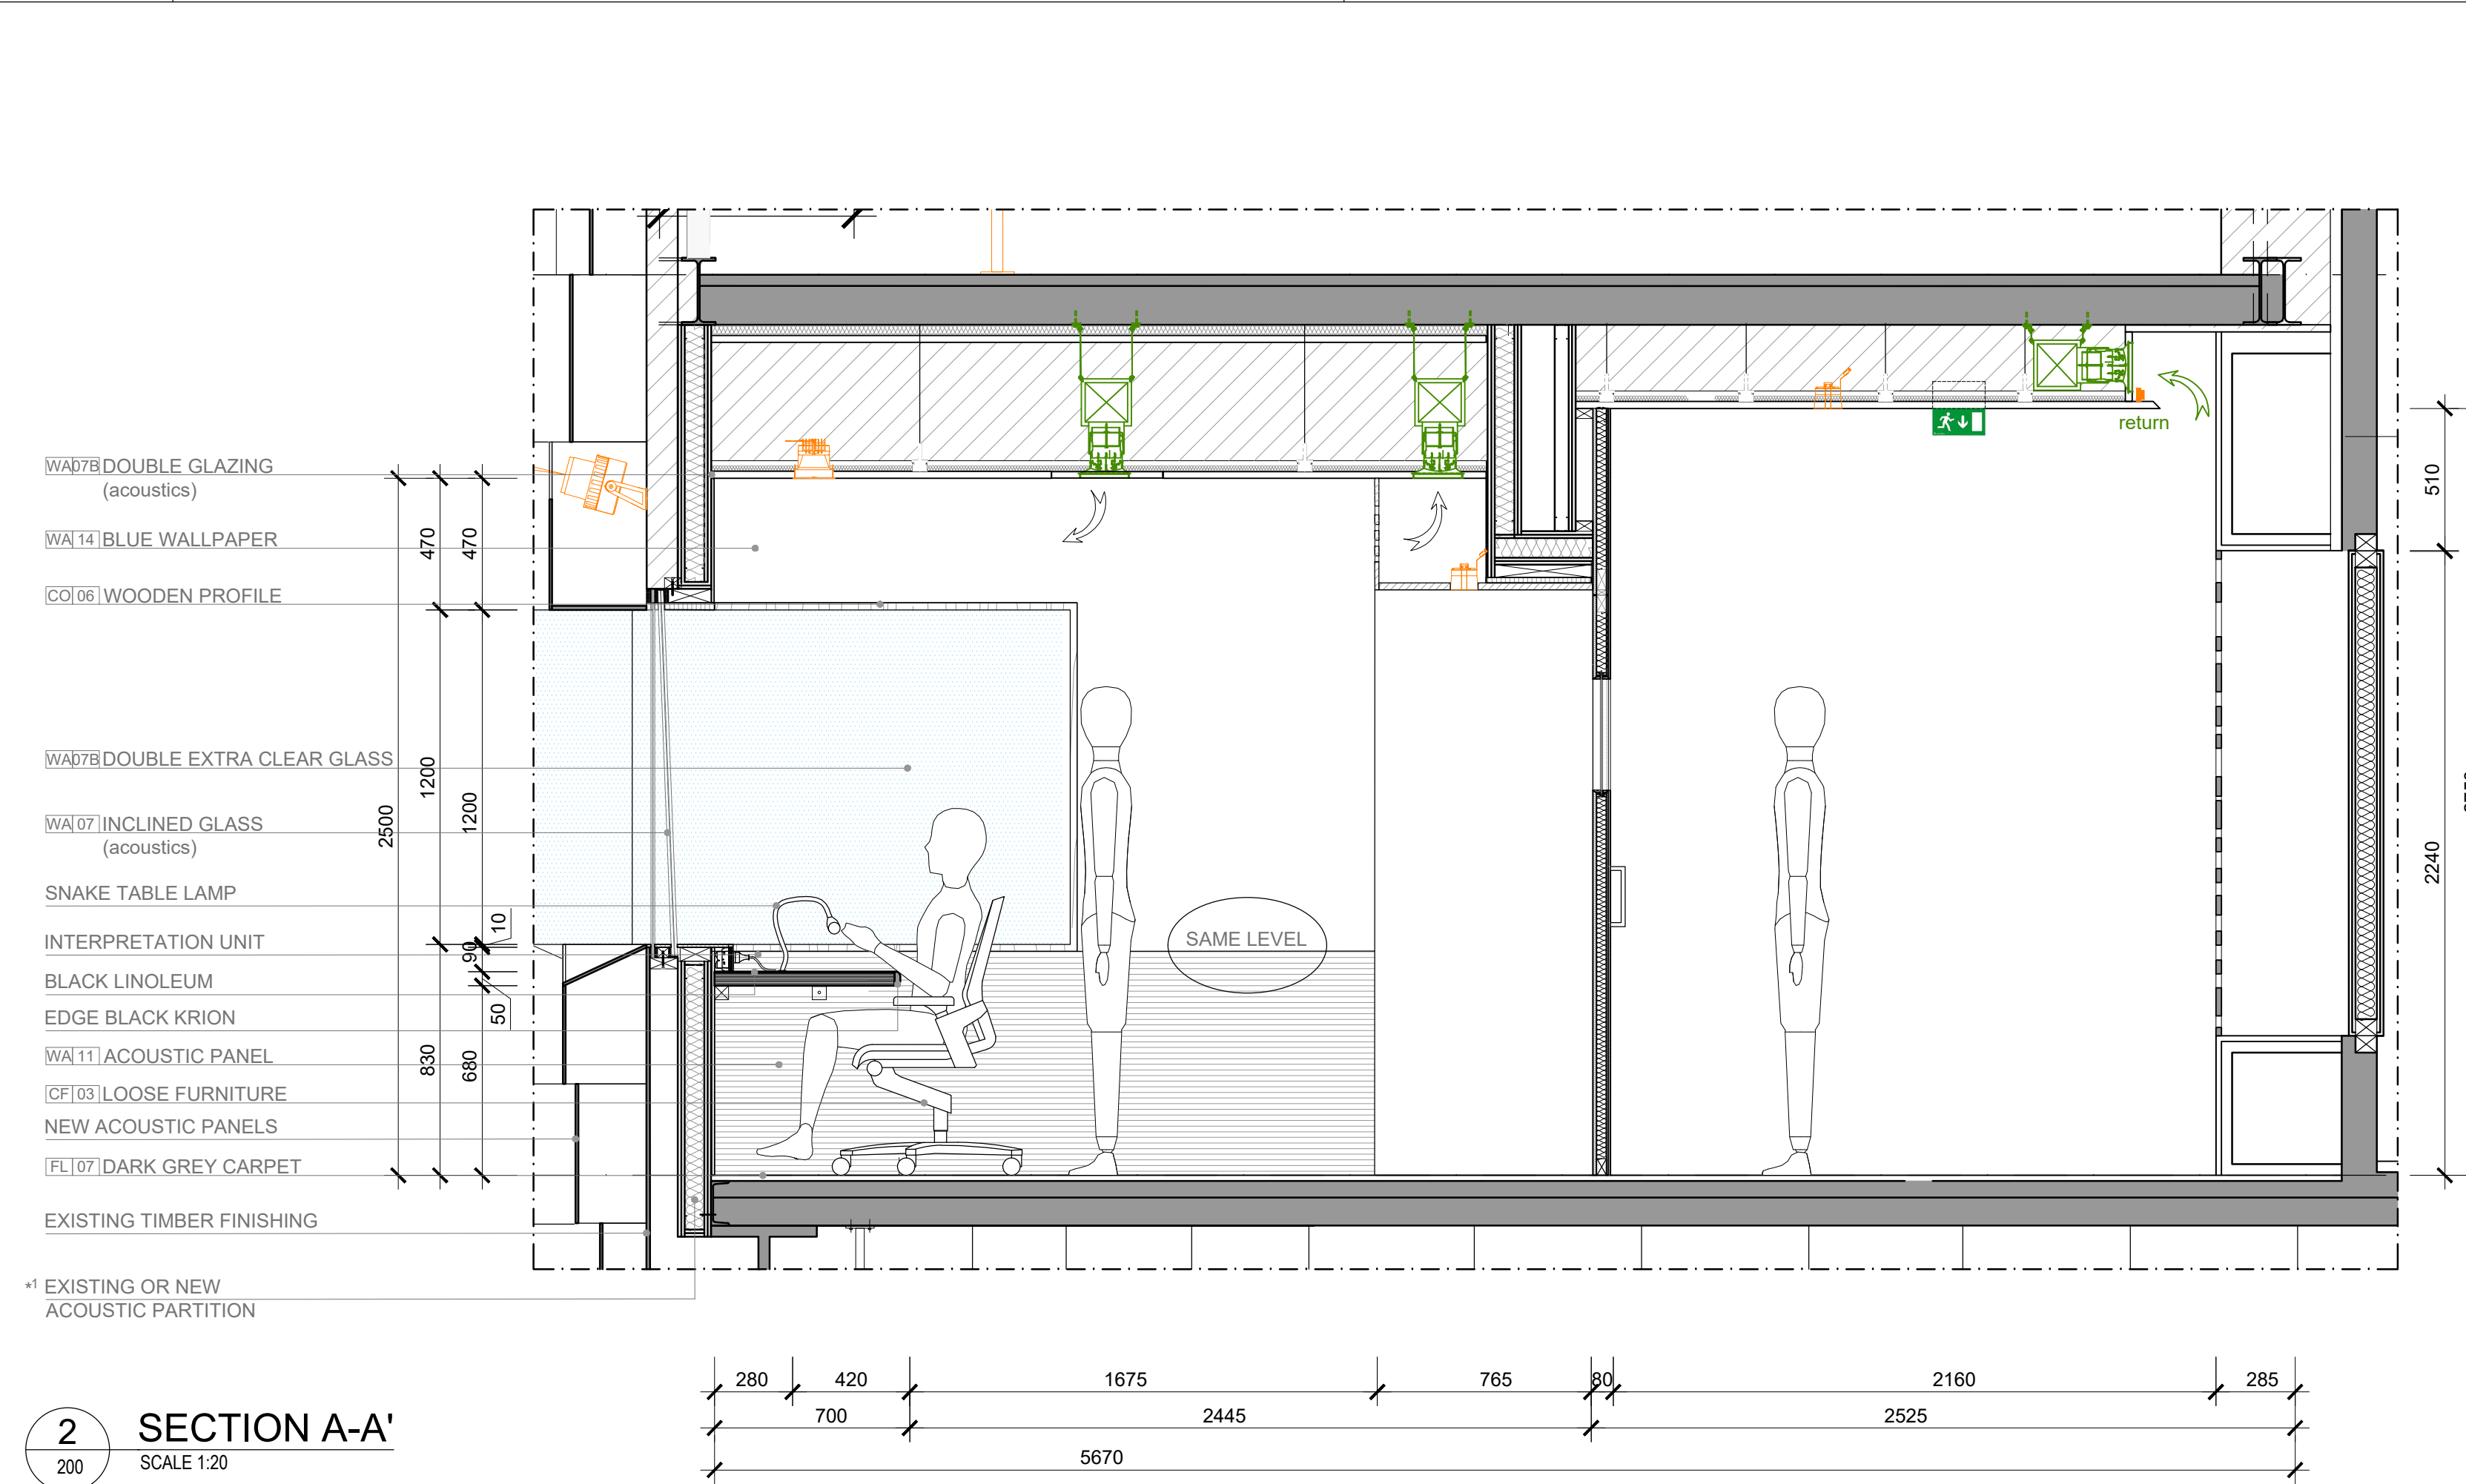


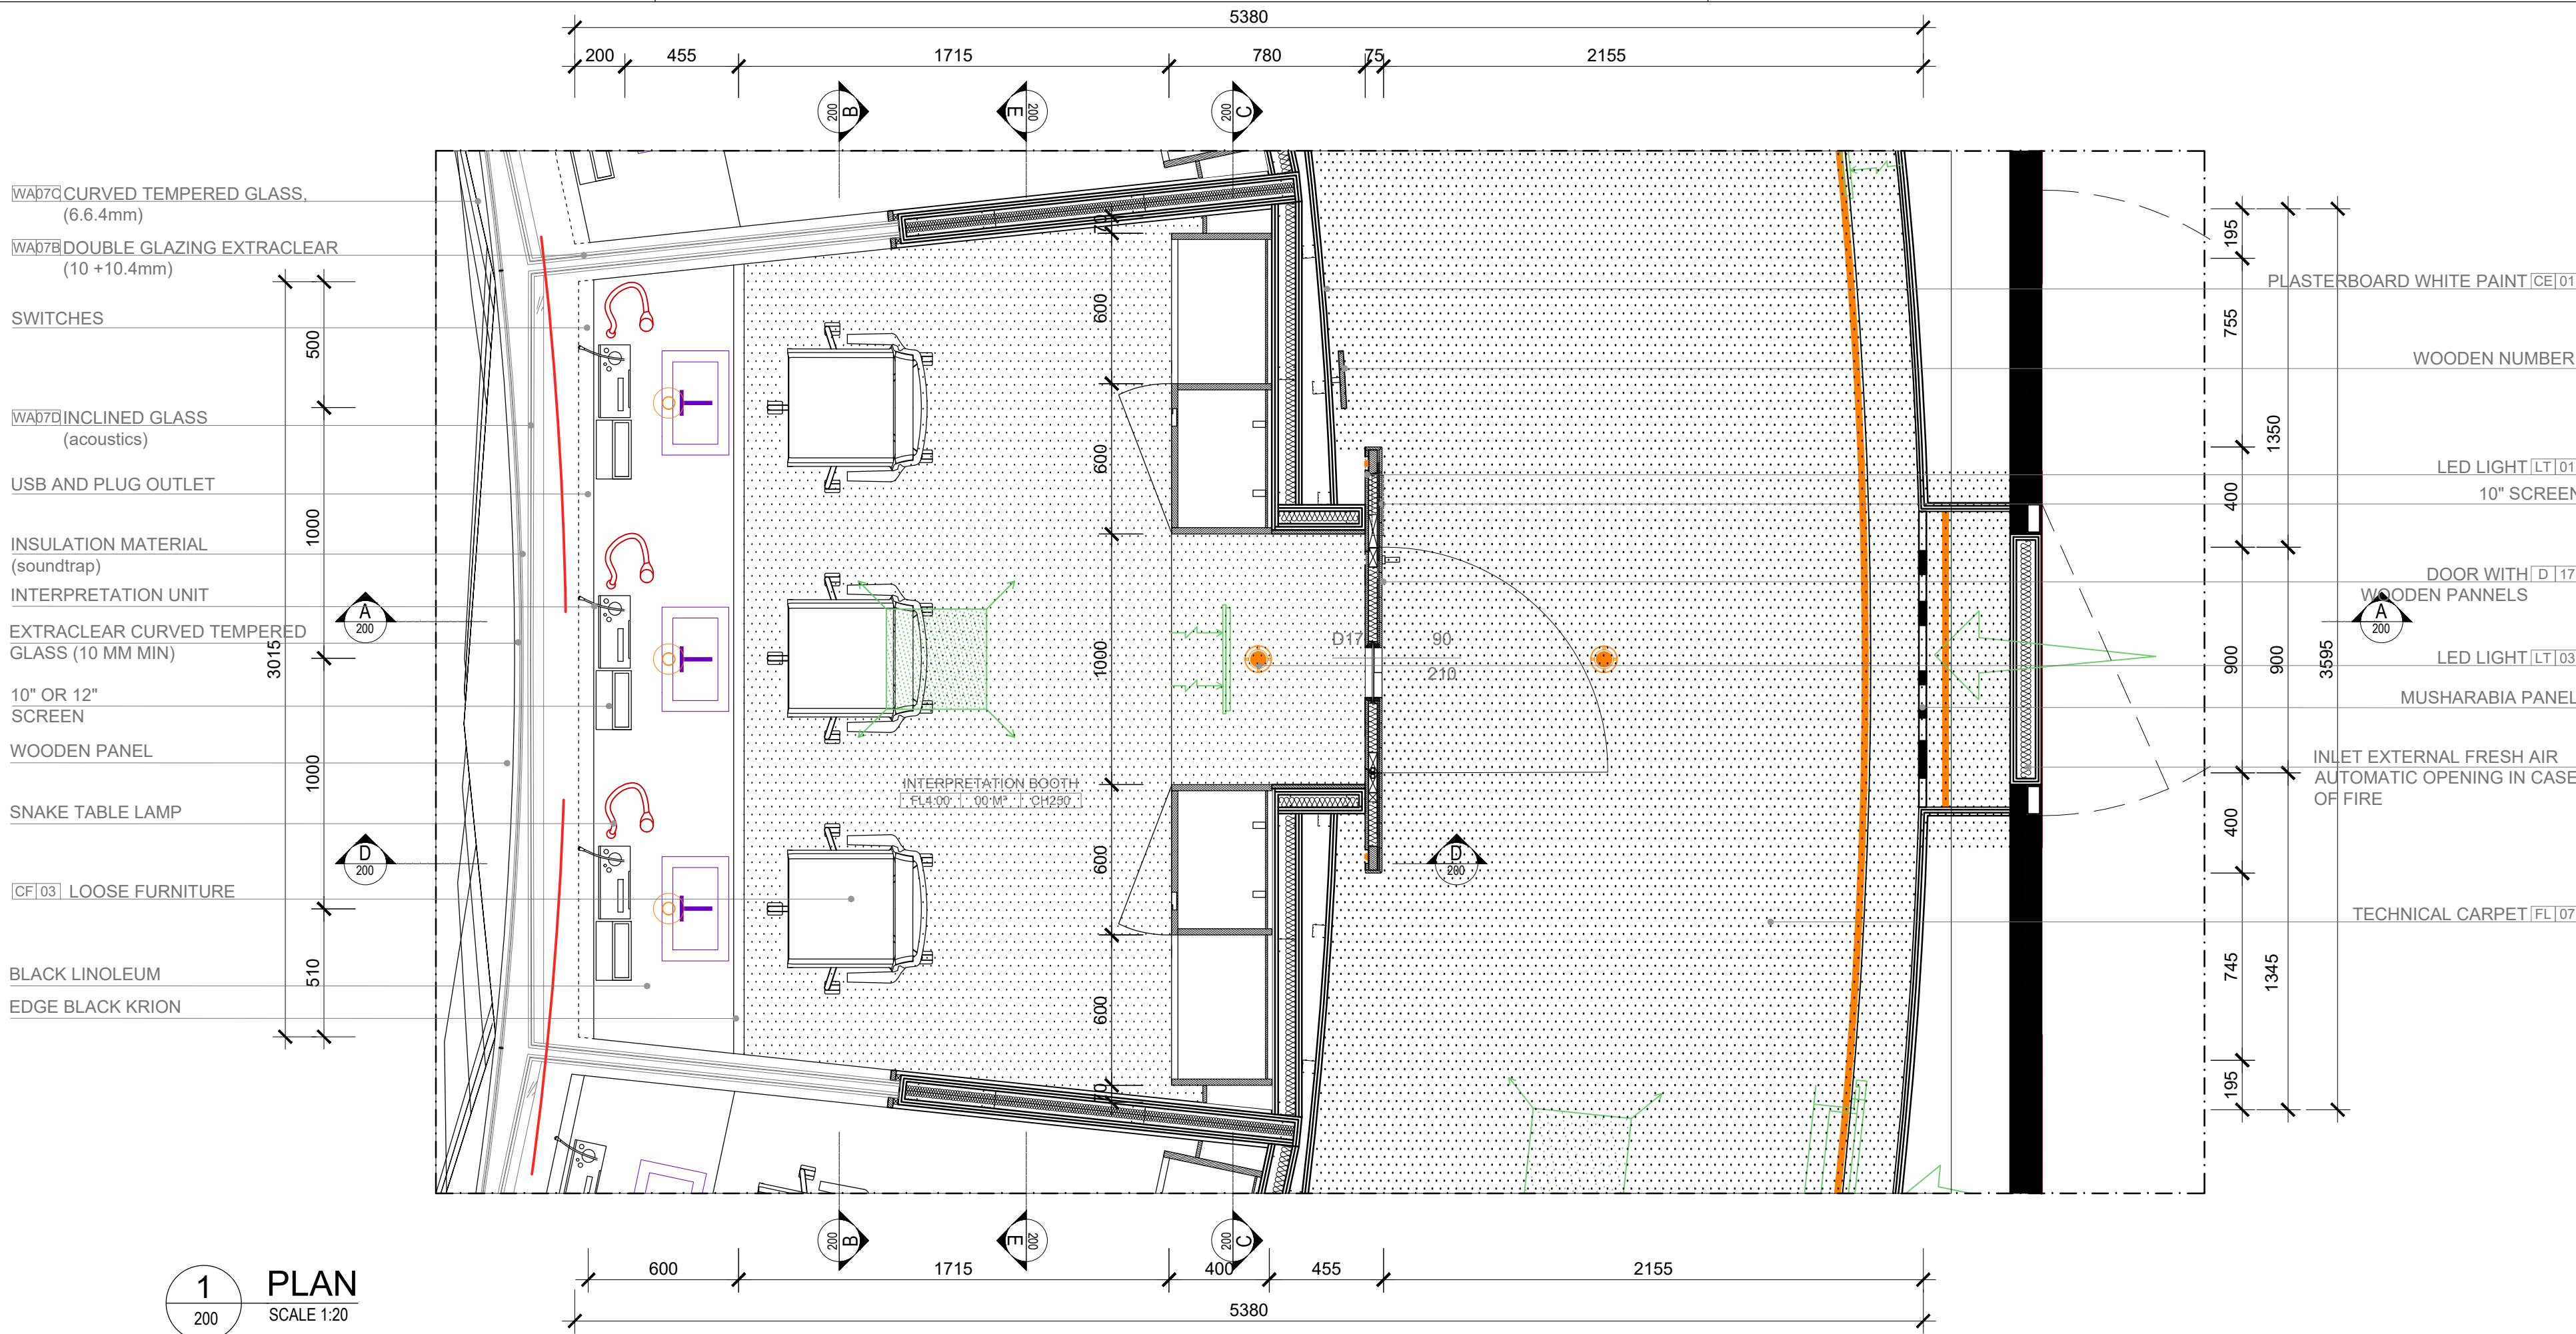

KEYPLAN-UPPER LEVEL

LEGEND: CEILING LIGHTS

LEGEND: THERMIC AND AIR SYSTEM

LEGEND: AUDIO / VIDEO

LEGEND: HYDRAULIC SYSTEM

LEGEND: WALL FINISHING

LEGEND: CEILING FINISHING

THE DESIGN OF THIS SIMULTANEOUS INTERPRETING PERMANENT BOOTHS IS RESPECTING THE INTERNATIONAL STANDARD REQUIREMENTS ISO 2603:2016 (E)

*1 TO BE CONFIRMED AFTER DEMOLITION AND REMOVALS

GENERAL NOTES

Architect: Peia Associati s.r.l.

Engineering: AI Engineering s.r.l.

Client: QATAR MINISTRY OF FOREIGN AFFAIRS

Project: Permanent Mission of the State of Qatar to the United Nations Office in Geneva

Project Phase: DETAIL PHASE

Drawing Subject: Detail - Interpretation Booth

Designed: Peia Associati

Date: 13/04/2018

Draft: LM

Scale: 1:20/1:50/A0 Sheet

Checked: GP

ID Dwg: GE_DET_IB

Review: 01

Sheet No.: A 200