
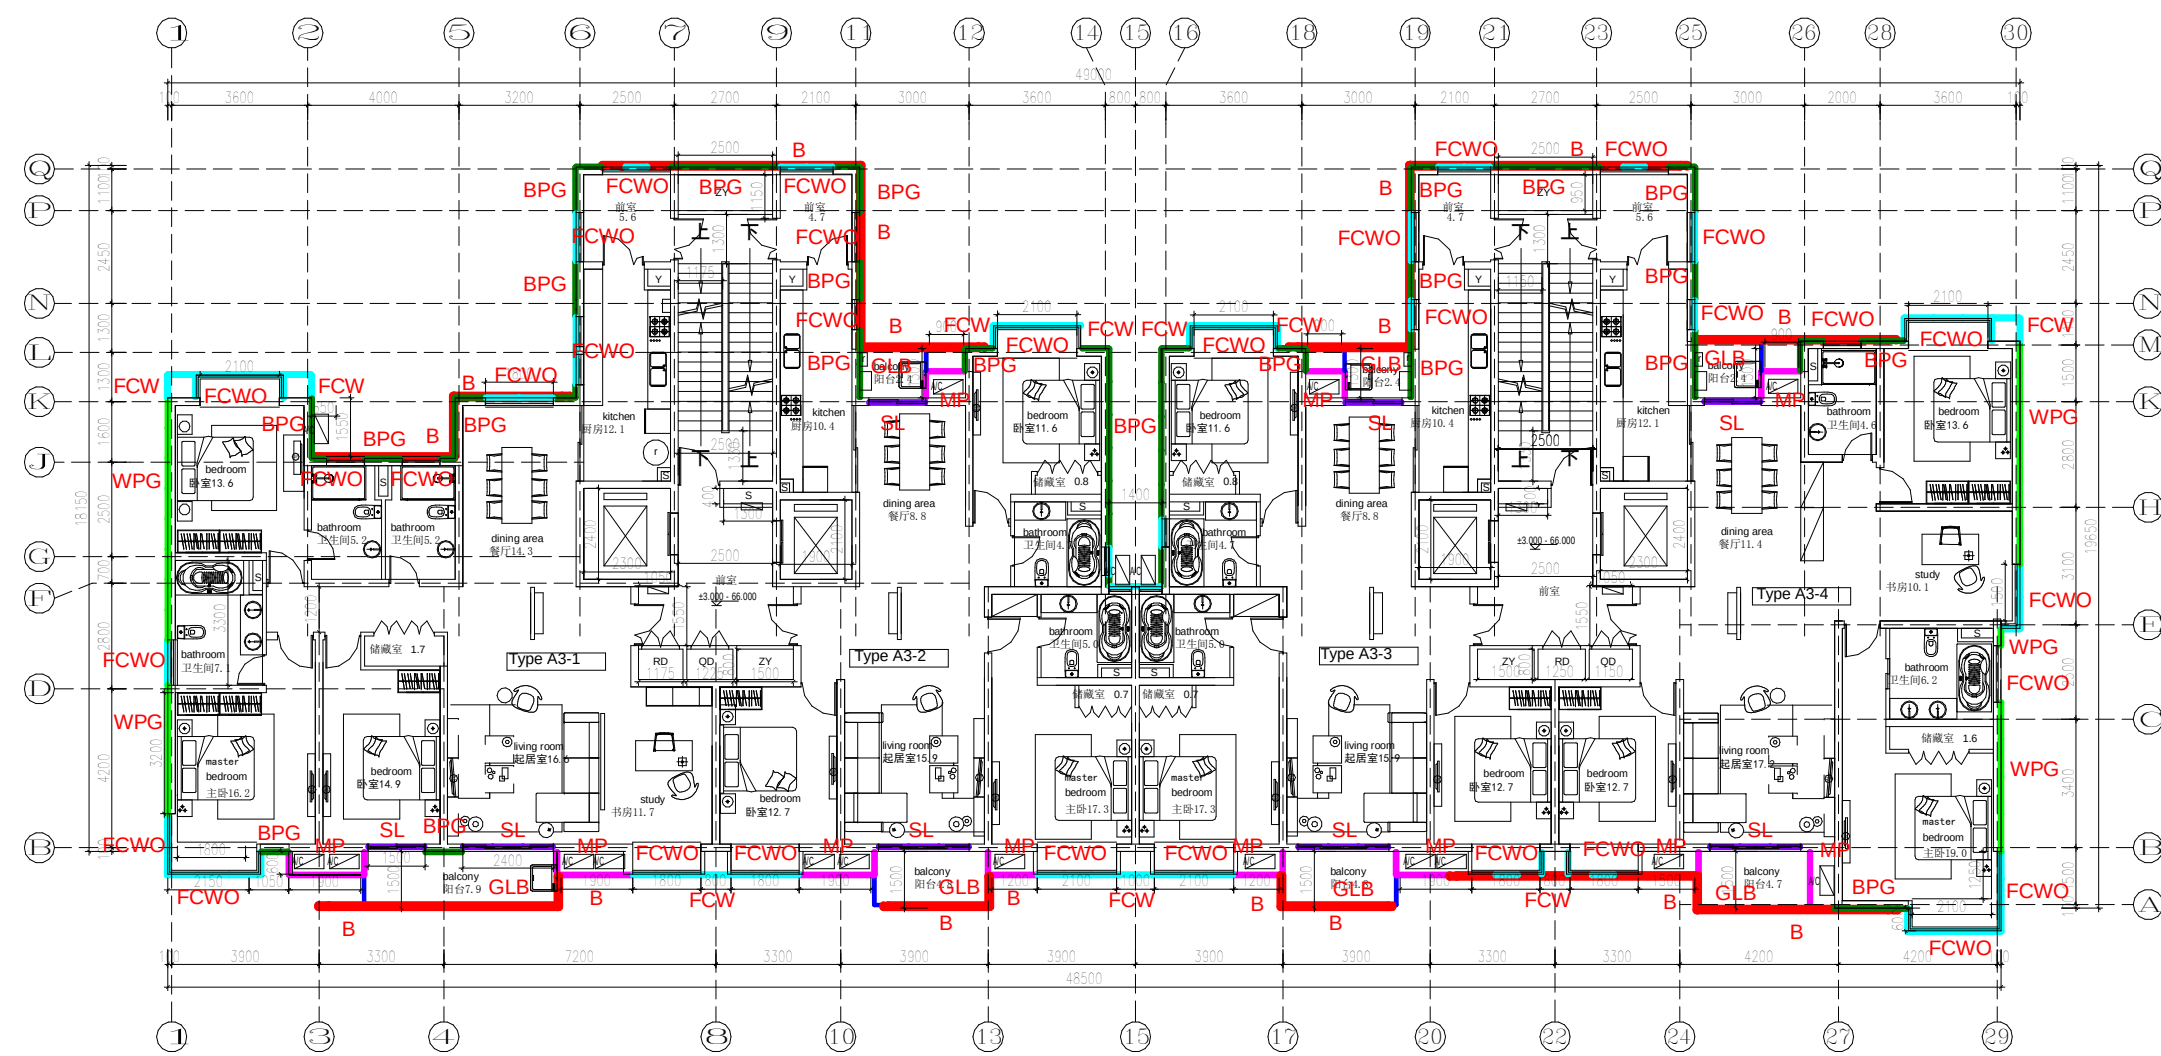
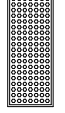
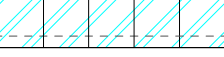
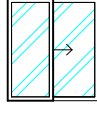
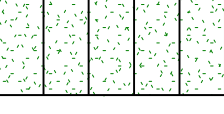


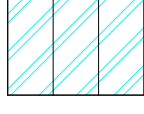

Legend:

 B	Balustrade (glass+white colour powder coating micro-perforated aluminum panels)		 MP	Dark colour powder coating micro-perforated aluminum panel (on balcony's technical area)	
 GLB	Glass balustrade		 SL	Sliding openings (on balconies)	
 BPG	Back paint glass		 FCW	Frameless curtain wall	
 WPG	White colour powder coating aluminum panels		 FCWO	Frameless curtain wall openings	

scale 1 : 200