

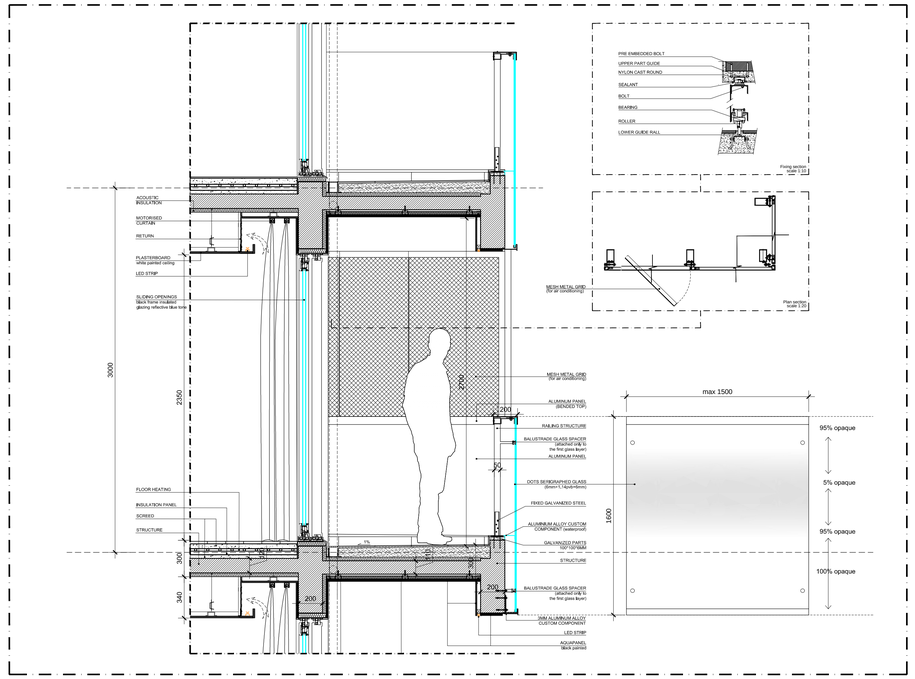



1 / 401 Section AA
SCALE: 1:20

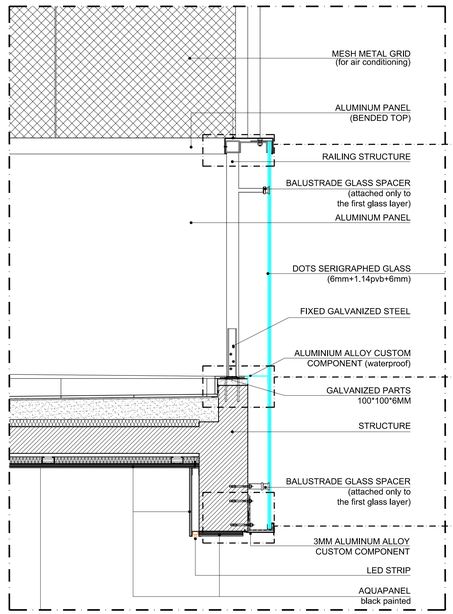

2a / 401 Section AA
SCALE: 1:10

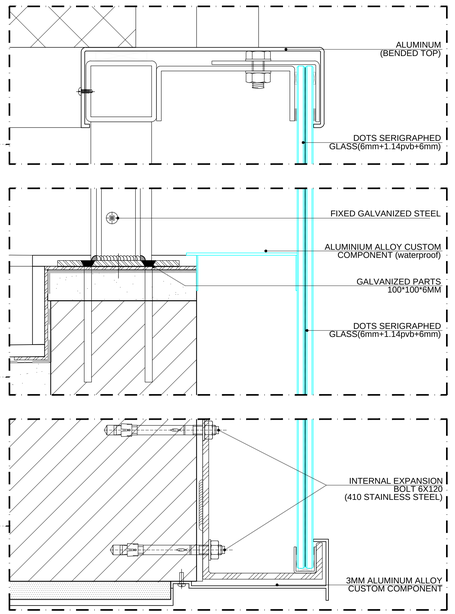


2b / 401 Section AA
SCALE: 1:2

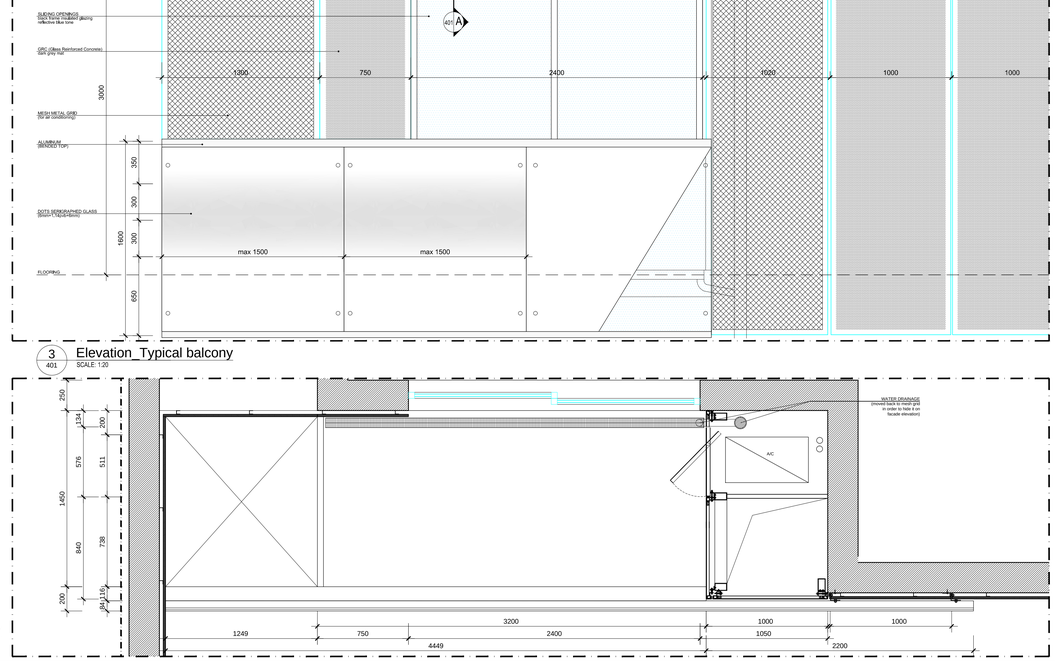

3 / 401 Elevation_Typical balcony
SCALE: 1:20

3a / 401 Plan_Typical balcony
SCALE: 1:20

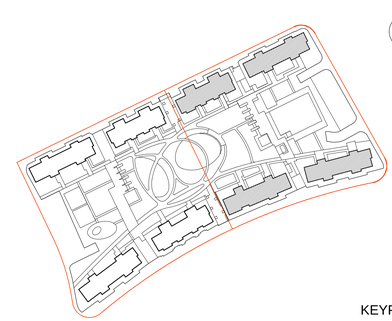

KEYPLAN

GENERAL NOTES:

A. ALL DIMENSIONS GIVEN ON THIS DRAWING ARE IN MILLIMETERS. DO NOT SCALE THE DRAWINGS. ANY DISCREPANCIES FOUND SHOULD BE REPORTED TO THE RESPONSIBLE ARCHITECT OR ENGINEER IMMEDIATELY.

B. IT IS THE RESPONSIBILITY OF THE CONTRACTOR OR BUILDERS TO ASCERTAIN AND CONFIRM THAT ALL DIMENSIONS SHOWN IN THESE DRAWINGS SHALL COMPLY WITH THE SITE DIMENSIONS AND LEVELS PRIOR TO PREPARING DRAWINGS AND EXECUTING THE WORKS.

C. ALL MEASUREMENT MUST BE VERIFIED AND CONFIRMED AT CONSTRUCTION SITE.

D. ALL WORKS ARE TO BE CARRIED OUT TO LOCAL CODES OF CONSTRUCTIONS.

E. THIS DRAWINGS SHOULD BE READ IN CONJUNCTION WITH THE OTHER RELEVANT ARCHITECTURAL, STRUCTURAL, MECHANICAL AND ELECTRICAL DRAWINGS AND ALL RELEVANT SECTIONS OF THE SPECIFICATIONS.

F. EXACT LOCATION, SIZES AND DETAILS OF ELECTRO-MECHANICAL WALL OPENINGS SHALL BE COORDINATED WITH ELECTRO-MECHANICAL ENGINEERS.

G. DIMENSION AND LOCATION OF SERVICES SHALL BE COORDINATED WITH RESPECTIVE ARCHITECTURAL AND SERVICES DRAWINGS PRIOR TO COMMENCEMENT OF ANY WORK. ANY DISCREPANCY FOUND SHOULD BE BROUGHT TO THE NOTICE OF THE CONCERNED ENGINEER.

H. ALL MATERIALS MUST BE VERIFIED AND CONFIRMED BY PEIA ASSOCIATI SRL ON SHOP DRAWINGS AND SAMPLES BY CONTRACTOR.

I. REFER TO SCHEDULE OF FINISHES FOR FLOORS, WALLS AND CEILINGS.

J. ALL MATERIAL FINISHES AND WORMANSHIP SHOULD BE OF HIGH STANDARD QUALITY OF WORKS.

K. ALL TEXTURES AND COLORS SHOULD BE REFERED TO SCHEDULE OF FINISHES AND HAVE APPROVAL OF ARCHITECT.

LEGEND:

F.F.L. = FLOOR FINISHING LEVEL

Architect:
PEIA
Peia associati srl
Via Cadolini, 30 - 20137
Milano, Italy
Tel: +39 02 6598647
Fax: +39 02 36554984
e-mail: info@peiaassociati.it

Engineering:

Owner:
Yanfull (Shanghai) Co. Ltd.
78, Xin Zhen road
Qi Bao town
Min Hang district
Shanghai 201101
P.R. China

Project:
ROYAL GARDEN PHASE 3
Shanghai, China

Drawing Subject:
RG3_DETAIL_TYPICAL BALCONY SECTION

Designed:	Draft:	Checked:	Review:
Peia Associati s.r.l.	YW	GP	01
Date: 2016-05-13	Scale: vary @A1+ (1051x594mm)	ID Dwg: 1501_RG_RG3_DET	Sheet No.: 401

CAD File Ref: 1501_RG_RG3_DET_Details.dwg

COPYRIGHT LAW RULES THE USE AND COPYING OF THIS DOCUMENT

Printed Date & Time: May 13, 2016 - 10:29 am