




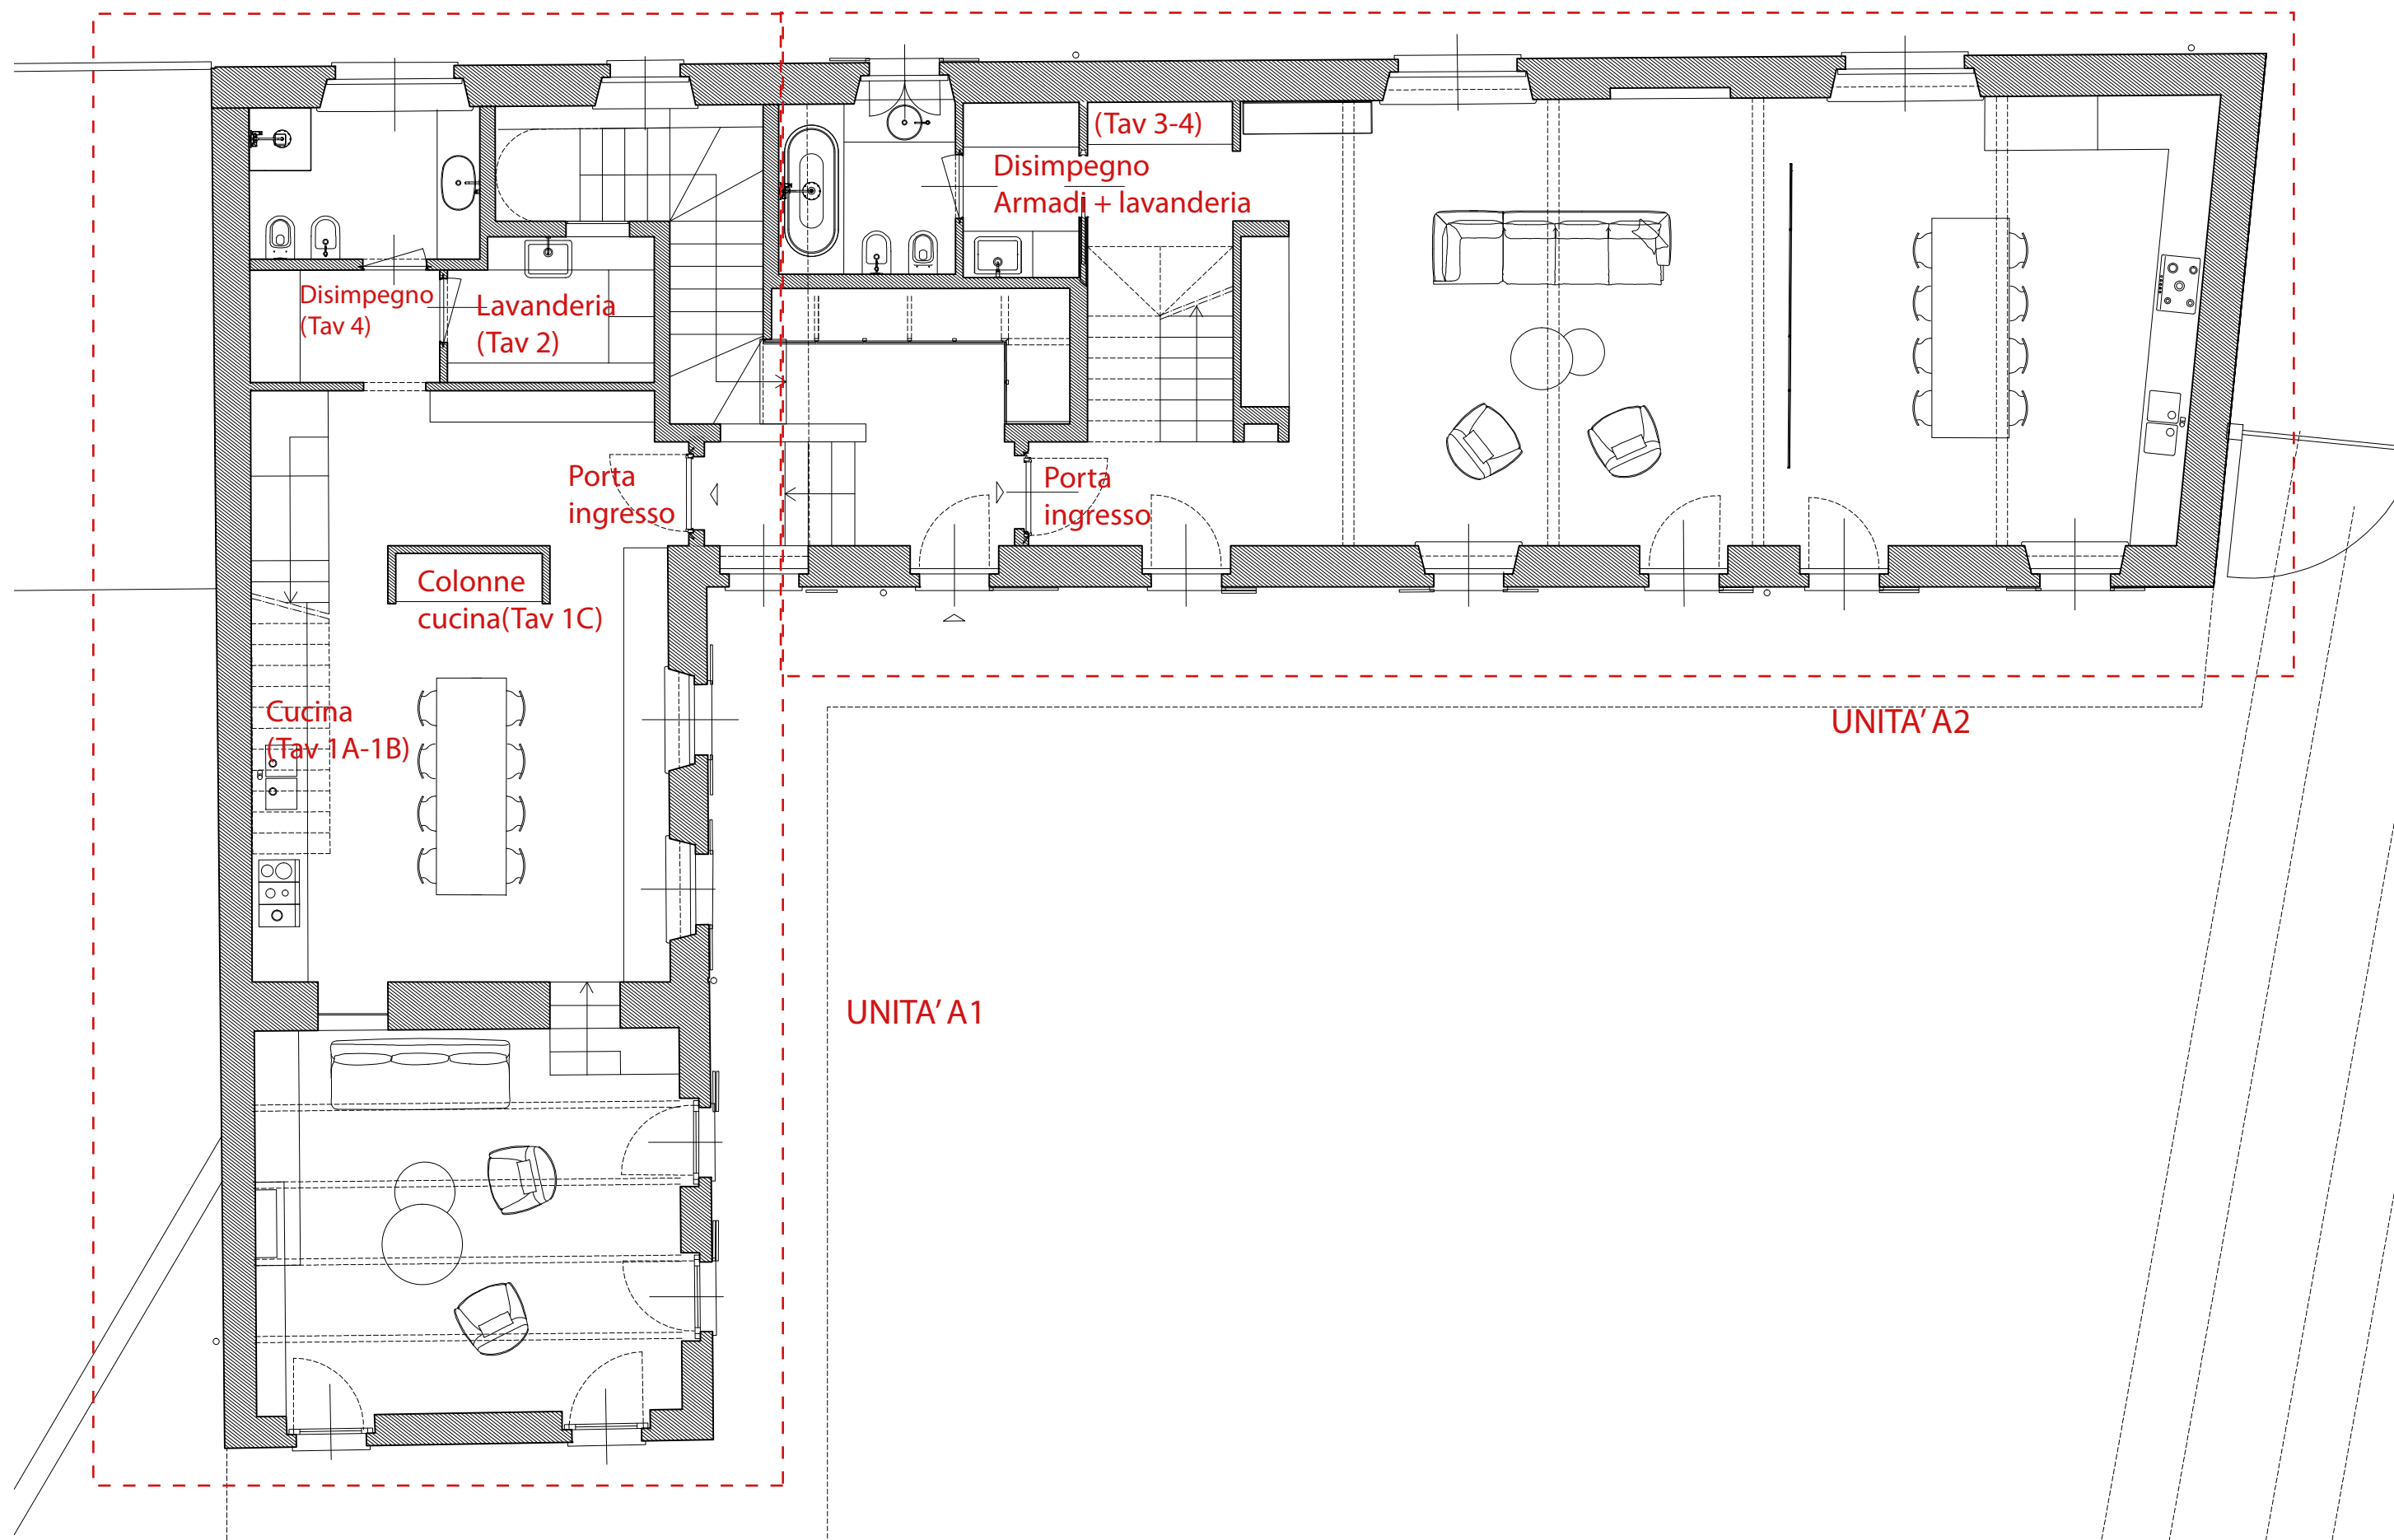


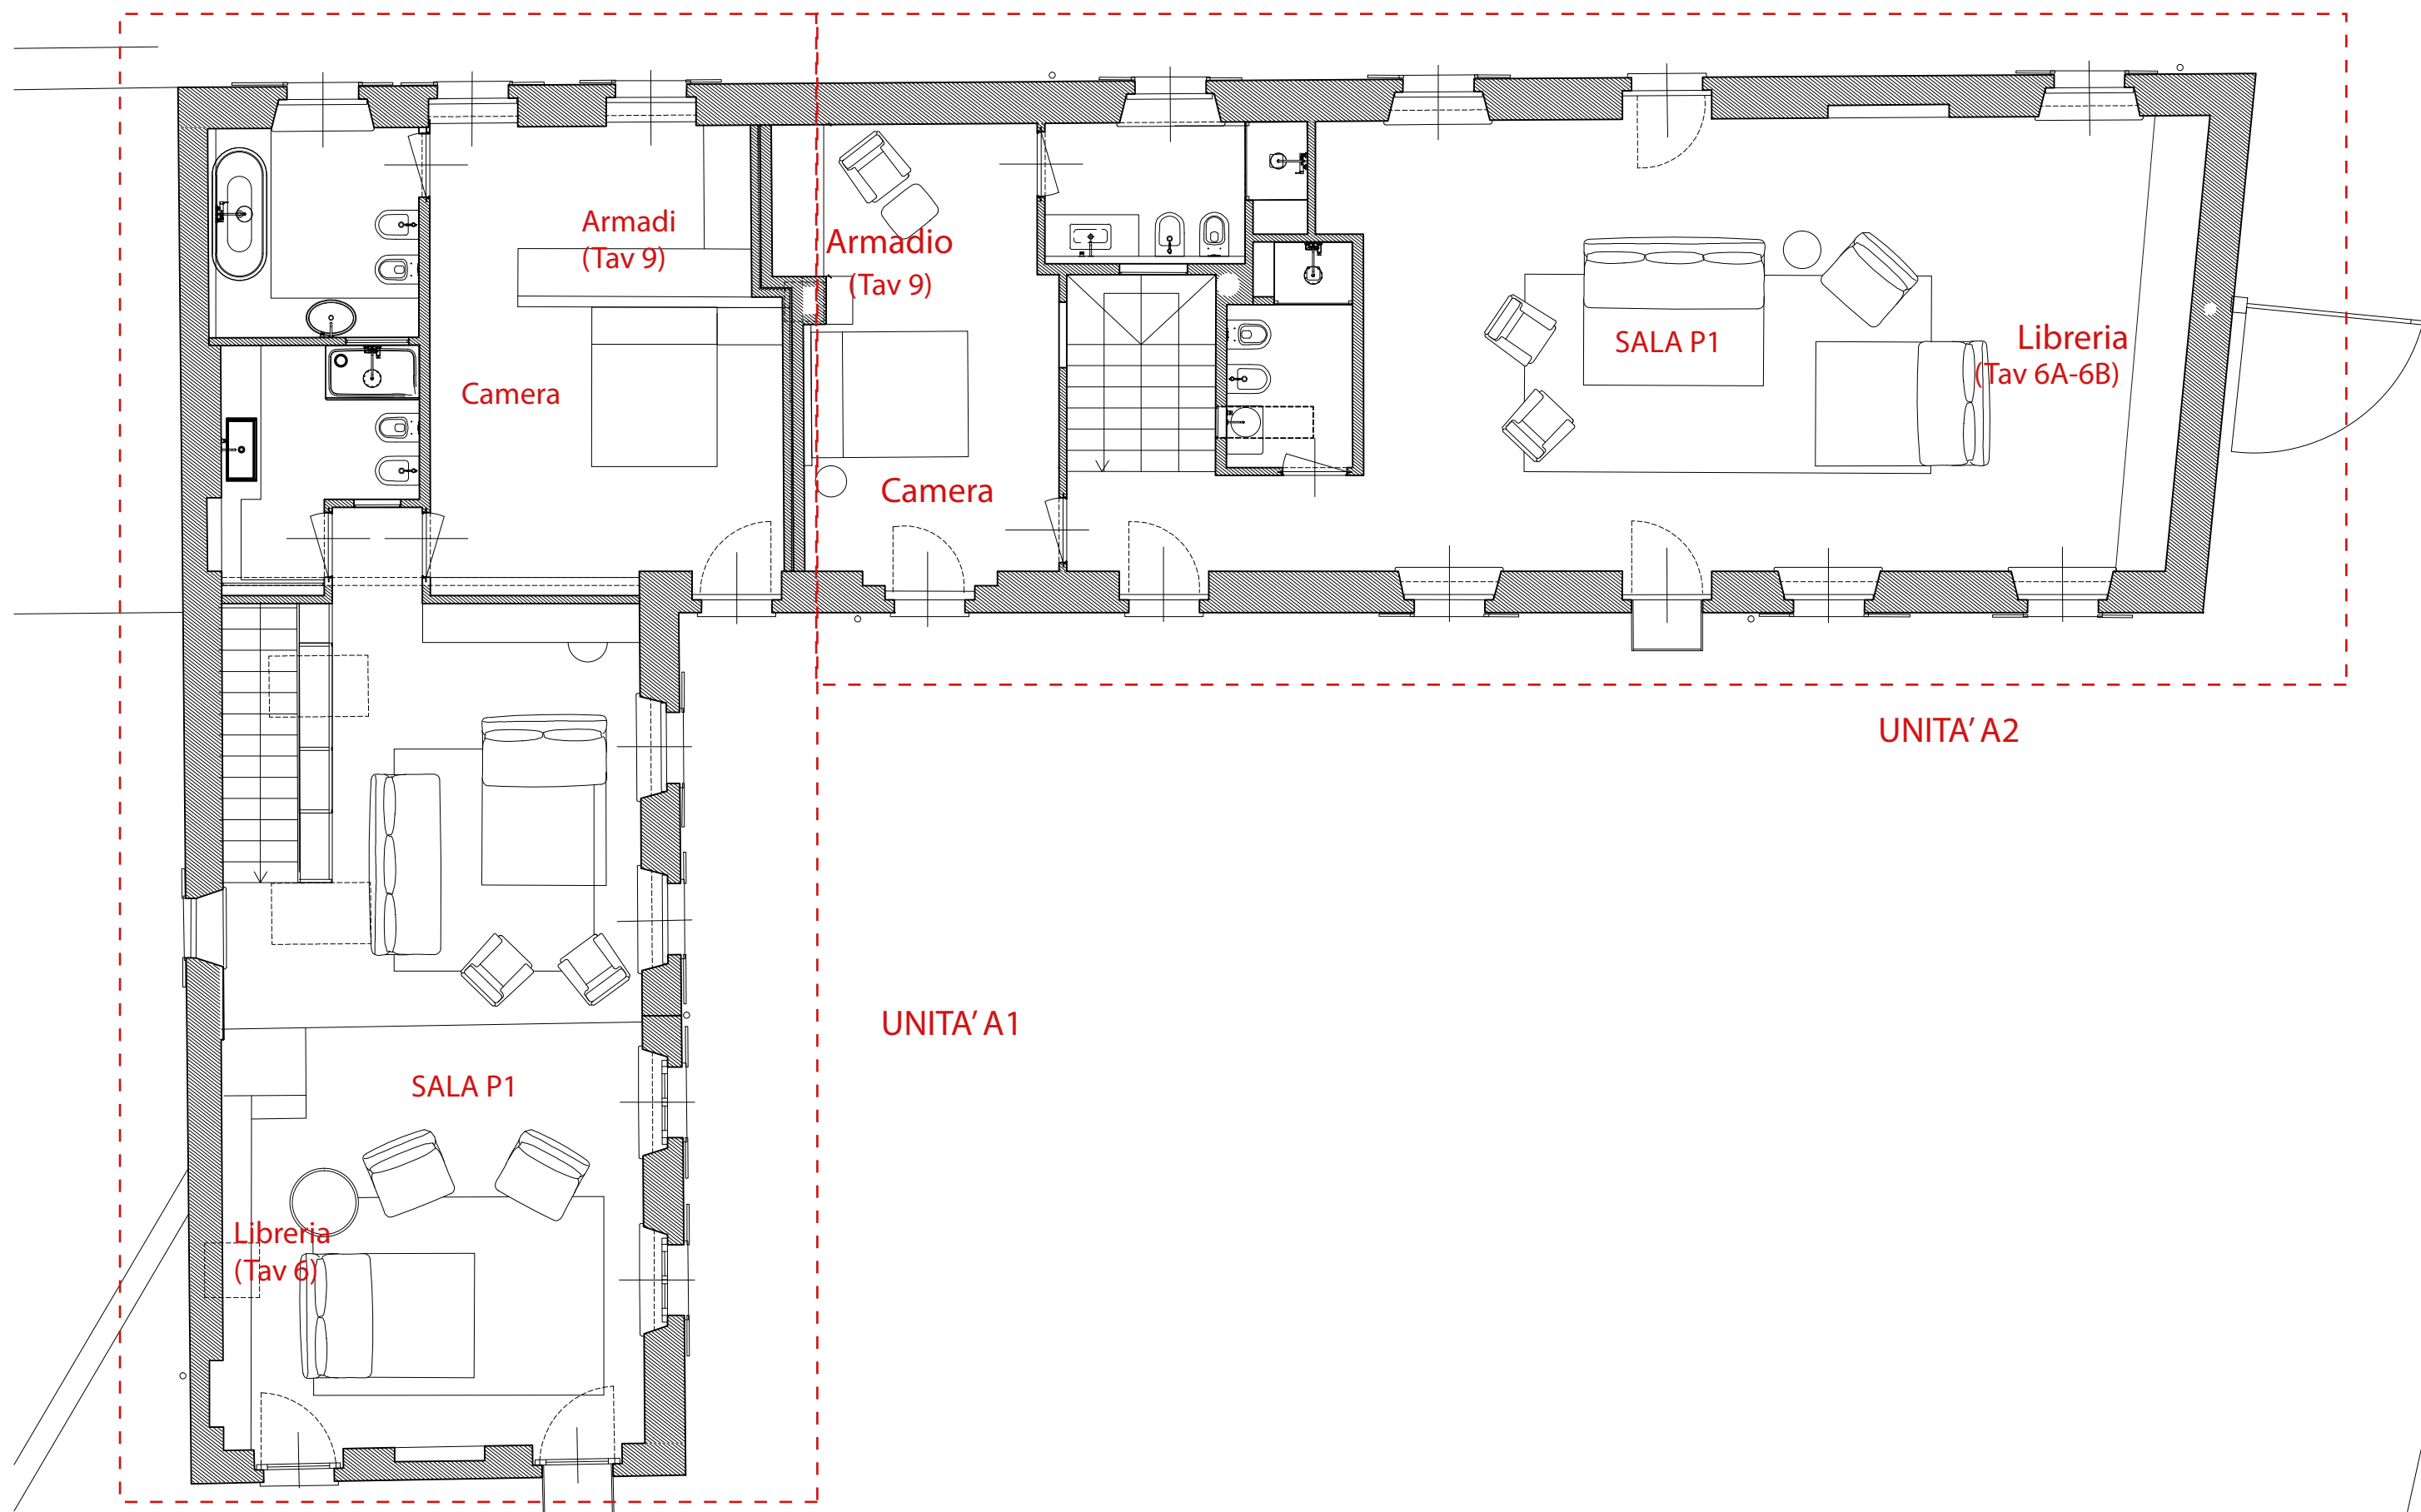

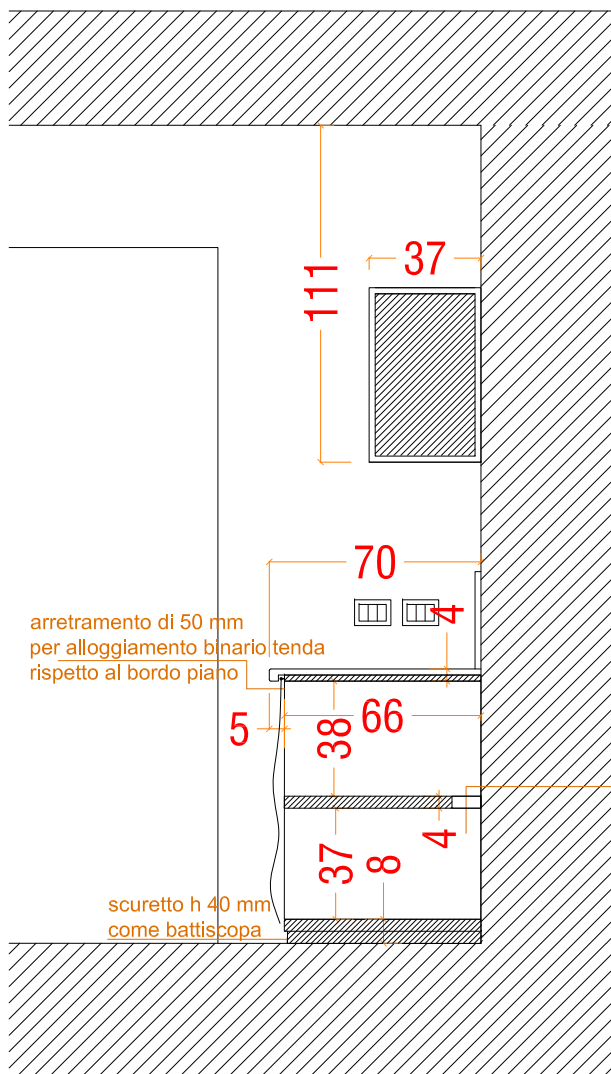


SEZIONE AA

N.B. tutte le dimensioni si intendono indicative, è necessario un rilievo esecutivo in cantiere per procedere alla produzione

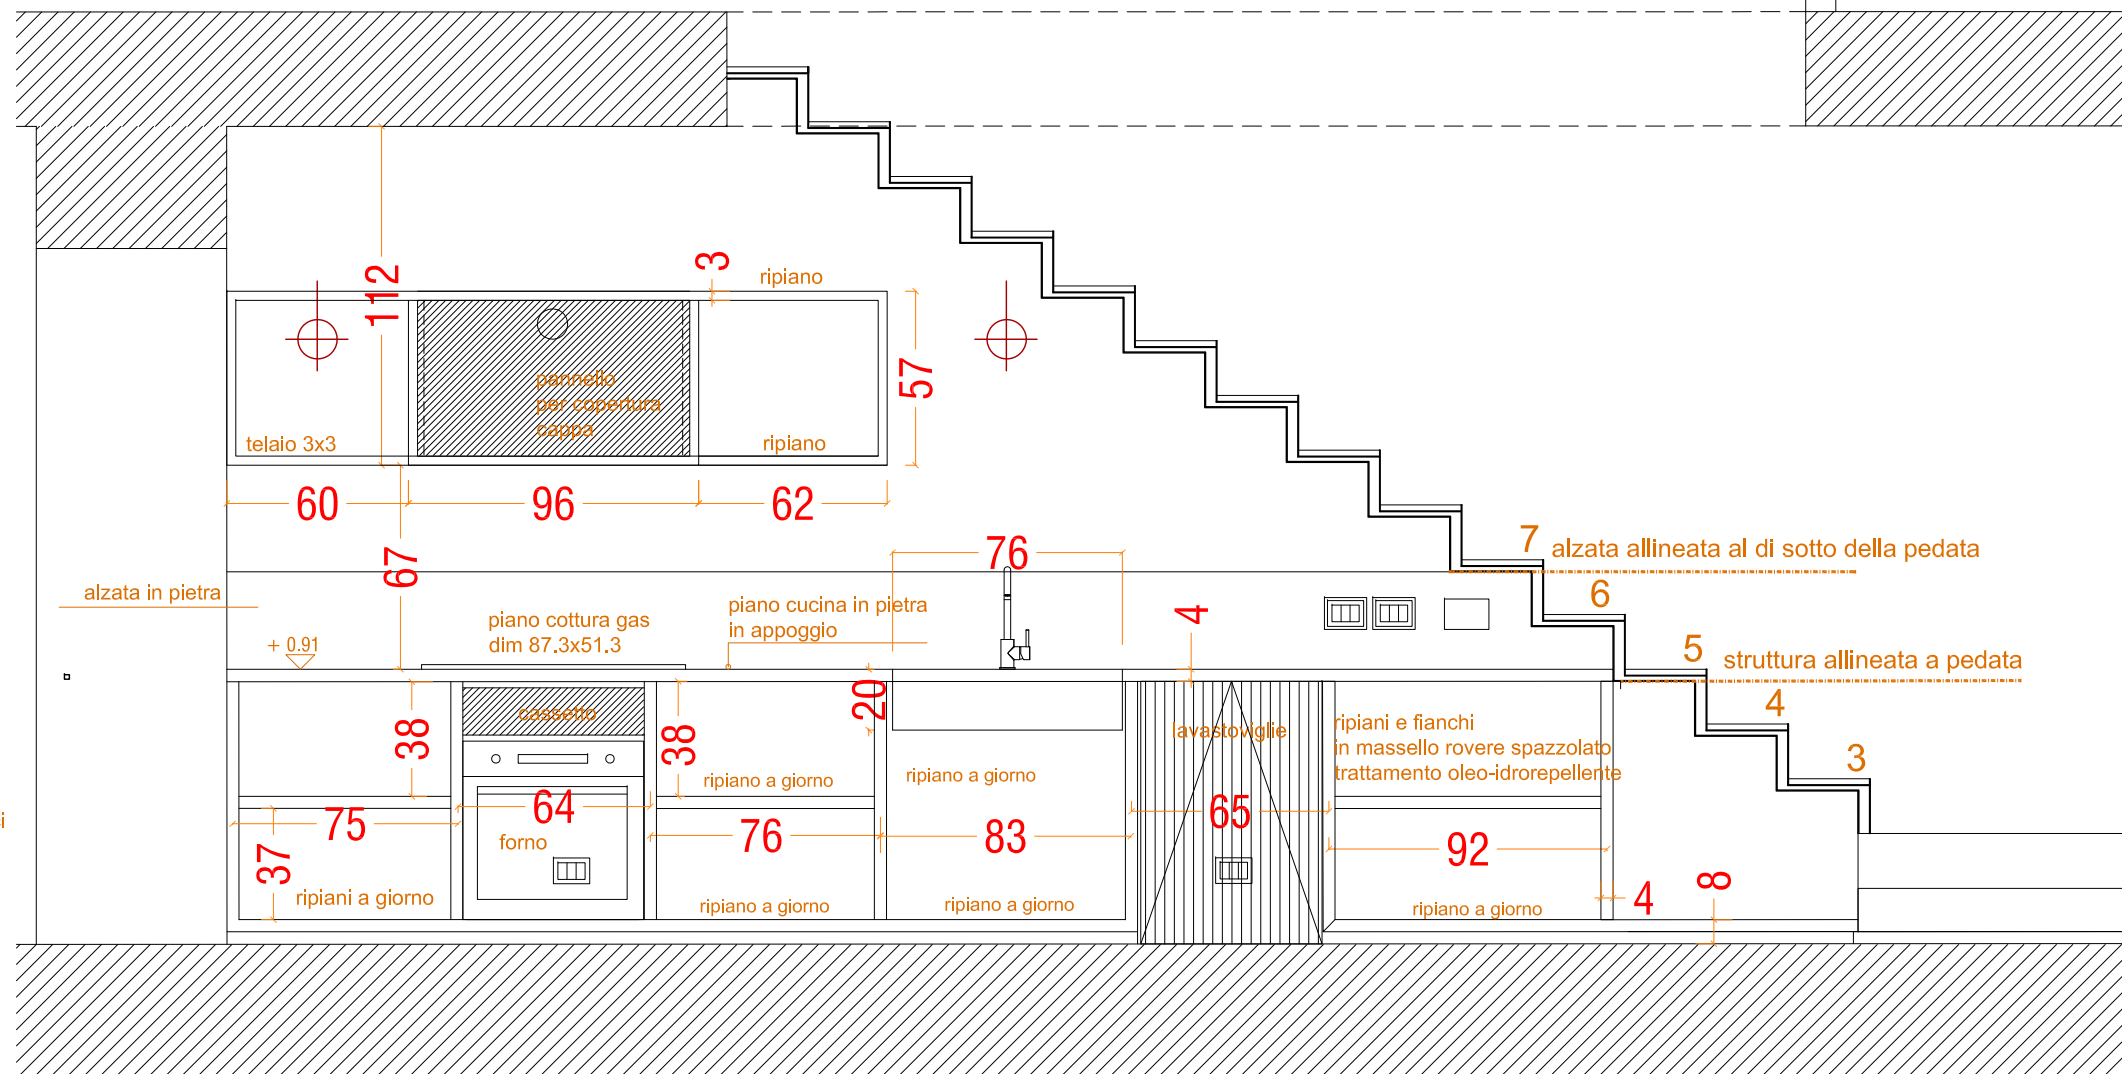


PROSPETTO

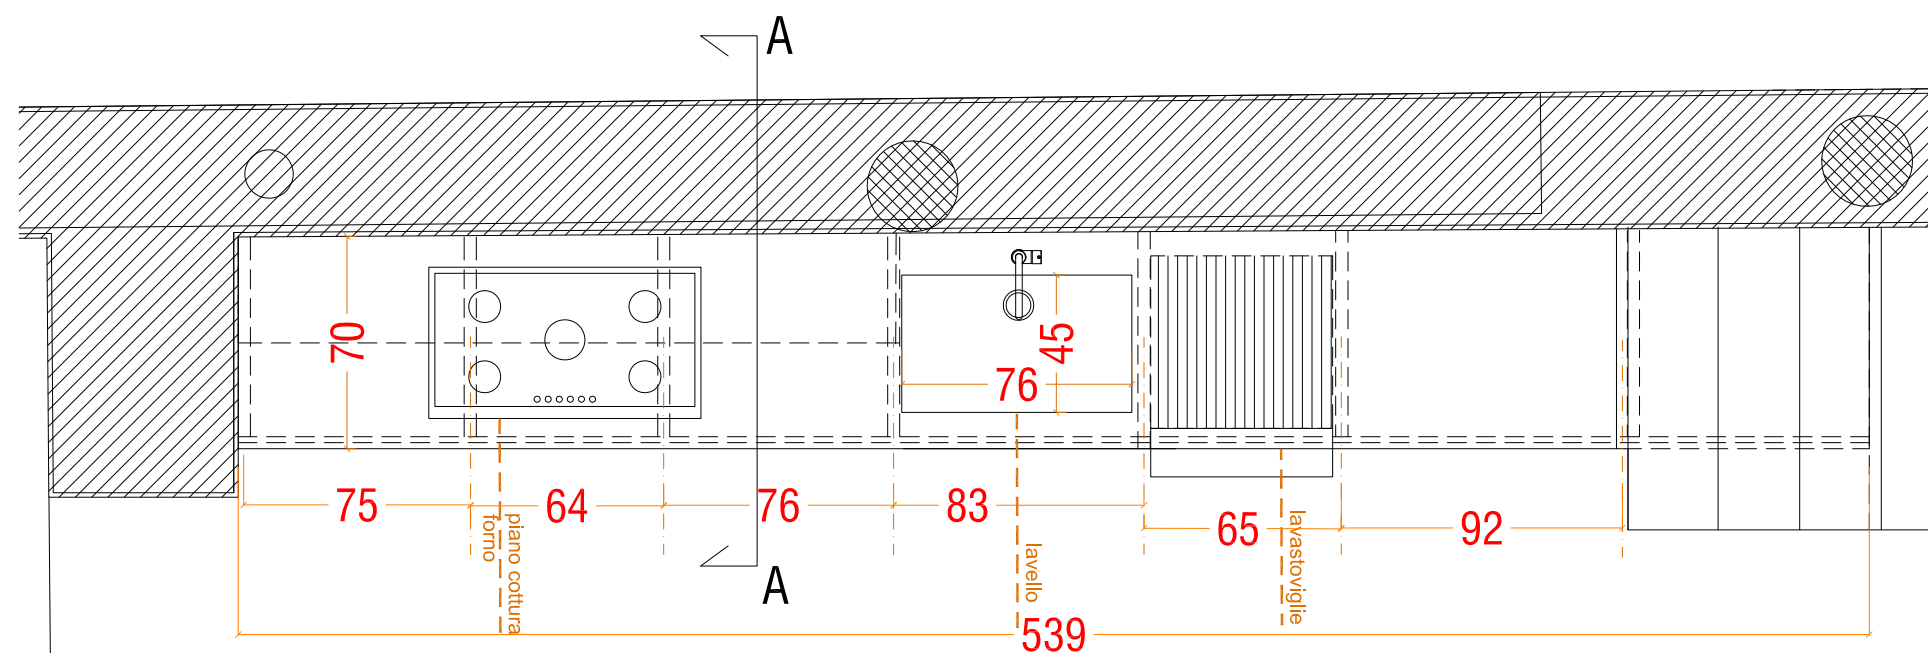


PIANTA

Strada Bionzo 20,
Costigliole d'Asti

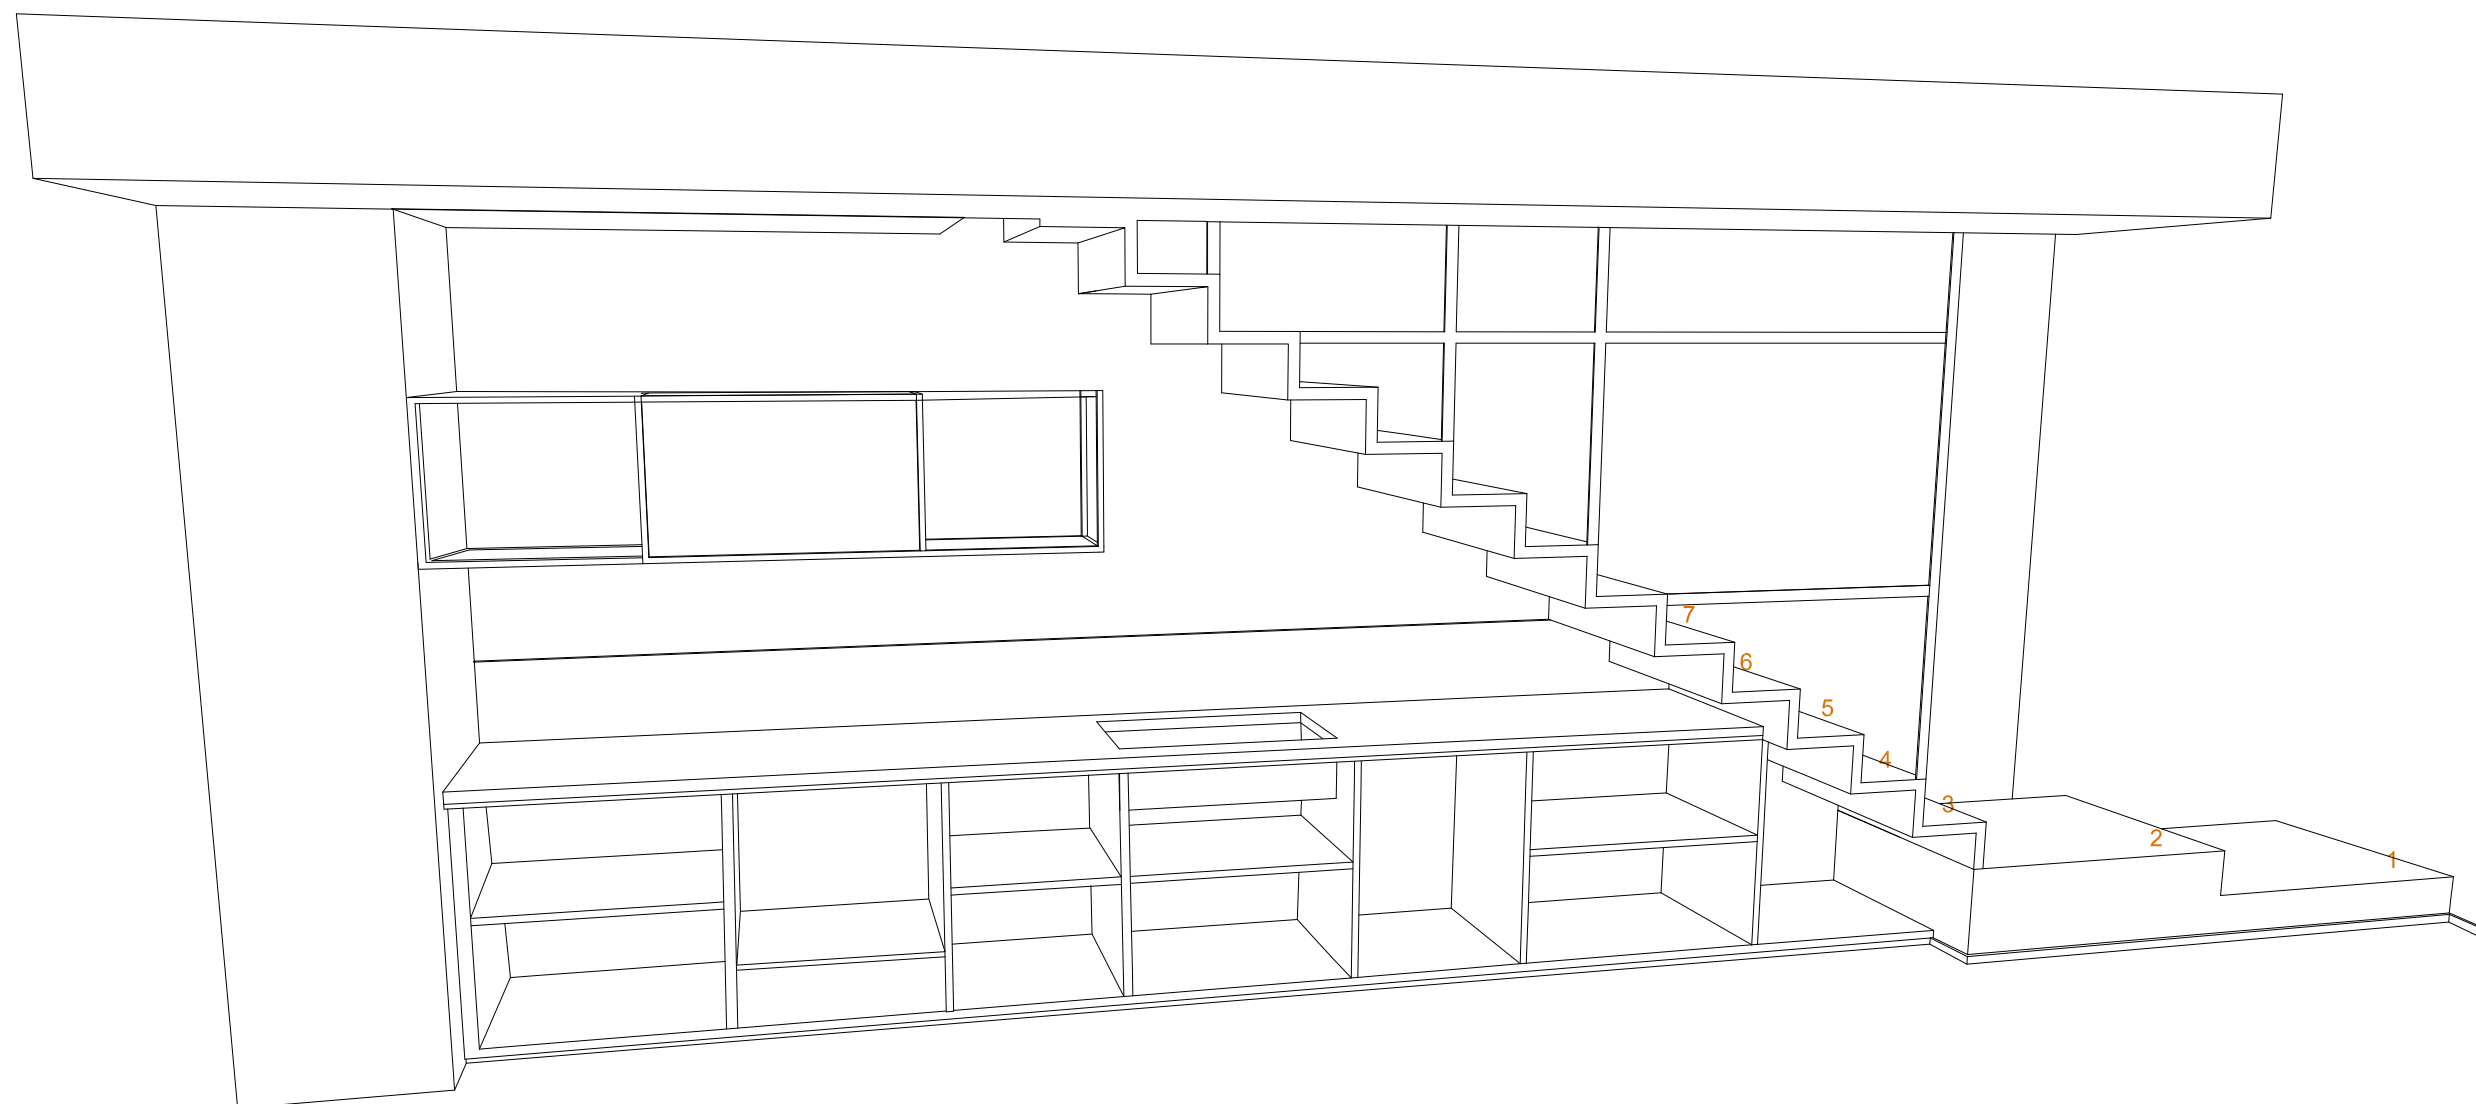








PROSPETTO RIPIANI

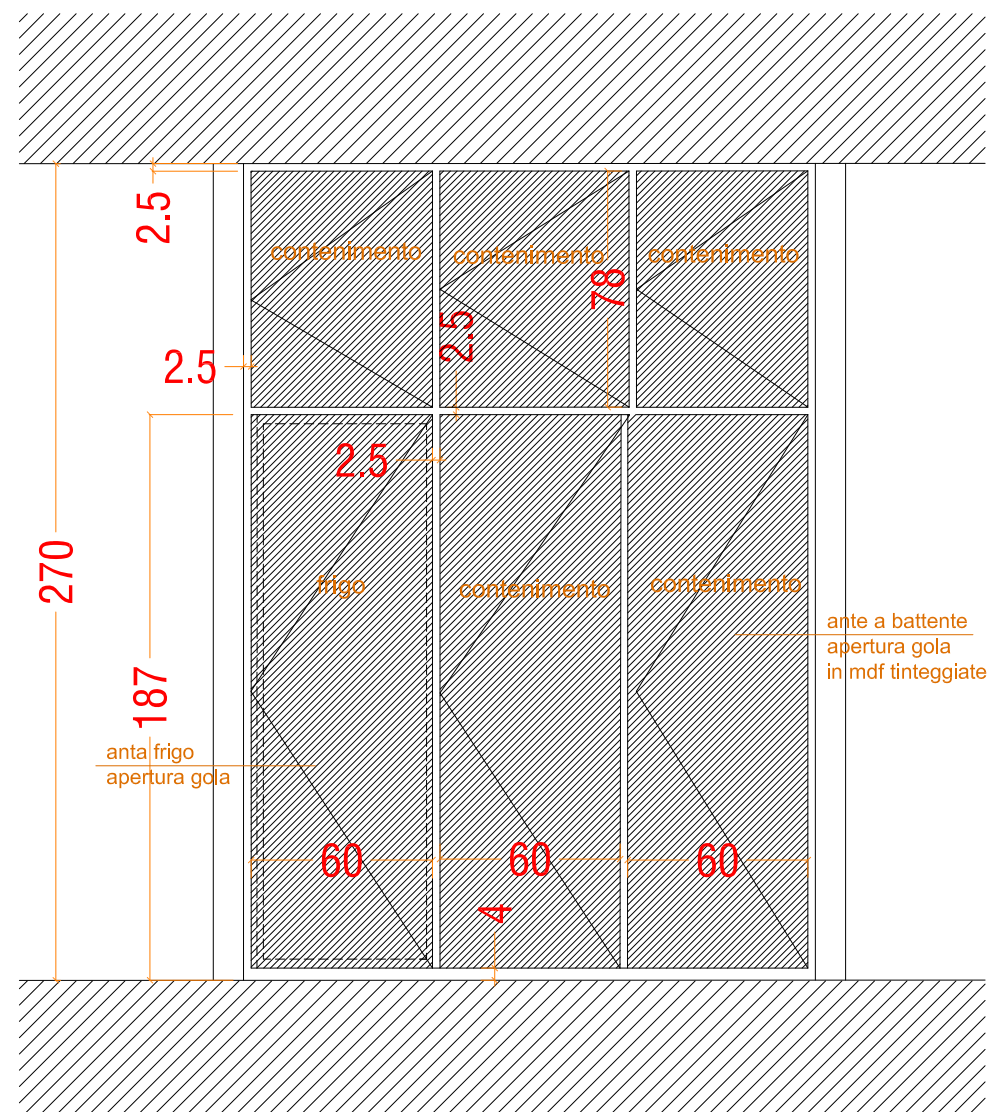


PROSPETTO ANTE

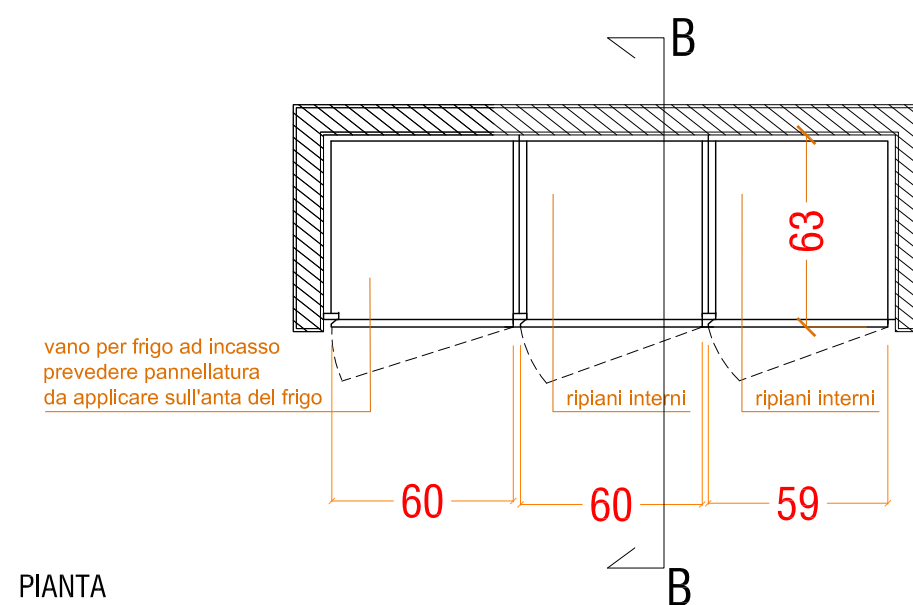

PIANTA

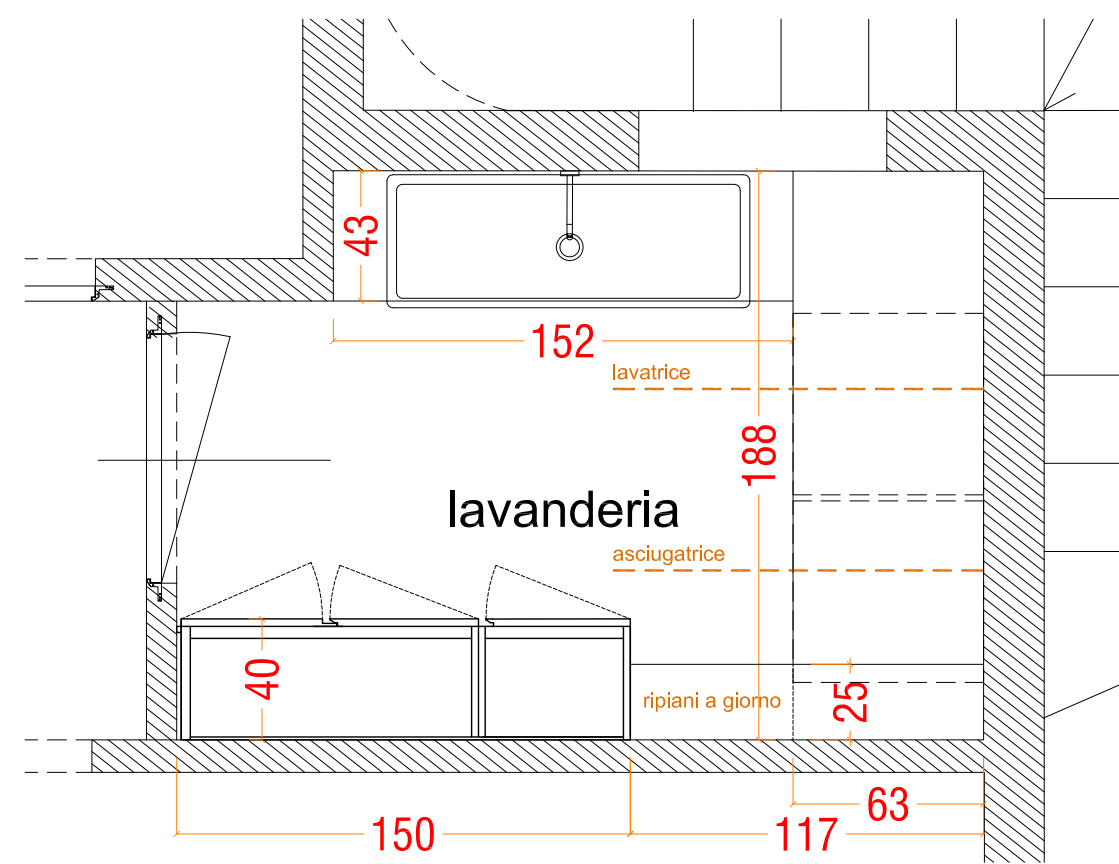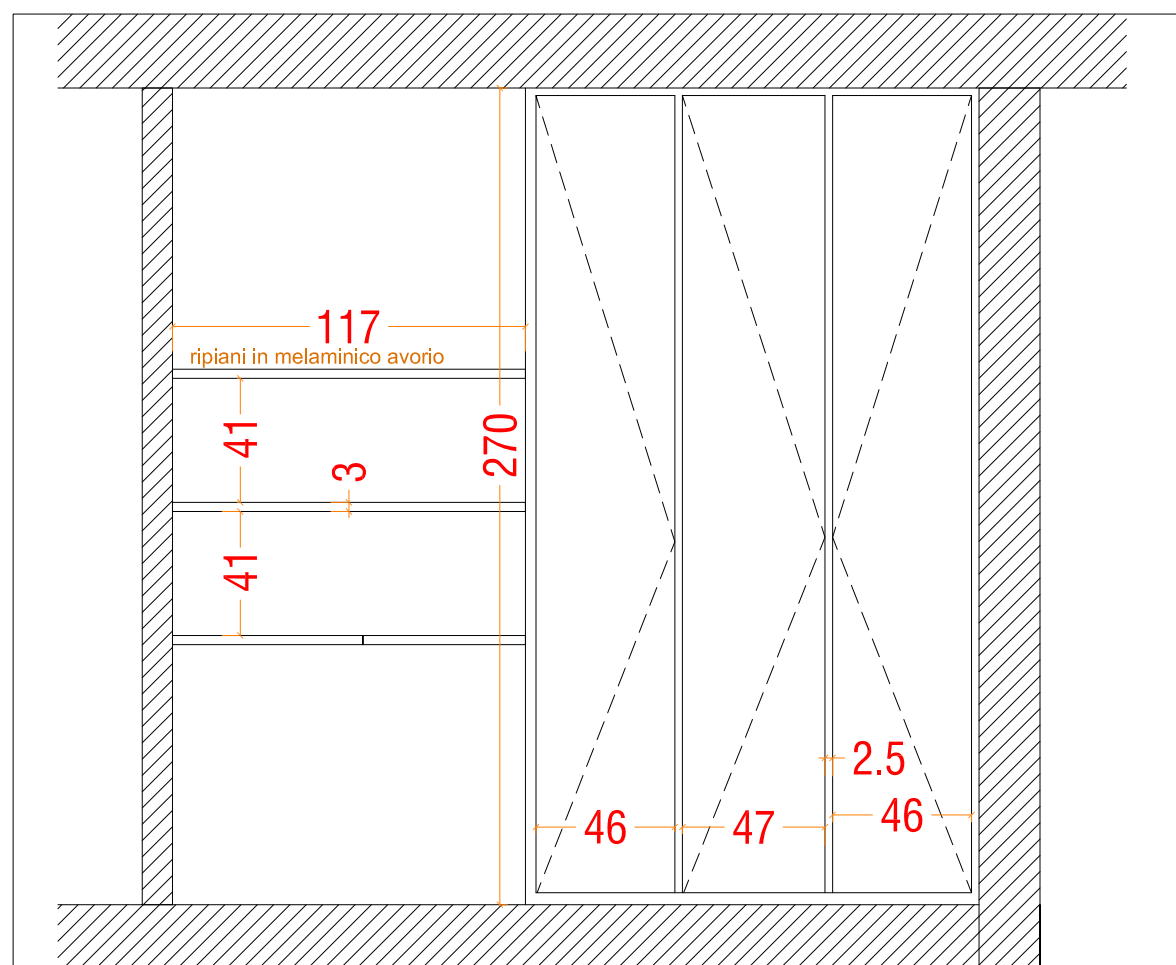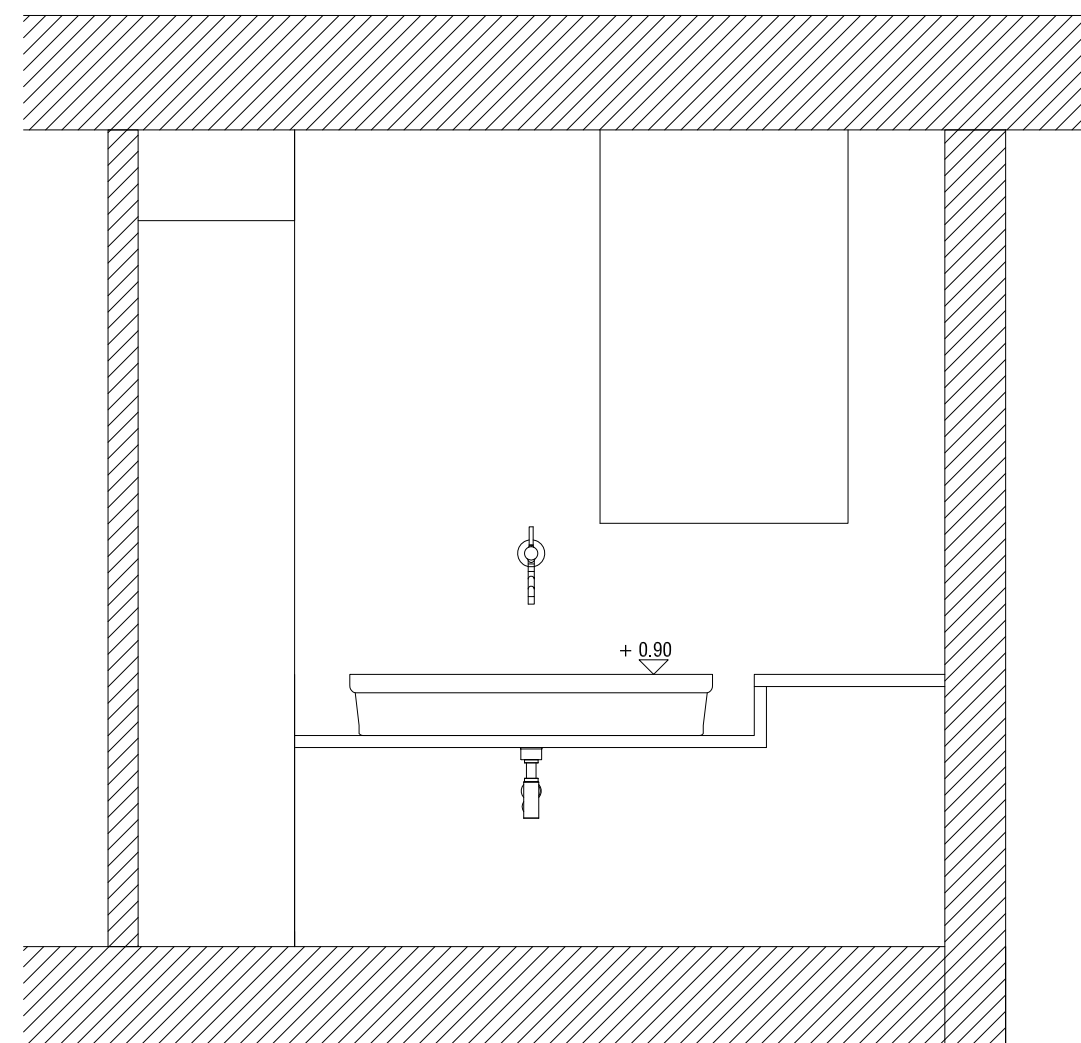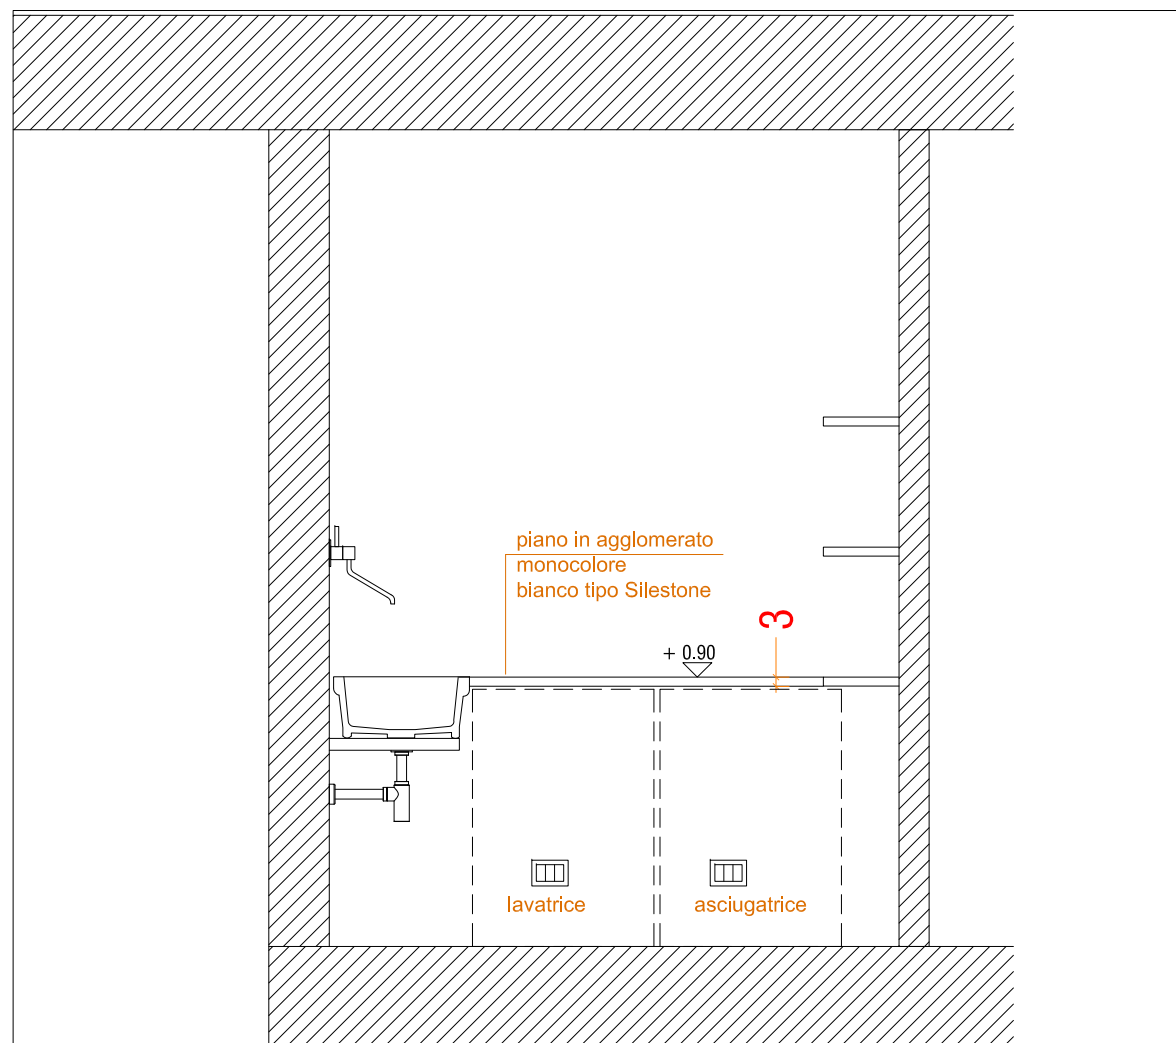

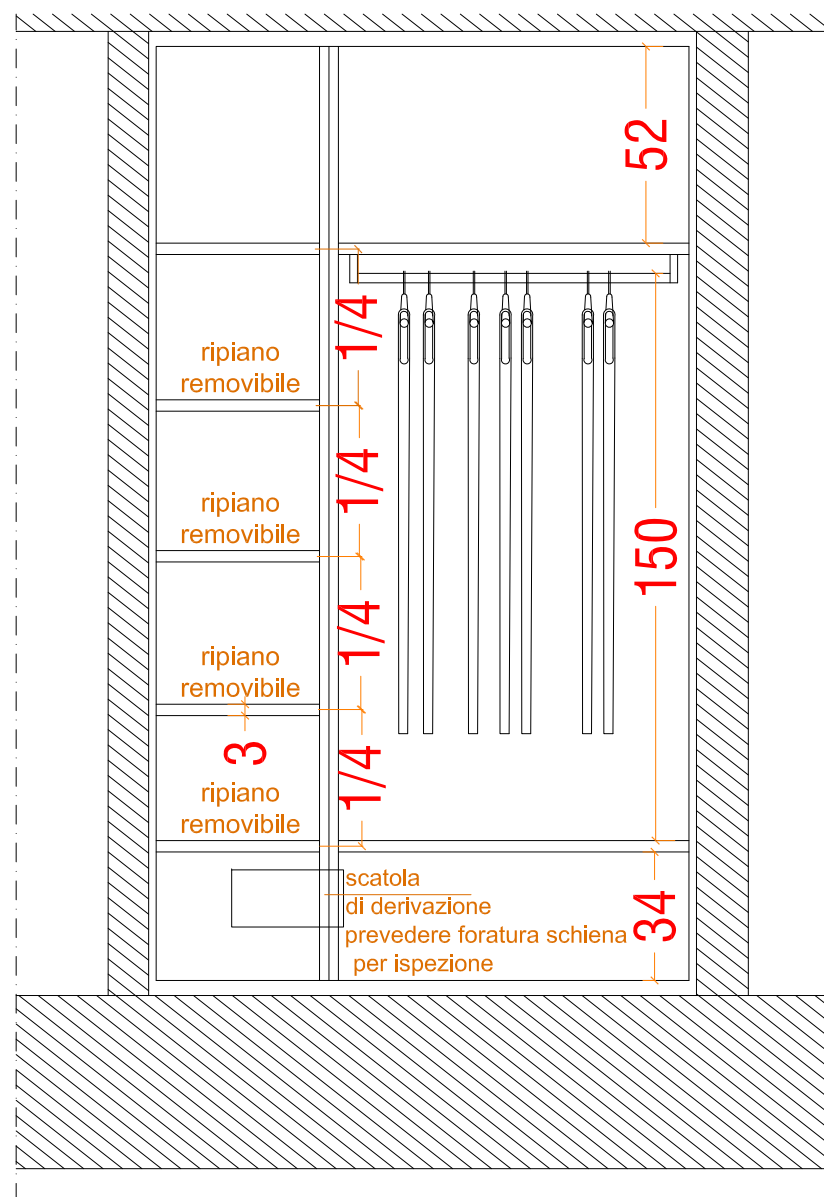

ante a battente
apertura gola
in mdf integgrate

